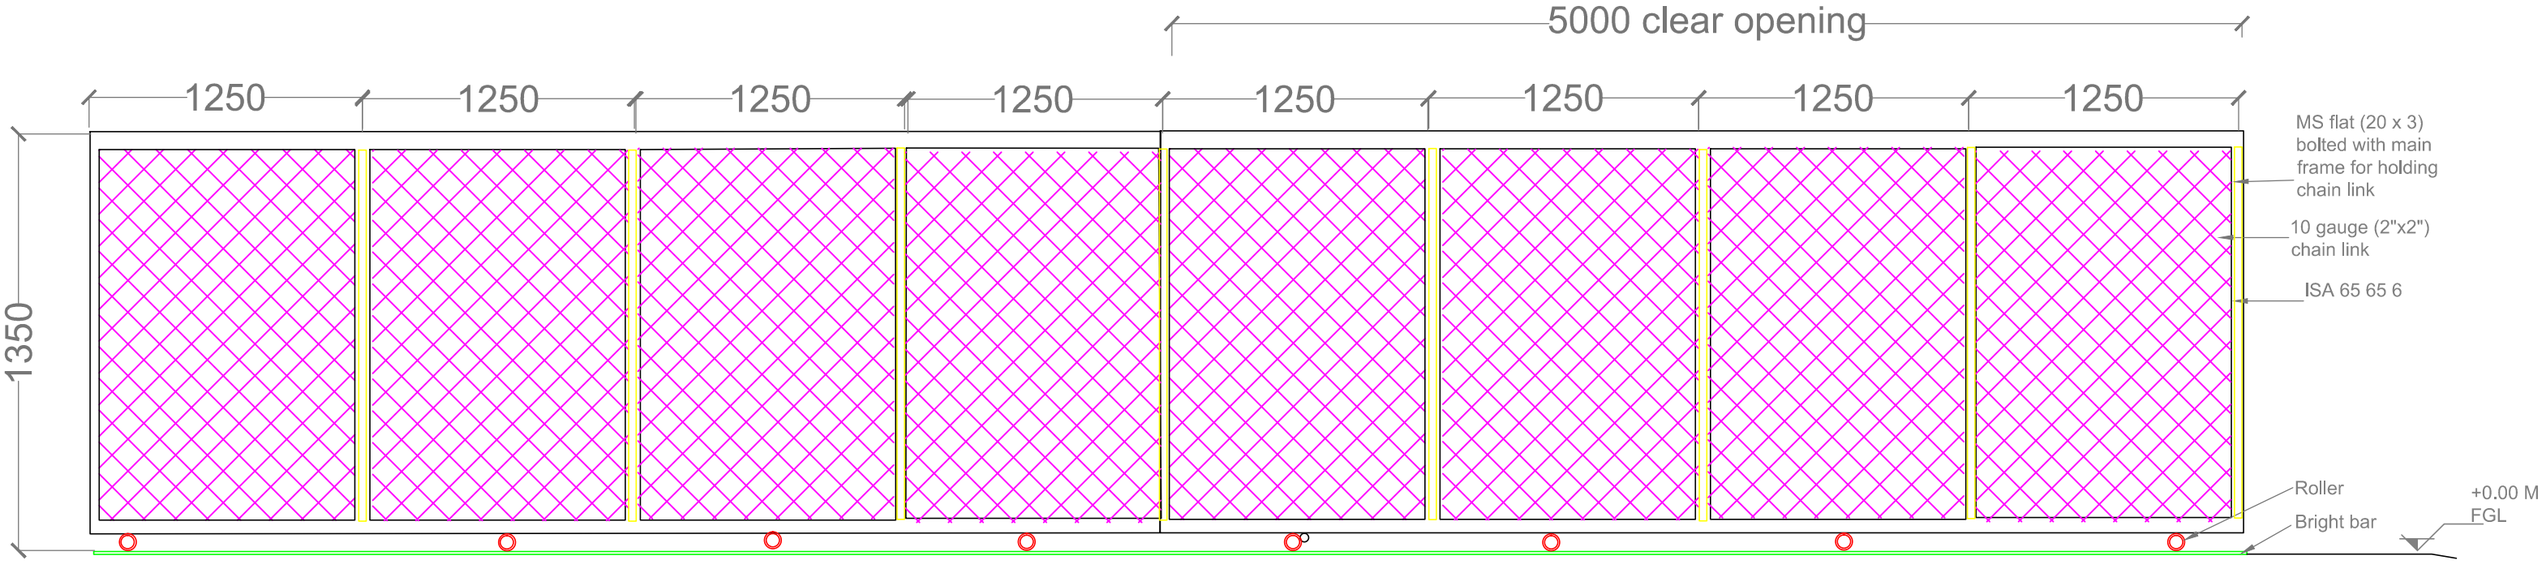


TYPICAL FENCED SLIDING GATE (5 m OPENING SIZE)