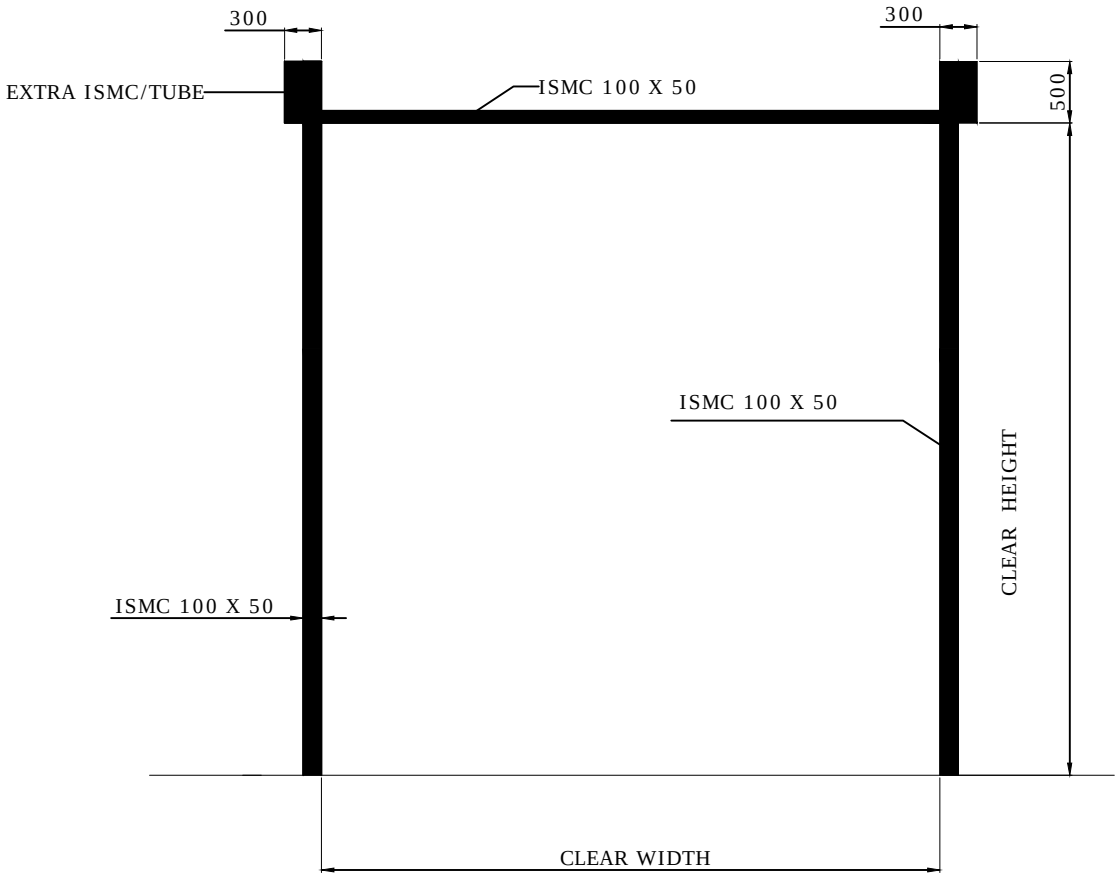

CLEAR WIDTH	CLEAR HEIGHT	QTY.
4000mm	3150mm	01NO

NOTE :

1. MATERIAL FOR ALL STRUCTURE = M.S
2. REQ. CIVIL WORK & M.S STRUCTURE WILL BE IN CLIENT SCOPE.

CLEAR WIDTH (CW)	CLEAR HEIGHT (CH)	QUANTITY
4000	3150	1 NO

TOLERANCE ±10 MM

This drawing & designing is the property of NIHVA TECHNOLOGIES. Not to be sold or copied to any other concern.

TITLE: MOTORIZED ROLLING SHUTTER STRUCTURE

NIHVA TECHNOLOGIES PVT. LTD. PUNE
Tel : 020 66304033
Email:- info@nihva.com
Website:- www.nihva.com

	NAME		DATE
DRAWN	P.A		19.12.19
CHECK	G.J		19.12.19
REV.			
APPROVAL			

If any queries contact : projects@nihva.com

ALL DIMENSION ARE IN mm

CLIENT - BSA

PROJECT -

SITE LOCATION - CHAKAN

DWG. NO. : NIHVA/19-20/0179

SCALE: NTS | WT: | SHEET: 01 OF 01