


PRODUCED BY AN AUTODESK EDUCATIONAL PRODUCT

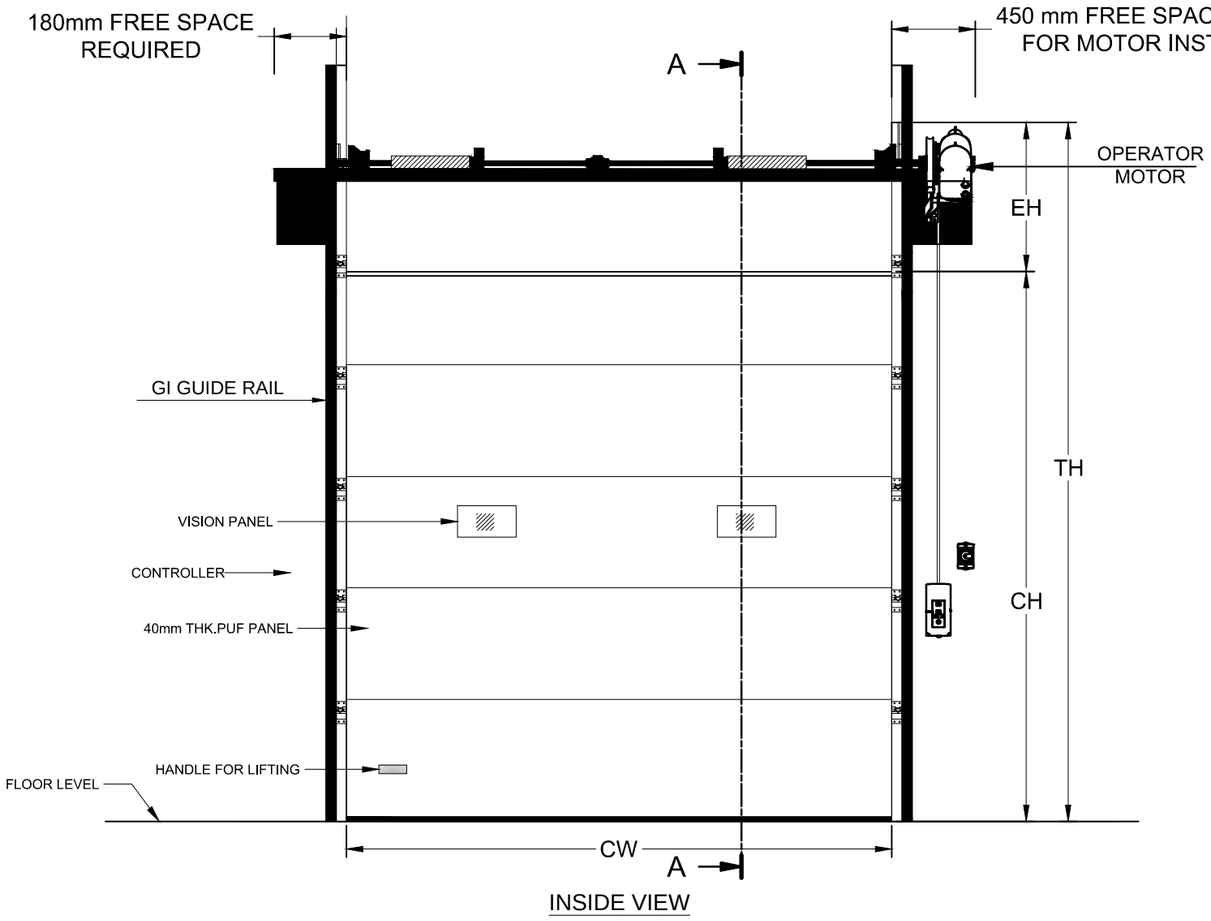

INSIDE VIEW

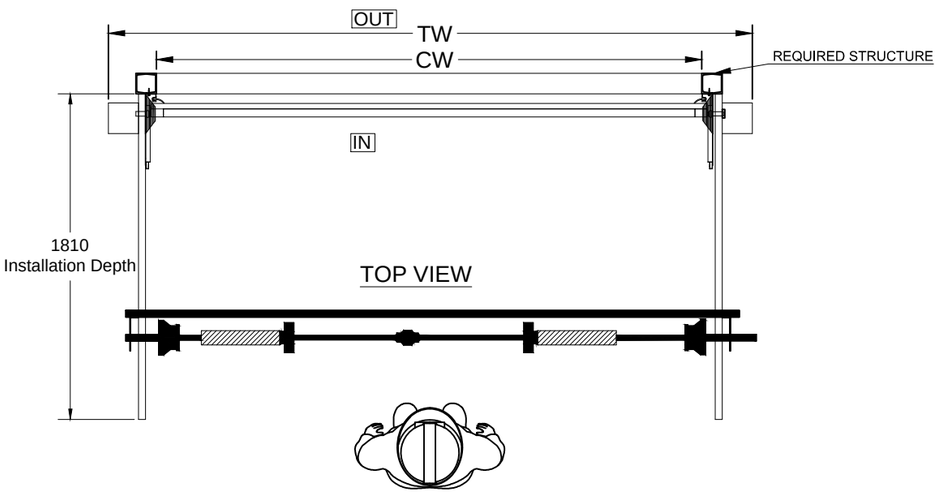

TOP VIEW

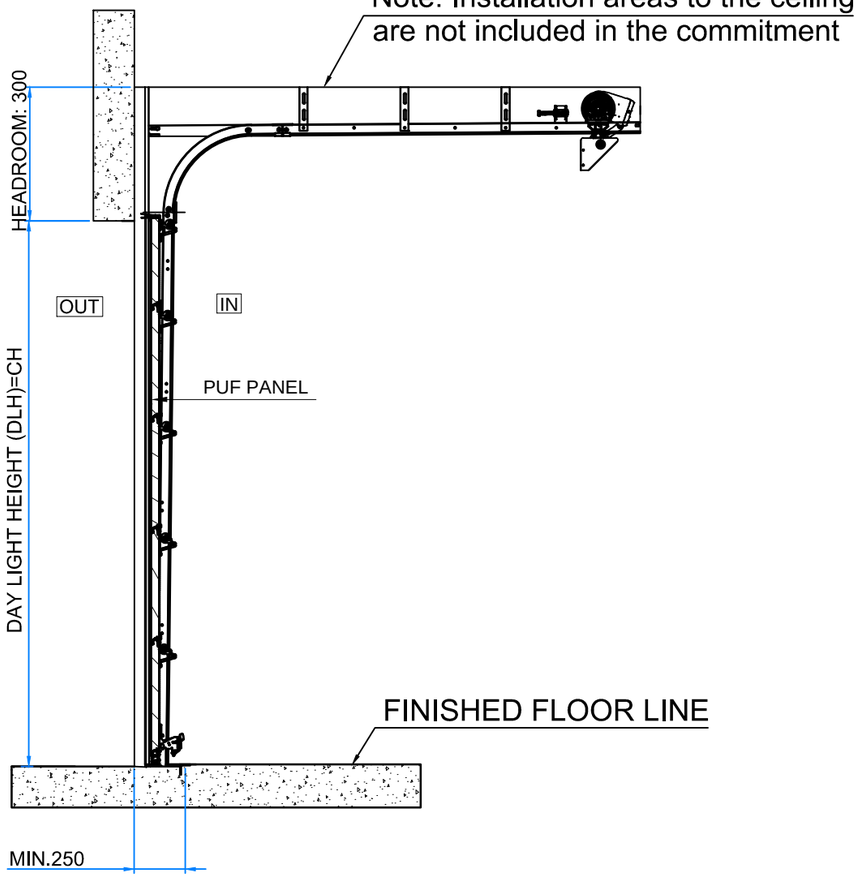

SECTION A-A

TOLERANCE: ± 10mm

SR NO	CLEAR WIDTH	CLEAR HEIGHT	QTY	TH	EH	CH
01	2600 mm	2480 mm	1	2780	300	3230

This drawing & design is the property of NIHVA TECHNOLOGIES. Not to be sold or copied to any other concern.

TITLE: SECTIONAL DOOR (LOW LIFTING)

	NAME	SIGN	DATE
DRAWN	AKASH		11.01.19
CHECK	VIKRANT		11.01.19
APPROVAL	R.D		11.01.19

NIHVA TECHNOLOGIES PVT. LTD.
NIHVA TECHNOLOGIES PVT. LTD. PUNE
Website:- www.nihva.com
Tel : 020 66304033
Email:- info@nihva.com

CLIENT - SURESBHAI DHEBARIWALA
PROJECT -
SITE - SURAT, GUJRAT
DWG. NO. : NIHVA/18-19/ REV: 0
If any queries contact : design@nihva.com
ALL DIMENSION ARE IN mm
SCALE: NTS WT: SHEET: 01 OF 01

PRODUCED BY AN AUTODESK EDUCATIONAL PRODUCT
PRODUCED BY AN AUTODESK EDUCATIONAL PRODUCT
PRODUCED BY AN AUTODESK EDUCATIONAL PRODUCT