
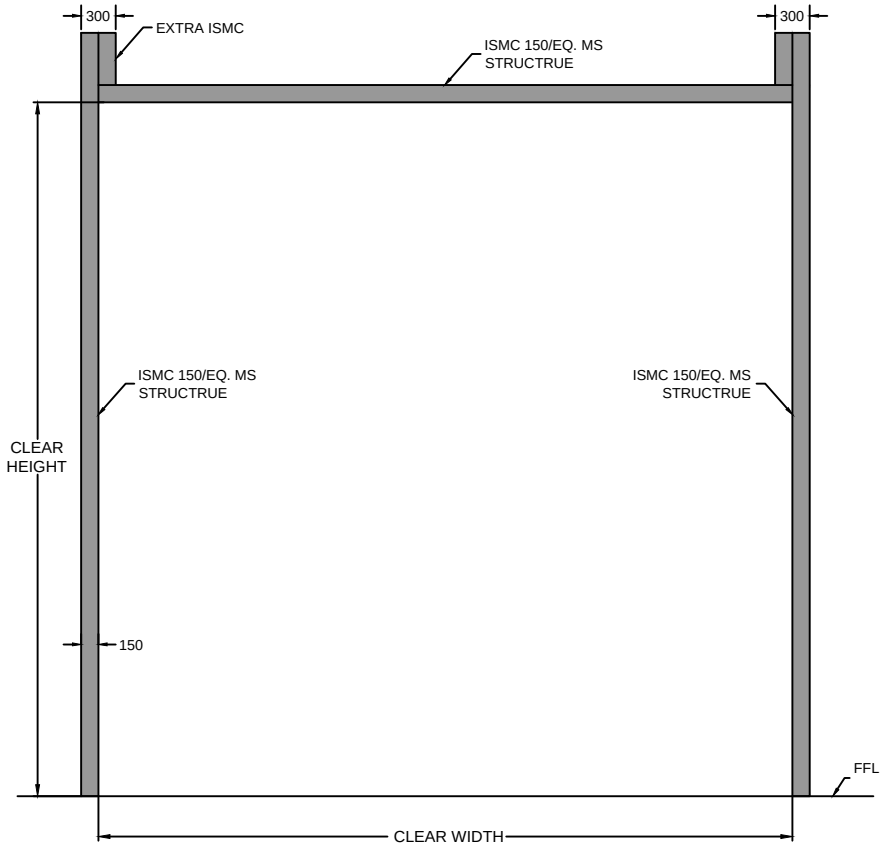


INSIDE ELEVATION

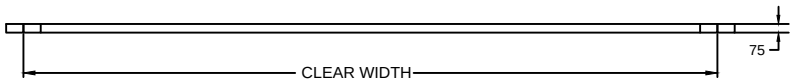

PLAN

SR NO.	CLEAR WIDTH	CLEAR HEIGHT	QUANTITY
1	6000 mm	6000 mm	01
2	4000 mm	5000 mm	01

TOLERANCE - ±10mm

This drawing & design is the property of NIHVA TECHNOLOGIES. Not to be sold or copied to any other concern.

TITLE: MS STRUCTURE FOR SECTIONAL DOOR

NIHVA TECHNOLOGIES PVT. LTD.

NIHVA TECHNOLOGIES PVT. LTD. PUNE
Tel : 020 66304033
Email:- info@nihva.com
Website:- www.nihva.com

	NAME	SIGN	DATE
DRAWN	OMKAR		
CHECK	PRADEEP		
APPRD.	SHEKHAR		

CLIENT - LM WIND POWER

PROJECT -

SITE LOCATION - GUJARAT

If any queries contact : design@nihva.com

DWG. NO. : NIHVA/17-18/0373 REV- 0

ALL DIMENSION ARE IN mm

SCALE: NTS WT: SHEET: 01 OF 01