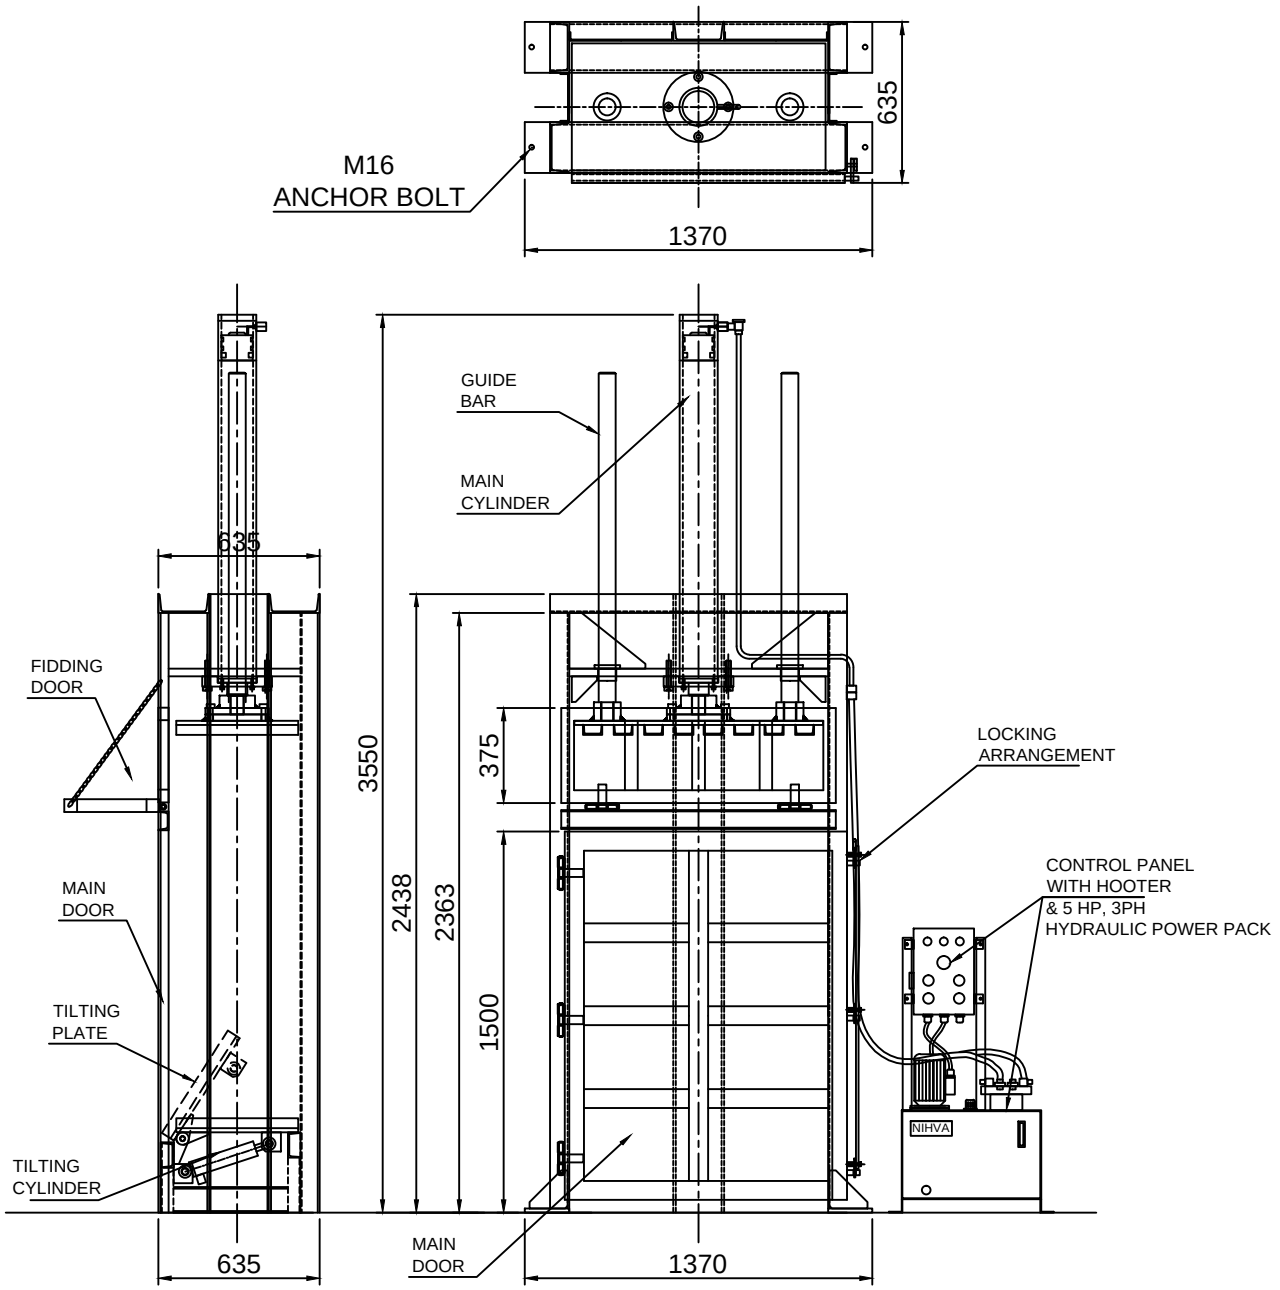

CAPACITY	20 TON
BAILING CHAMBER	1000L X 500W X 1500H
BAIL SIZE	1000L X 500W X 300H

This drawing & design is the property of NIHVA TECHNOLOGIES. Not to be sold or copied to any other concern.

TITLE
BAILING PRESS

NIHVA
NIHVA TECHNOLOGIES PVT. LTD.

NIHVA TECHNOLOGIES
PVT. LTD. PUNE
Tel : 020 66304033
Email:- info@nihva.com
Website:- www.nihva.com

	NAME	SIGN	DATE
DRAWN	P.A		18.09.2019
CHECK	G.J		18.09.2019
APPRD.			

CLIENT - IKEA
PROJECT -
SITE LOCATION -

If any queries contact : design@nihva.com
DWG. NO. :NIHVA/19-20/0096
REV- 0

ALL DIMENSION ARE IN mm
SCALE: NTS
WT:
SHEET: 01 OF 01