

PEB

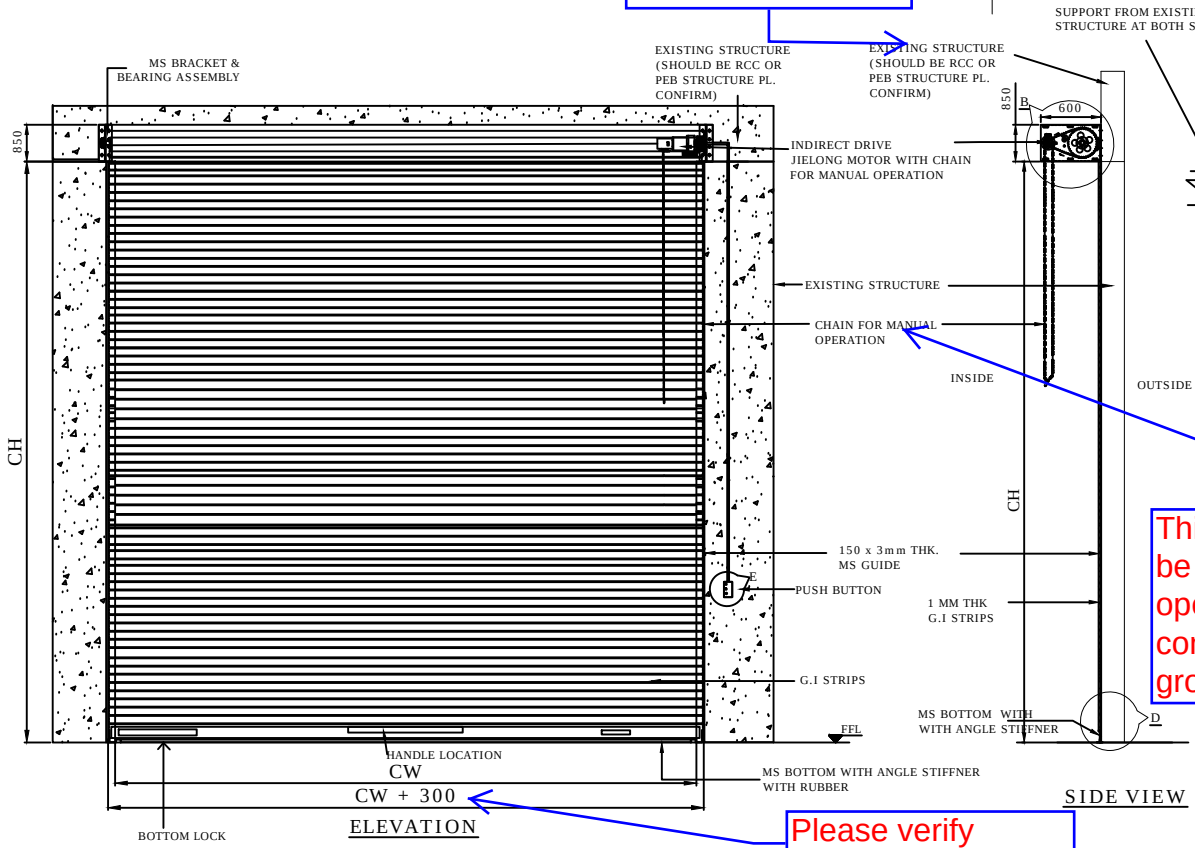


ELEVATION


SIDE VIEW

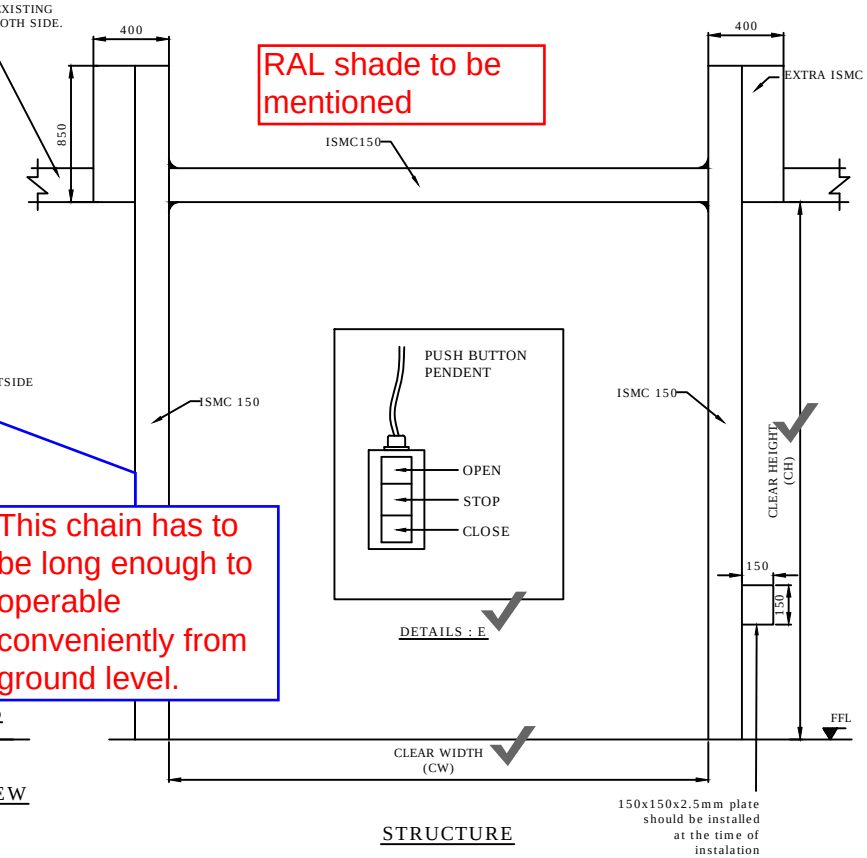


STRUCTURE

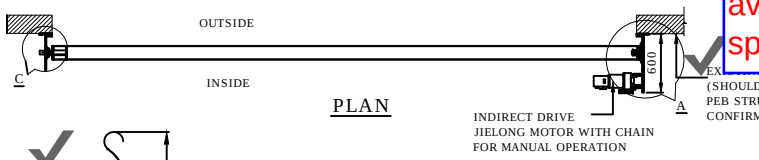


PLAN

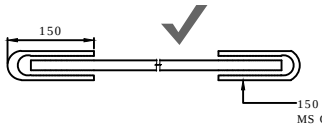


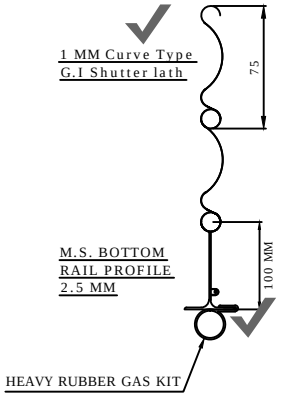

DETAILS : D

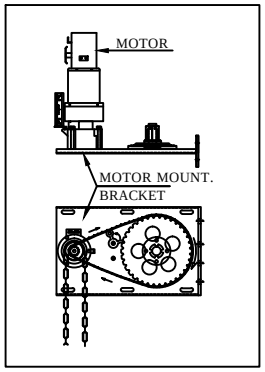

DETAILS : A & B

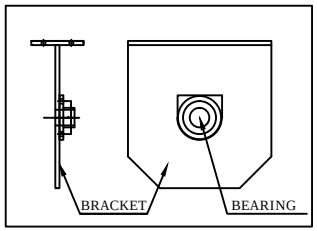

DETAILS : C

(NOTE: REQUIRED TECHANICAL STRUCTURE FOR SHUTTER IN CLIENT SCOPE)

This chain has to be long enough to operable conveniently from ground level.

Please verify availability of this space at site

By WPI

4500	6000	3	RAL -
CLEAR WIDTH (CW)	CLEAR HEIGHT (CH)	QUANTITY	RAL COLOR

This drawing & design is the property of NIHVA TECHNOLOGIES. Not to be sold or copied to any other concern.

TITLE	MOTORIZED ROLLING SHUTTER			NIHVA TECHNOLOGIES PVT. LTD. PUNE Tel : 020 66304033 Email:- info@nihva.com Website:- www.nihva.com
	NAME	SIGN	DATE	
DRAWN	P.A		19.11.2019	CLIENT - WANI
CHECK	G.J		19.11.2019	PROJECT - BRIDGESTONE
APPRD.				SITE LOCATION - CHAKAN
If any queries contact : design@nihva.com				DWG. NO. : NIHVA/19-20/0155 REV- R00
ALL DIMENSION ARE IN mm				SCALE: NTS WT: SHEET: