



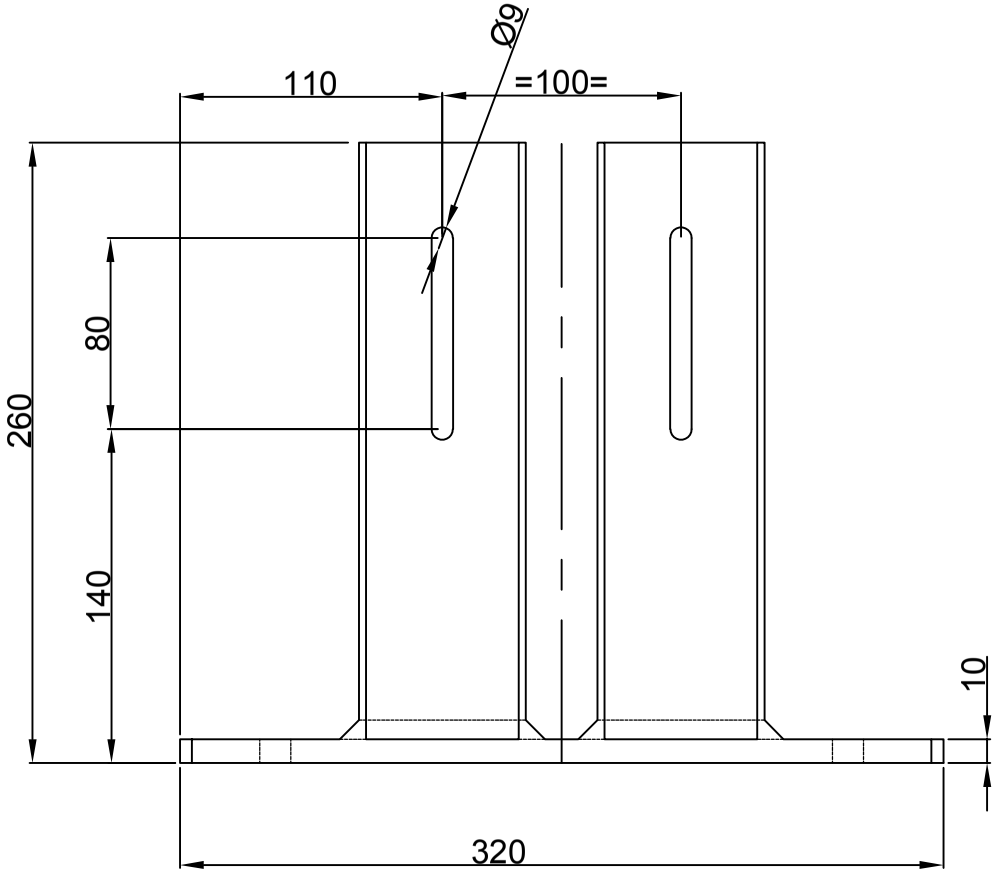

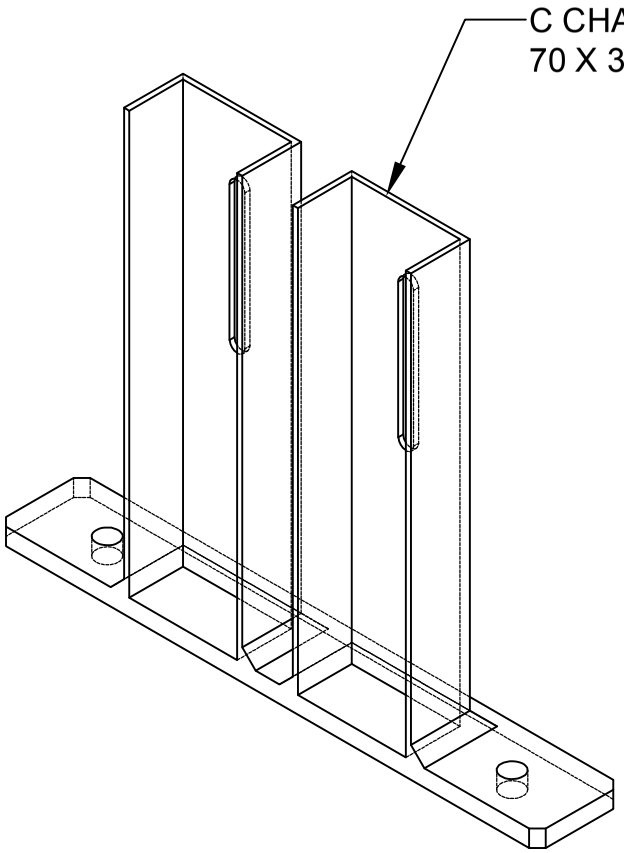

C CHANNEL FRAME-01
MATL-MS
QTY-11
DRG NO-01-01

SR NO.	REV NO.	Date	Revised By

TITLE:- C CHANNEL FRAME-01

NIHVA TECHNOLOGIES PVT. LTD.

NIHVA TECHNOLOGIES PVT. LTD. PUNE
Tel : 020 66304033
Email:- info@nihva.com
Website:- www.nihva.com

	NAME	DATE	SIGN
DRAWN	KISHAN	20/07/22	
CHECK	G. JAIN	20/07/22	
APPRD.	V. TARAK		

If any queries contact : design@nihva.com

ALL DIMENSION ARE IN mm

CLIENT - NIHVA TECHNOLOGIES PVT.LTD
LOCATION -
PRODUCT - RETRACTABLE ROOF
DWG NO:-NIHVA/22-23/MFG/0036
SCALE: NTS | SCALE:-- 1:1 | SHEET: