



DRAWING


REV DESCRIPTION	DATE	REV NO
	05-06-2026	REV 00
1.		

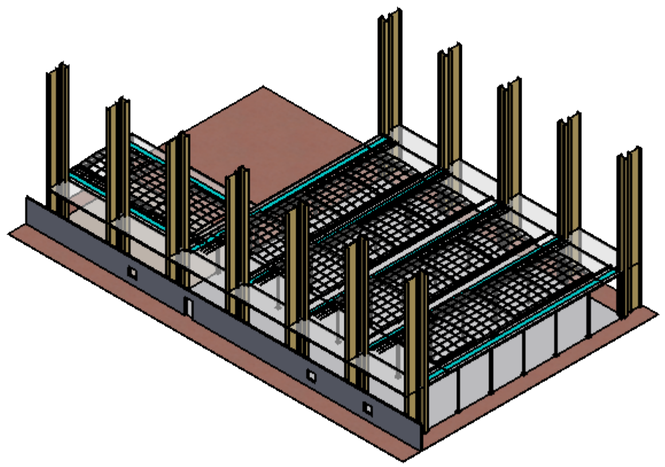


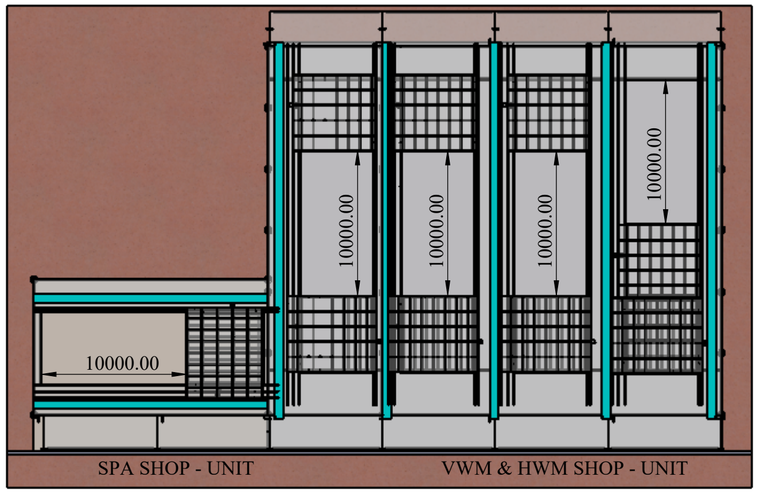


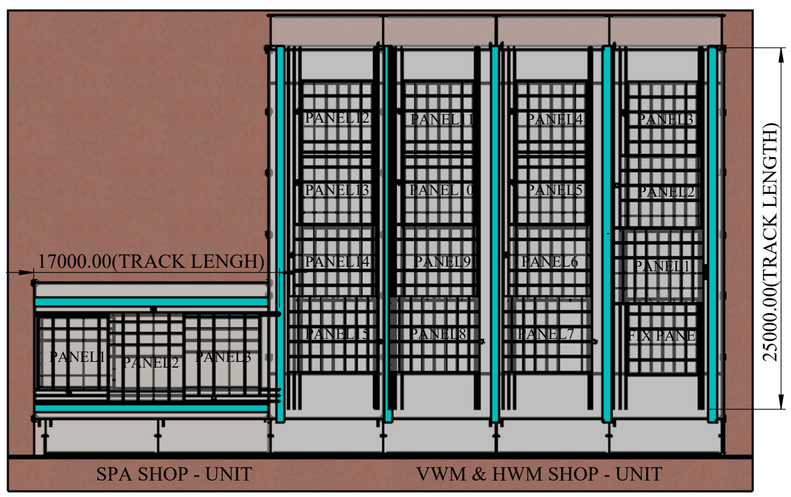

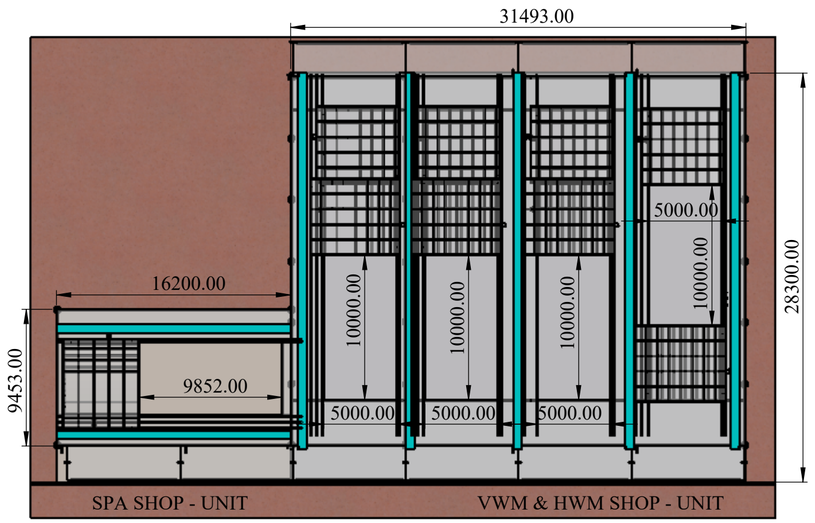

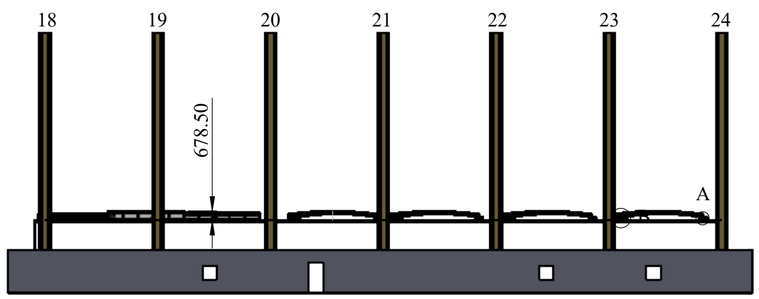

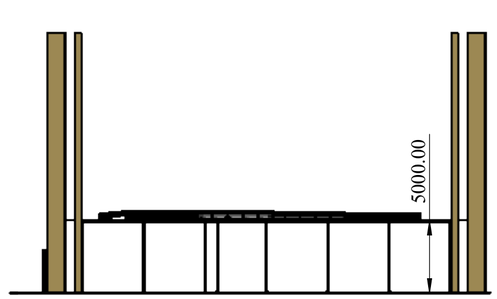

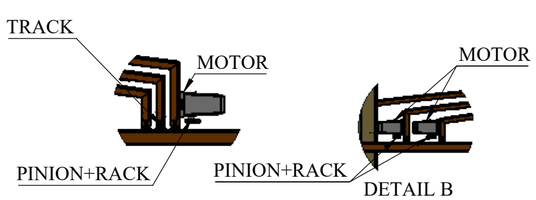

DETAIL A
SCALE 1 : 30

DETAIL B
SCALE 1 : 50


NOTE :

SPECIAL INSTRUCTION'S :

This drawing & design is the property of NIHVA TECHONOLOGIES PVT. LTD. Not to be sold or copied to any other concern

TITLE - ROOF AUTOMATION				NIHVA Technologies Pvt. Ltd.	NIHVA TECHNOLOGIES PVT.LTD.PUNE Website - www.nihva.com
DWG NO - NTPL-000-PM-001					
	NAME	SIGNATURE	DATE	PRODUCT - RETRACTABLE ROOF	
DRAWN	V.W.		05-06-2026	PROJECT NO - NTPL-000-PM	REVISION - 00
CHK'D	S.P.		06-06-2026	SITE LOCATION -	WEIGHT -
APPV'D	V.T.		06-06-2026	MATRIAL -	QTY - 1
If any queries contact - info@nihva.com				PROJECTION METHOD:	SCALE :
ALL DIMENSION ARE IN mm			A2		SHEET 1 OF 2

DRAWING

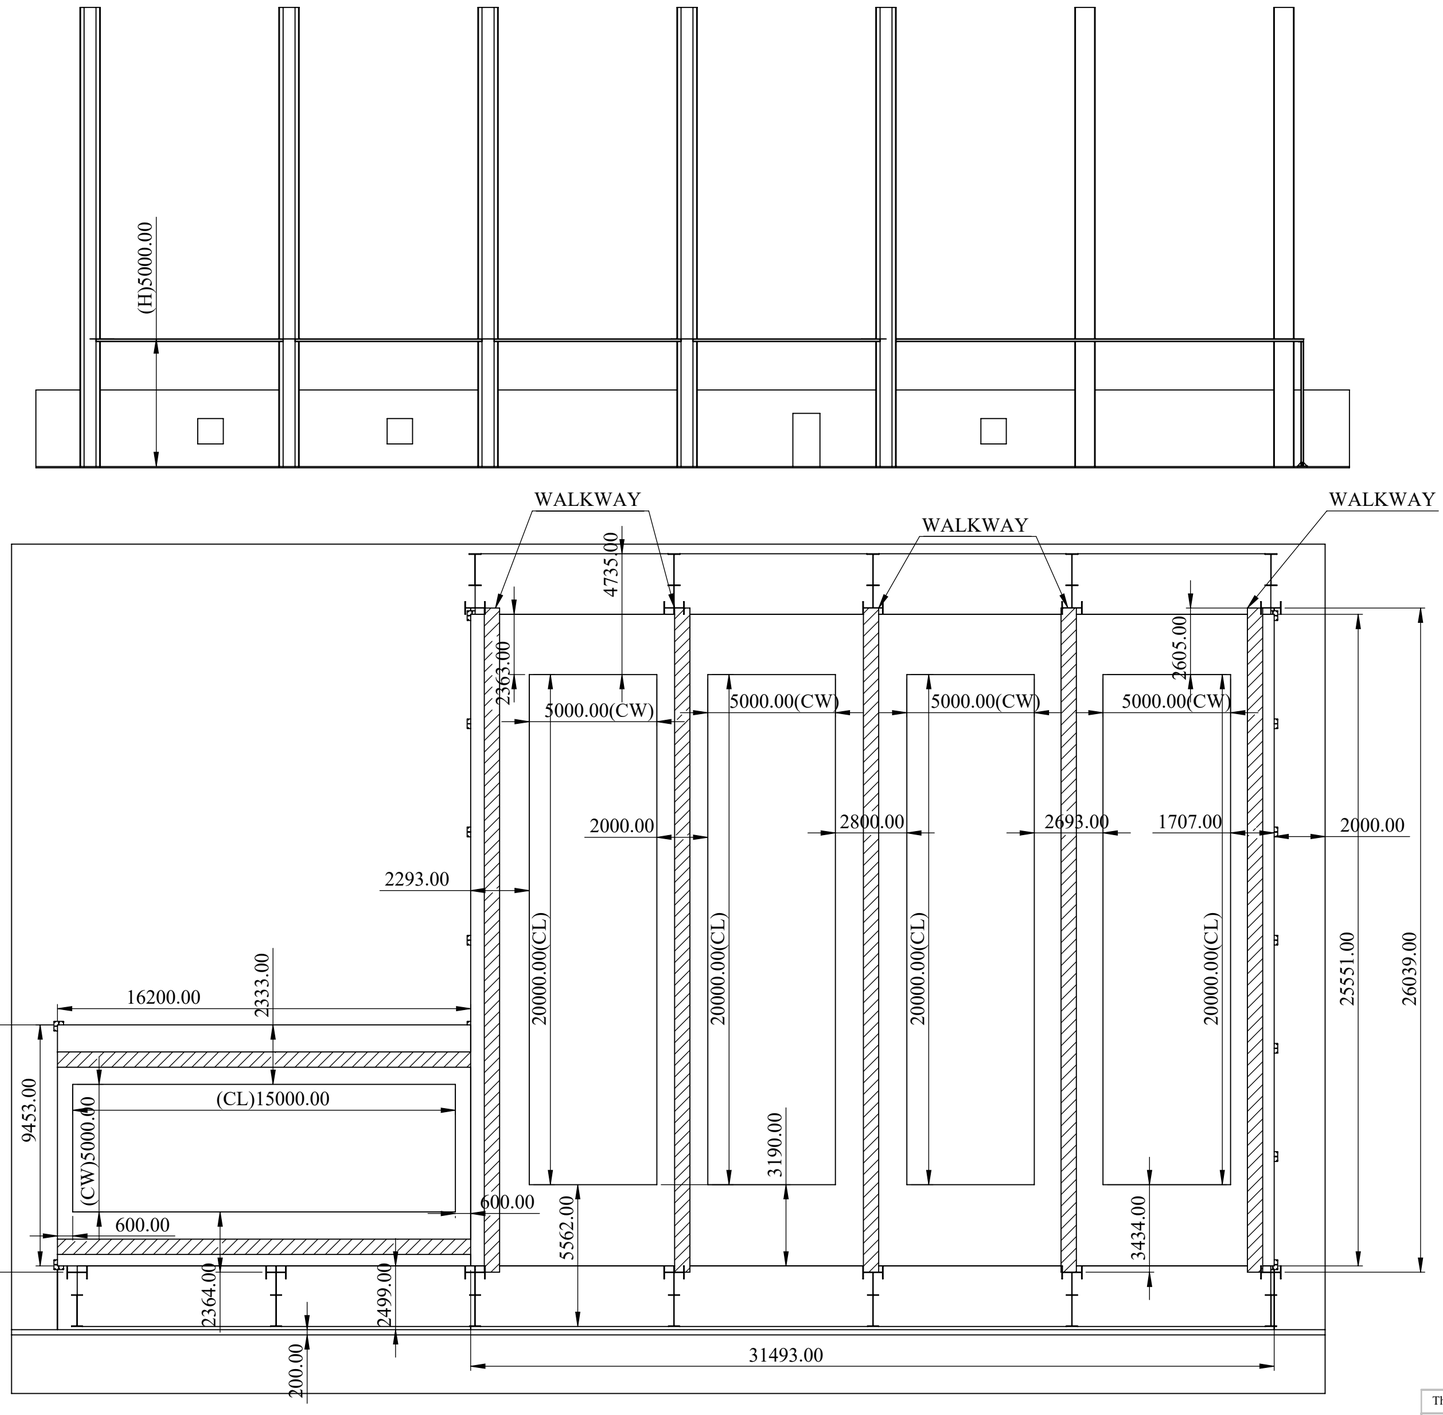

REV DESCRIPTION	DATE	REV NO
	05-06-2026	REV 00
1.		

NOTE :

BASE STRUCTURE IN CLIENT SCOPE

SPECIAL INSTRUCTION'S :

This drawing & design is the property of NIHVA TECHONOLOGIES PVT. LTD. Not to be sold or copied to any other concern

TITLE - ROOF AUTOMATION

DWG NO - NTPL-000-PM-001

NIHVA TECHNOLOGIES PVT.LTD.PUNE
Website - www.nihva.com

	NAME	SIGNATURE	DATE
DRAWN	V.W.		05-06-2026
CHK'D	S.P.		06-06-2026
APPV'D	V.T.		06-06-2026

PRODUCT - RETRACTABLE ROOF

PROJECT NO - NTPL-000-PM | REVISION - 00

SITE LOCATION - | WEIGHT -

MATRIAL - | QTY - 1

If any queries contact - info@nihva.com

ALL DIMENSION ARE IN mm | A2

PROJECTION METHOD:

SCALE :