
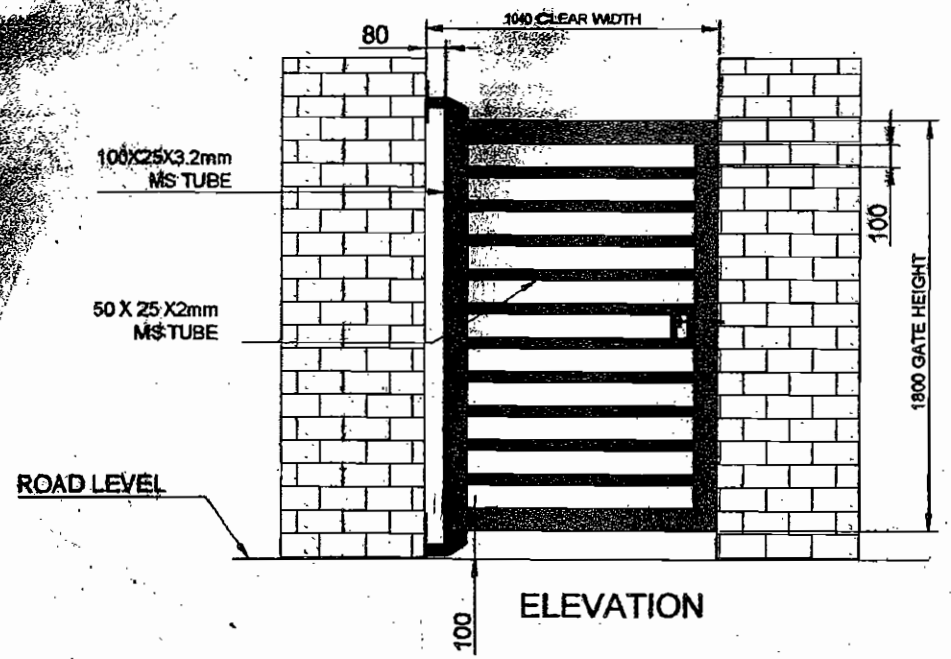


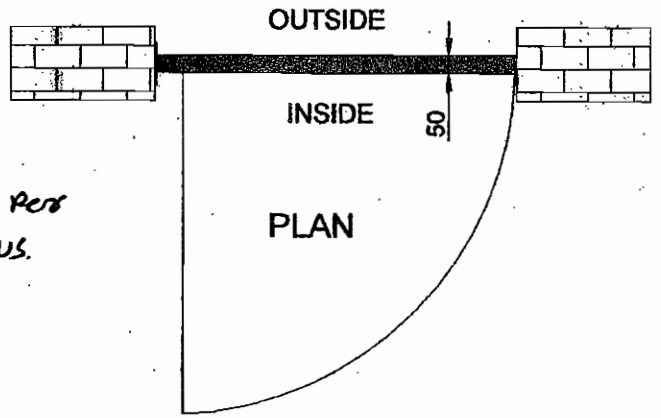

O.K.

Tube section shall be as per drawing given by us.

Sagar Gaud

SR NO	TUBE SPECIFICATION	
1	100X50X3.2mm	OUTER FRAME
2	50X25X2mm	INNER PATTERN

REV.01.- TUBE SIZE CHANGED
REV.02.- SIZE CHANGED AS PER SITE CONDITION

CLEAR WIDTH	CLEAR HEIGHT	QUANTITY
1040	1800	02 NOS

Color Scheme - RSS
Color - Grey.

DIMENSION :

CLEAR WIDTH	CLEAR HEIGHT	QUANTITY
1040	1800	02 NOS

MATERIAL :

THICKNESS :

NOTE-
1. ALL REQUIRED CIVIL WORK WILL BE IN CLIENTS SCOPE.

NIHVA
NIHVA TECHNOLOGIES PVT. LTD.
NIHVA TECHNOLOGIES PVT. LTD. PUNE.
Email- info@nihva.com
Website:- www.nihva.com

TITLE:

WICKET GATE


CLIENT'S APPROVAL :

CLIENT - SHILCHAR TECHNOLOGIES LTD.
PROJECT -
SITE LOCATION -VADODARA
DWG. NO. : NIHVA/17-18/0159/R02


SCALE: NTS	WT:	SHEET: 1 OF 1
DRAWN BY: OMKAR		DATE: 24-08-2017
CHECK BY: SHEKHAR		DATE: 24-08-2017
APPROVED BY : SHEKHAR		DATE: 24-08-2017

If any queries contact : projects@nihva.com
NOTE: ALL DIMENSIONS ARE IN mm

THIS DRAWING & DESIGNING IS THE PROPERTY OF NIHVA TECHNOLOGIES. NOT TO BE SOLD OR COPIED TO ANY OTHER CONCERN.

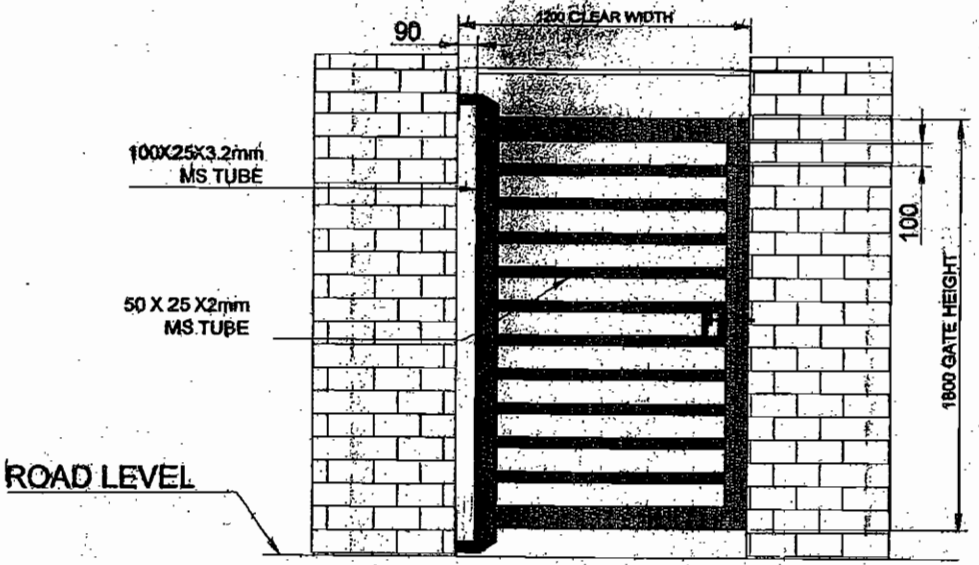

ELEVATION

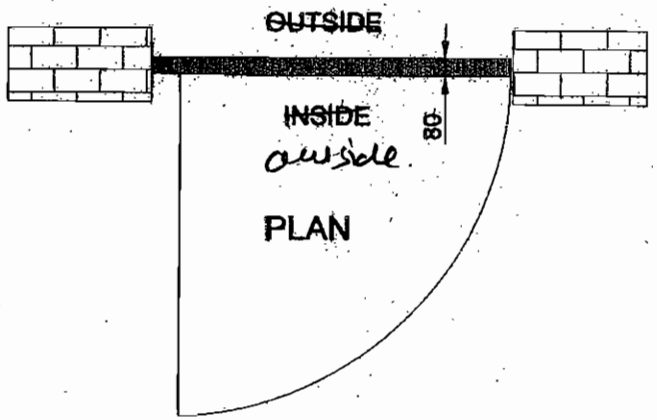

PLAN

O.C

Tube section should be as per our drawing.

Sagar Gaikwad

Color Scheme. RSS

Color - grey.

SR NO	TUBE SPECIFICATION	
1	100X50X3.2mm	OUTER FRAME
2	50X25X2mm	INNER PATTERN

REV.01.- TUBE SIZE CHANGED

CLEAR WIDTH	CLEAR HEIGHT	QUANTITY
1200	1800	02 NOS

DIMENSION :

CLEAR WIDTH	CLEAR HEIGHT	QUANTITY
1200	1800	02 NOS

MATERIAL :

THICKNESS :

NOTE-
1. ALL REQUIRED CIVIL WORK WILL BE IN CLIENTS SCOPE.

NIHVA TECHNOLOGIES PVT. LTD.

NIHVA TECHNOLOGIES PVT. LTD. PUNE
Email:- info@nihva.com
Website:- www.nihva.com

TITLE:

WICKET GATE

CLIENT'S APPROVAL :

CLIENT - SHILCHAR TECHNOLOGIES LTD.

PROJECT -

SITE LOCATION -VADODARA

DWG. NO. : NIHVA/17-18/0159/R01

SCALE: NTS	WT:	SHEET:1 OF 1
DRAWN BY: OMKAR		DATE: 24-08-2017
CHECK BY: SHEKHAR		DATE: 24-08-2017
APPROVED BY : SHEKHAR		DATE: 24-08-2017

If any queries contact : projects@nihva.com

NOTE: ALL DIMENSIONS ARE IN mm

THIS DRAWING & DESIGNING IS THE PROPERTY OF NIHVA TECHNOLOGIES, NOT TO BE SOLD OR COPIED TO ANY OTHER CONCERN.


DOCK LEVELER SIZE	WIDTH (W)	LENGTH (L)	HEIGHT (H)	LIP (C) LENGTH	BUFFER SIZE (OPTIONAL)
	2000	3000	480	400	200X300X100


Included

PIT DIMENSION	WIDTH (W1)	LENGTH (L1)	DEPTH (D)	ALL DIMENSIONS ARE IN mm
	2050	3070	485	

Section at A-A


75x75x6 Angle - Anchored

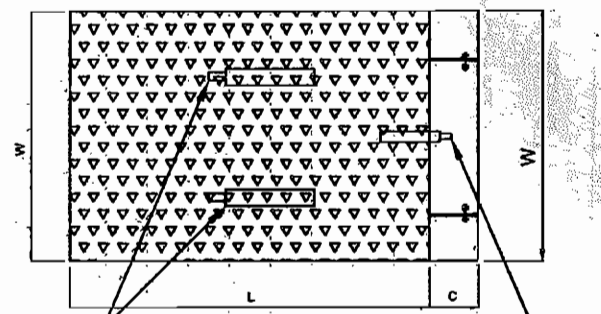


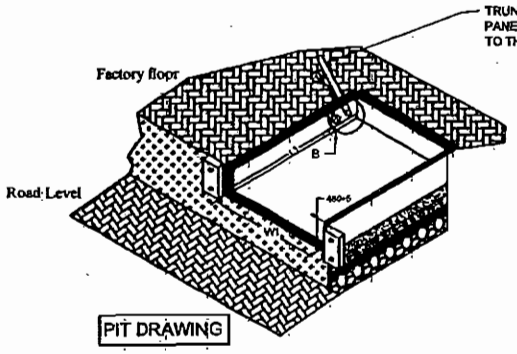

PIT DRAWING

VIEW B

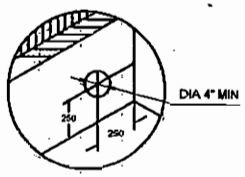

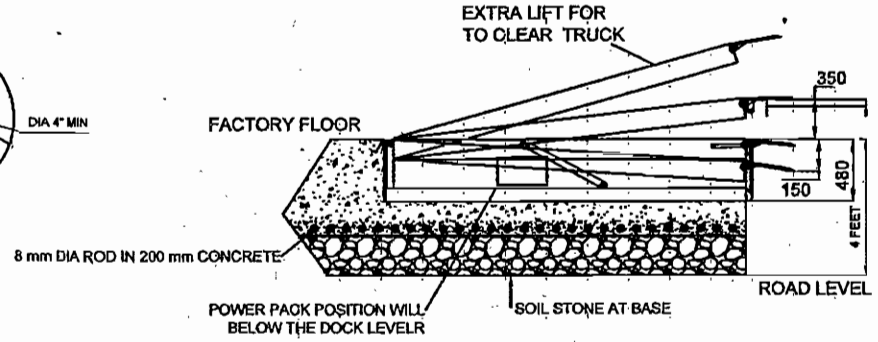

O.K
Sagar gokul
Dues

NOTE:-
1. PROPER DRAINAGE SHOULD BE DONE
2. TRENCH AS SHOWN SHOULD BE MADE BY DECIDING THE POWER PACK POSITION (SUPPLY CABLE LENGTH STD. 7000 MM)
3. LEVEL OF THE PIT SHOULD BE PLAIN AND SHOULD TAKE AT LEAST 12000 KG FLOOR LOADING
4. MOUNTING ARRANGEMENT FOR BUFFERS SHOULD BE MADE AS PER BUFFER DRAWING (IF ORDERED)
5. FABRICATION TOLERANCE FOR PLATFROM SIZE WILL BE ± 15 MM

DOCK LEVELER- 10 TON CAPACITY -

CLIENT APPORVAL-	DATE	SIGN.	NIHVA TECHNOLOGIES PVT. LTD.	NIHVA TECHNOLOGIES PVT. LTD. PUNE Tel : 020 66304033 Email:- info@nihva.com Website - www.nihva.com
DRAWN :- SURAJ	22/08/2017			
CHECKED :- SHEKHAR	22/08/2017		CLIENT -SHILCHAR TECHNOLOGIES LTD.	
APPROVED :- SHEKHAR	22/08/2017		PROJECT -	
ALL DIMENSION ARE IN mm			SITE LOCATION -VADODARA.	
If any queries contact : projects@nihva.com			DWG. NO. - NIHVA/17-18/0164	

Colour scheme :- PS 5
Colour - Yellow.


O.K.

Control Panel:-
Location shall be
different than
shown in drawing.


Sagar J Gohil

option # 4.


OPTION 1

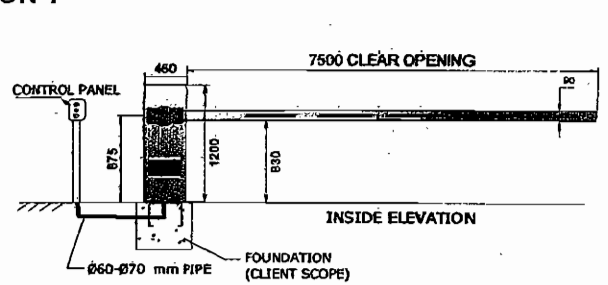


OPTION 2

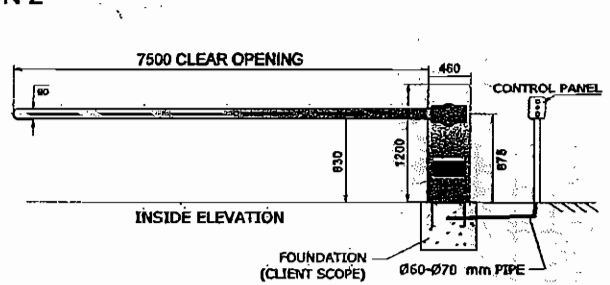


OPTION 3

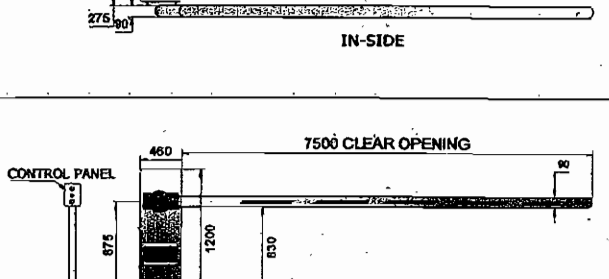

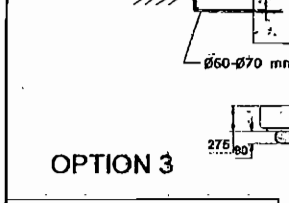

FOUNDATION (CLIENT SCOPE)


OPTION 4

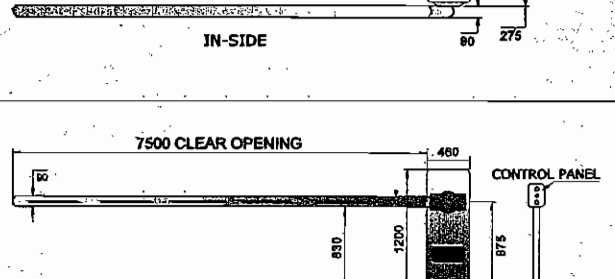



NOTE- CLIENT SHOULD SELECT POSITION OF BOOM BARRIER OUT OF OPTIONS.

This drawing is design is the property of NIHVA TECHNOLOGIES. Not to be sold or copied to any other concern.

TITLE: BOOM BARRIER			NIHVA TECHNOLOGIES PVT. LTD. PUNE
	SIGN	DATE	NIHVA TECHNOLOGIES PVT. LTD. Tel : 020 66304033 Email:- info@nihva.com Website:- www.nihva.com
DRAWN	SURAJ	29/08/17	CLIENT -SHILCHAR TECHNOLOGIES LTD.
CHECK	SHEKHAR	29/08/17	PROJECT -
REV.			SITE LOCATION - VADODARA.
APPROVAL	SHEKHAR	29/08/17	DWG. NO. : NIHVA/17-18/0165/R02
If any queries contact : projects@nihva.com			SCALE: NTS WT: SHEET: 01 OF 01
ALL DIMENSION ARE IN mm			

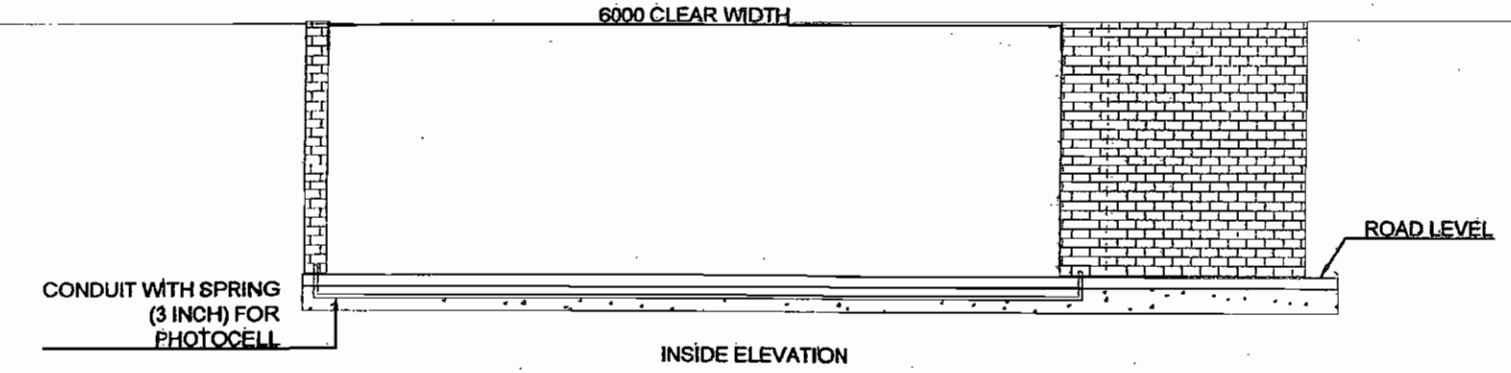

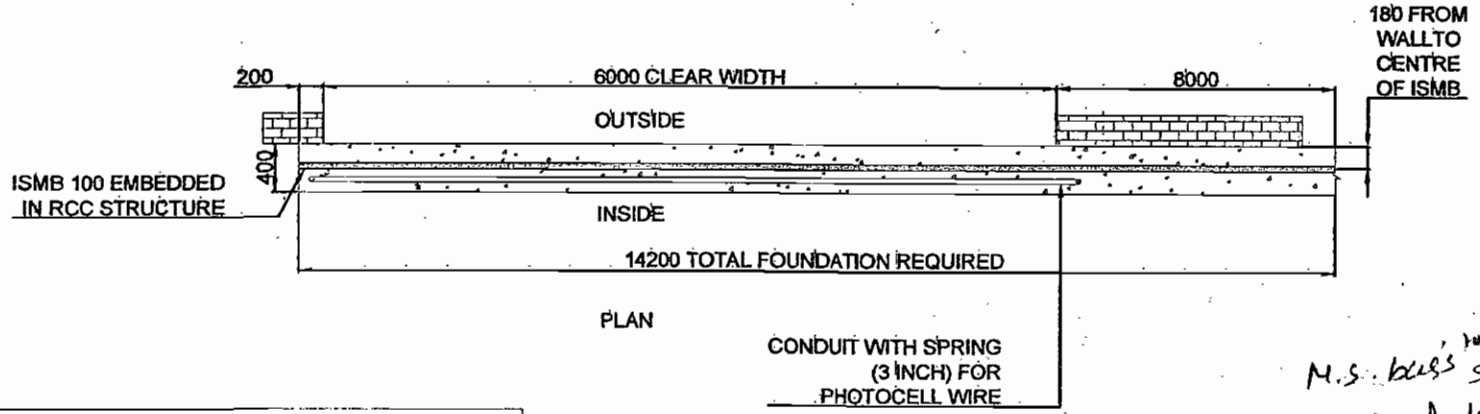

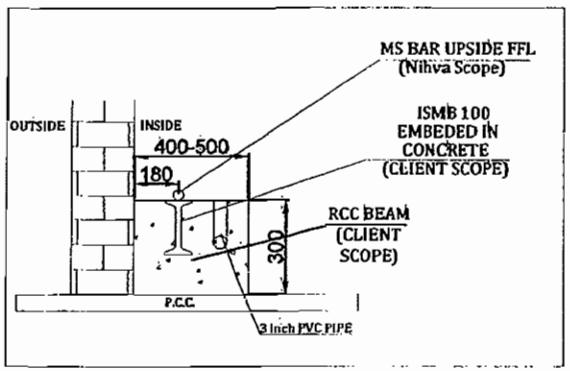

6.0m SLIDING GATE FOUNDATION

M.S. bar's top shall be at finished road level


Suggested

This drawing & design is the property of NIHVA TECHNOLOGIES. Not to be sold or copied to any other concern.


TITLE	FOUNDATION FOR 6M SLIDING GATE		
	SIGN	DATE	
DRAWN	OMKAR	31/08/17	
CHECK	SHEKHAR	31/08/17	
REV.			
APPROVAL	SHEKHAR	31/08/17	
If any queries contact : projects@nihva.com			
ALL DIMENSION ARE IN mm			

NIHVA
NIHVA TECHNOLOGIES PVT. LTD.
NIHVA TECHNOLOGIES PVT. LTD. PUNE
Tel : 020 66304033
Email:- info@nihva.com
Website:- www.nihva.com


CLIENT - SHILCHAR TECHNOLOGIES LTD.
PROJECT -
SITE - VADODARA
DWG. NO. : NIHVA/17-18/0190
SCALE: NTS | WT: | SHEET: 01 OF 01

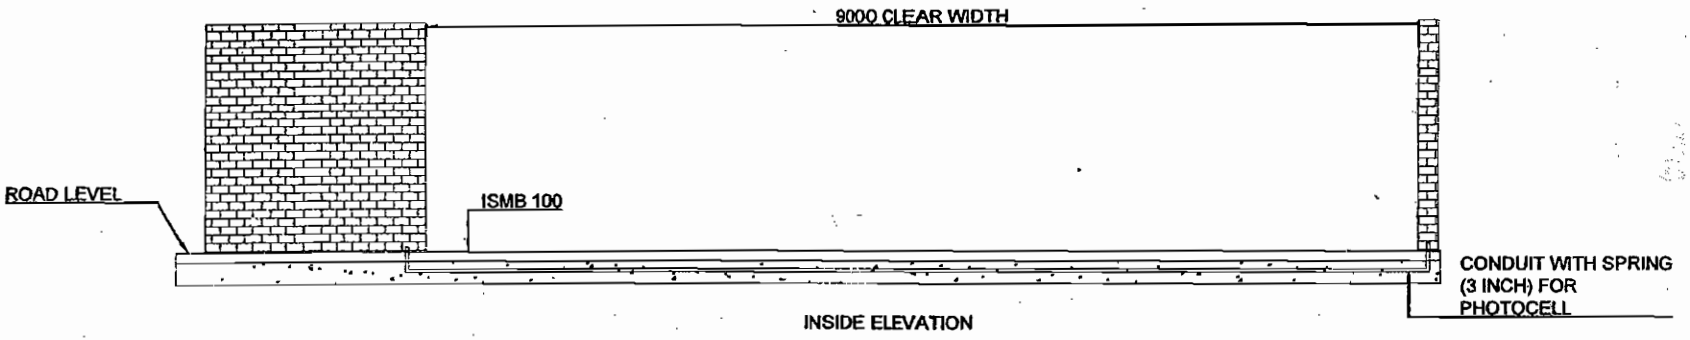

INSIDE ELEVATION

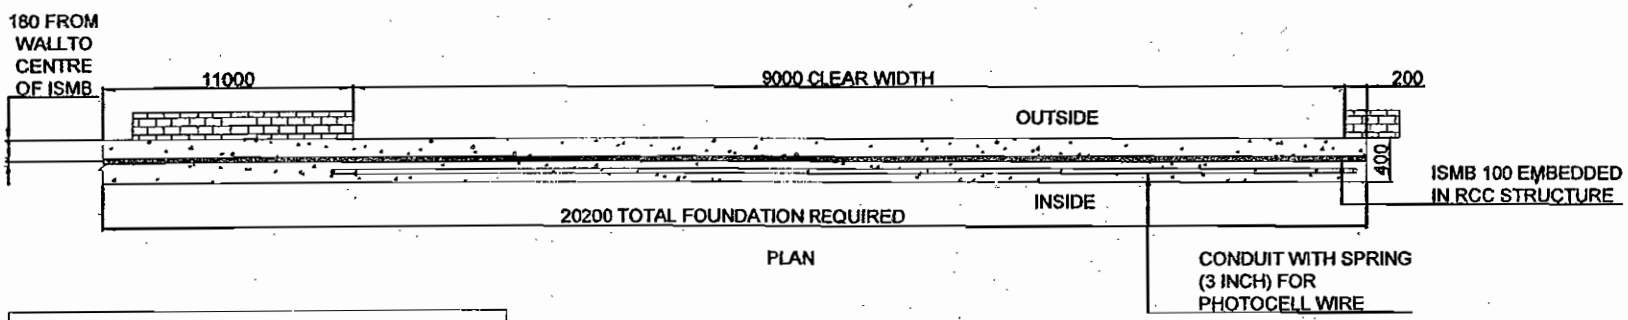

PLAN

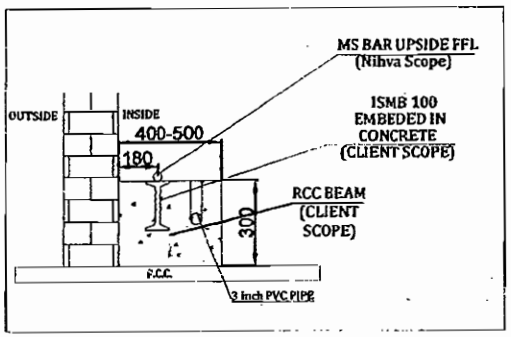


9.0m SLIDING GATE FOUNDATION

M.S bar top should be at finished road level

Thanks
Sagar Gohil.

This drawing & design is the property of NIHVA TECHNOLOGIES. Not to be sold or copied to any other concern.

TITLE	FOUNDATION FOR 9M SLIDING GATE		NIHVA TECHNOLOGIES PVT. LTD. PUNE
	SIGN	DATE	NIHVA TECHNOLOGIES PVT. LTD. Tel : 020 66304033 Email:- info@nihva.com Website:- www.nihva.com
DRAWN	OMKAR	31/08/17	CLIENT - SHILCHAR TECHNOLOGIES LTD.
CHECK	SHEKHAR	31/08/17	PROJECT -
REV.			SITE - VADODARA
APPROVAL	SHEKHAR	31/08/17	DWG. NO. : NIHVA/17-18/0189
If any queries contact : projects@nihva.com			SCALE: NTS | WT: | SHEET: 01 OF 01
ALL DIMENSION ARE IN mm			

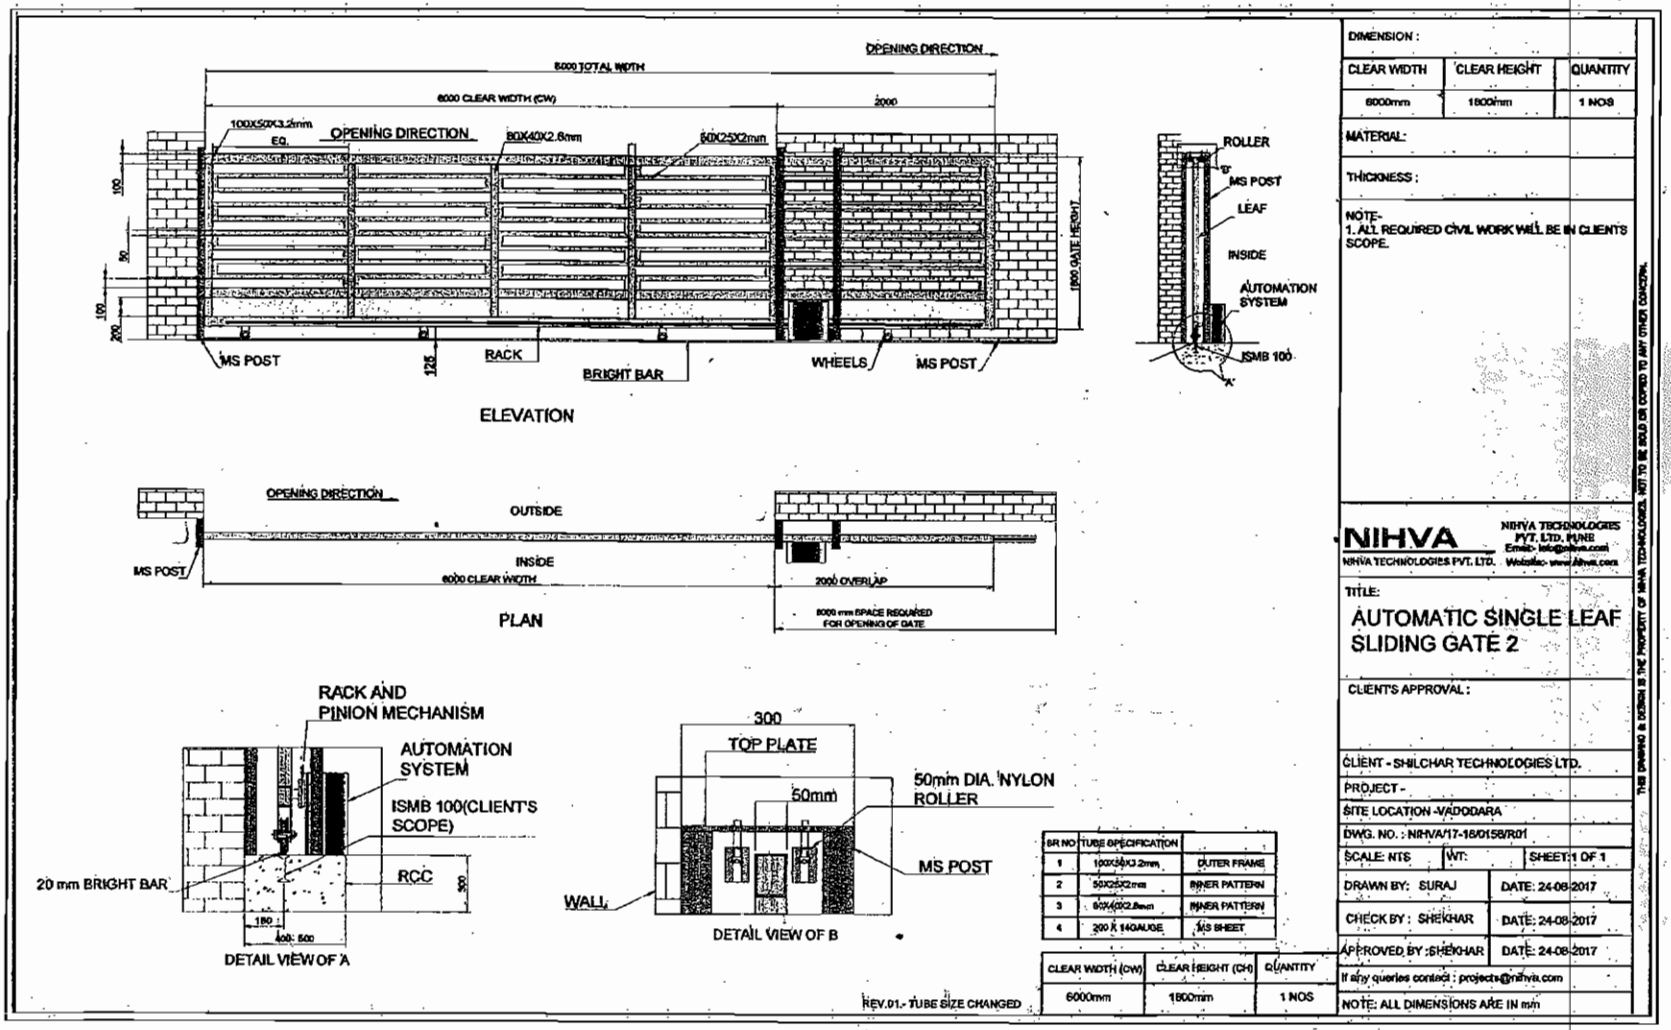

SR NO	TUBE SPECIFICATION	
1	100X50X3.2mm	OUTER FRAME
2	50X25X2mm	INNER PATTERN
3	60X40X2.6mm	INNER PATTERN
4	200 X 14GAUGE	MS SHEET

CLEAR WIDTH (CW)	CLEAR HEIGHT (CH)	QUANTITY
6000mm	1800mm	1 NOS

REV.01.- TUBE SIZE CHANGED

DIMENSION :

CLEAR WIDTH	CLEAR HEIGHT	QUANTITY
6000mm	1800mm	1 NOS

MATERIAL :

THICKNESS :

NOTE-
1. ALL REQUIRED CIVIL WORK WILL BE IN CLIENTS SCOPE.

NIHVA

NIHVA TECHNOLOGIES PVT. LTD. PUNE
Email:- info@nihva.com
Website:- www.nihva.com

NIHVA TECHNOLOGIES PVT. LTD.

TITLE:

AUTOMATIC SINGLE LEAF SLIDING GATE 2

CLIENT'S APPROVAL :

CLIENT - SHILCHAR TECHNOLOGIES LTD.

PROJECT -

SITE LOCATION -VADODARA

DWG. NO. : NIHVA/17-18/0158/R01

SCALE: NTS	WT:	SHEET:1 OF 1
DRAWN BY: SURAJ		DATE: 24-08-2017
CHECK BY : SHEKHAR		DATE: 24-08-2017
APPROVED BY :SHEKHAR		DATE: 24-08-2017

If any queries contact : projects@nihva.com

NOTE: ALL DIMENSIONS ARE IN m/m

THIS DRAWING & DESIGN IS THE PROPERTY OF NIHVA TECHNOLOGIES, NOT TO BE SOLD OR COPIED TO ANY OTHER CONCERN.


0.11

Tube section Steel be as Per drawing Submitted by U.S.


Sagar gokul

Color scheme - PS 5


Color grey.

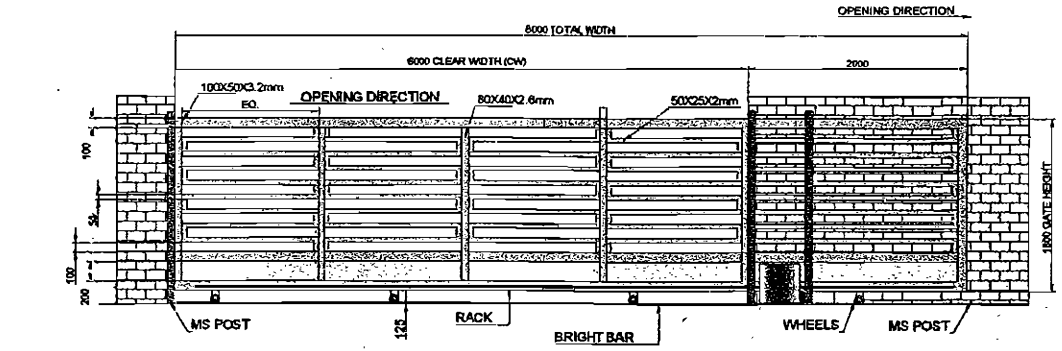


ELEVATION

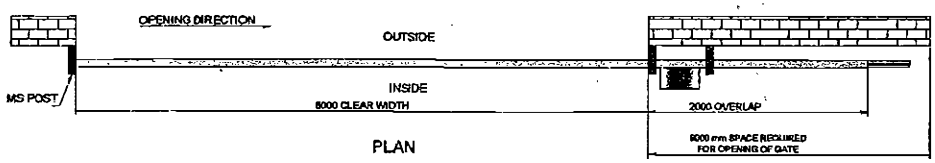

PLAN

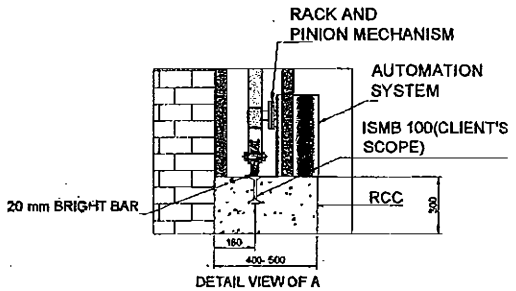

DETAIL VIEW OF A

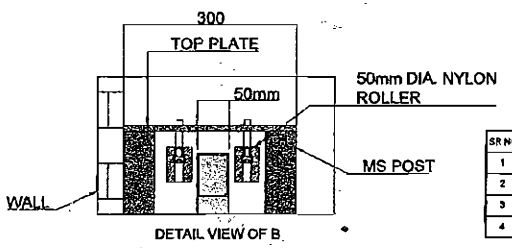

DETAIL VIEW OF B

SR NO	TUBE SPECIFICATION	
1	100X50X3.2mm	OUTER FRAME
2	50X25X2mm	INNER PATTERN
3	80X40X2.6mm	INNER PATTERN
4	200 X 14GAUGE	MS SHEET

CLEAR WIDTH (CW)	CLEAR HEIGHT (CH)	QUANTITY
6000mm	1800mm	1 NOS

REV.01 - TUBE SIZE CHANGED

DIMENSION :

CLEAR WIDTH	CLEAR HEIGHT	QUANTITY
6000mm	1800mm	1 NOS

MATERIAL:

THICKNESS :

NOTE-
1. ALL REQUIRED CIVIL WORK WILL BE IN CLIENTS SCOPE.

NIHVA TECHNOLOGIES PVT. LTD.

NIHVA TECHNOLOGIES PVT. LTD, PUNE
Email:- info@nihva.com
Website:- www.nihva.com

TITLE:

AUTOMATIC SINGLE LEAF SLIDING GATE 2

CLIENT'S APPROVAL :

CLIENT - SHILCHAR TECHNOLOGIES LTD.

PROJECT -

SITE LOCATION -VADODARA


DWG. NO. : NIHVA/17-18/0158/R01

SCALE: NTS	WT:	SHEET 1 OF 1
DRAWN BY: SURAJ		DATE: 24-08-2017
CHECK BY : SHEKHAR		DATE: 24-08-2017
APPROVED BY :SHEKHAR		DATE: 24-08-2017

If any queries contact : projects@nihva.com

NOTE: ALL DIMENSIONS ARE IN mm

THIS DRAWING & DESIGN IS THE PROPERTY OF NIHVA TECHNOLOGIES, NOT TO BE SOLD OR COPIED TO ANY OTHER CONCERN.

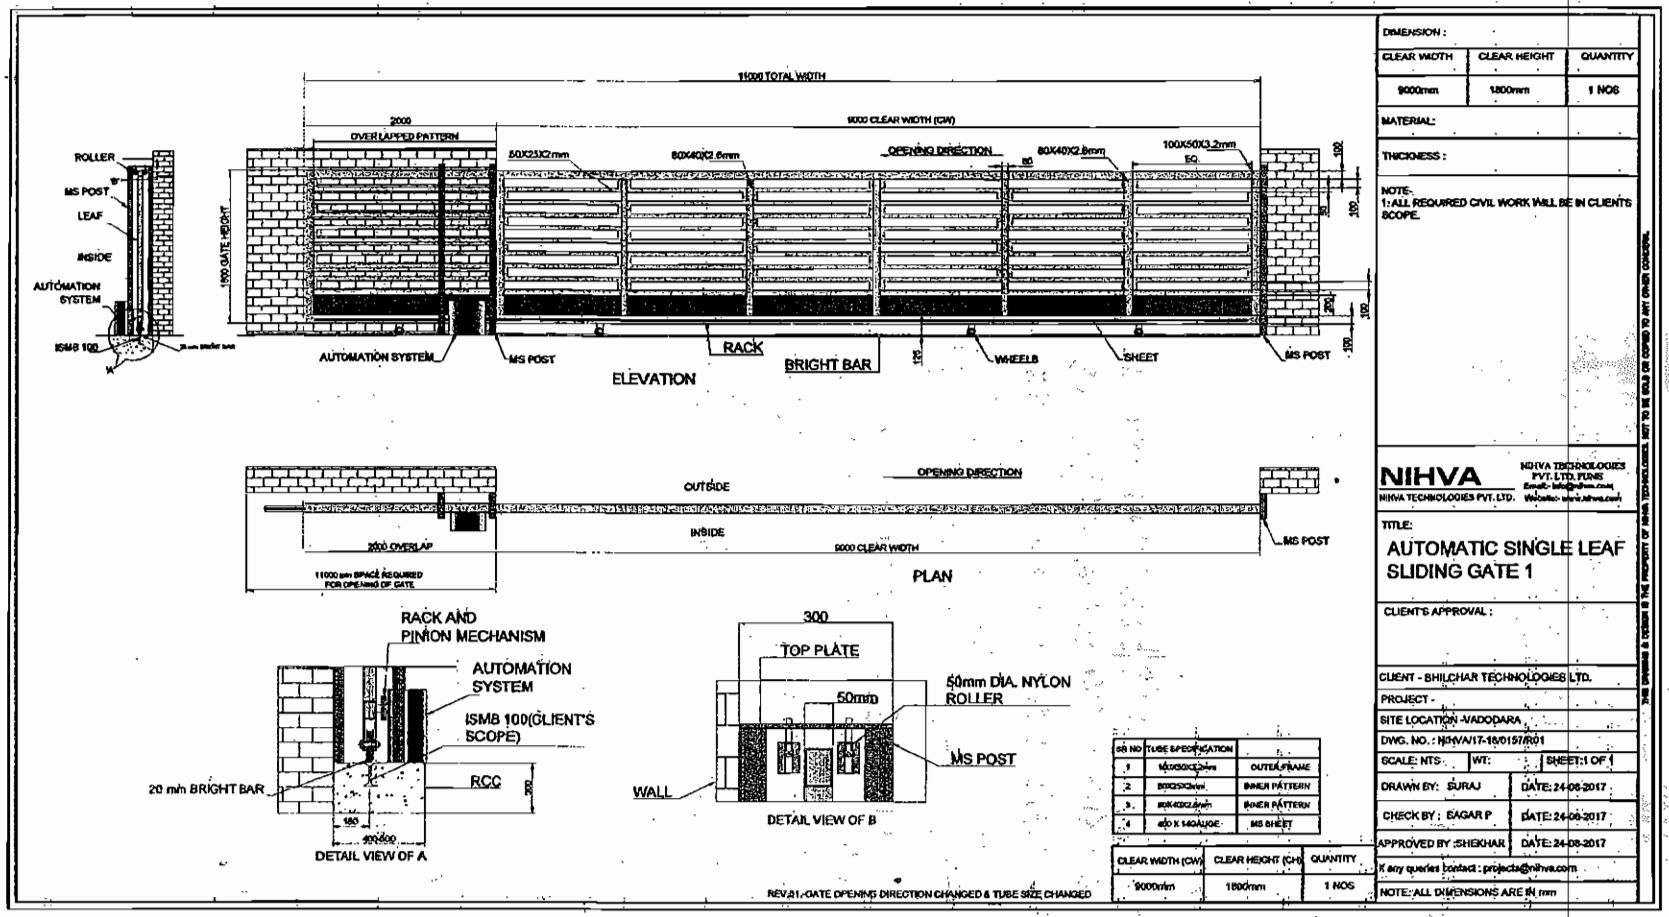

SR NO	TUBE SPECIFICATION	
1	100X50X2.0mm	OUTER FRAME
2	80X50X2mm	INNER PATTERN
3	80X40X2.6mm	INNER PATTERN
4	400 X 140ANGLE	MS SHEET

CLEAR WIDTH (CW)	CLEAR HEIGHT (CH)	QUANTITY
9000mm	1800mm	1 NOS

DIMENSION :

CLEAR WIDTH	CLEAR HEIGHT	QUANTITY
9000mm	1800mm	1 NOS

MATERIAL:

THICKNESS :

NOTE-
1: ALL REQUIRED CIVIL WORK WILL BE IN CLIENTS SCOPE.

NIHVA

NIHVA TECHNOLOGIES PVT. LTD.

NIHVA TECHNOLOGIES PVT. LTD. PUNE
Email:- info@nihva.com
Website:- www.nihva.com

TITLE:
AUTOMATIC SINGLE LEAF SLIDING GATE 1

CLIENT'S APPROVAL :

CLIENT - BHILCHAR TECHNOLOGIES LTD.
PROJECT -
SITE LOCATION -VADODARA
DWG. NO. : NIHVA/17-18/0157/R01
SCALE: NTS | WT: | SHEET:1 OF 1
DRAWN BY: SURAJ | DATE: 24-08-2017
CHECK BY : SAGAR P | DATE: 24-08-2017
APPROVED BY :SHEKHAR | DATE: 24-08-2017
If any queries contact : projects@nihva.com
NOTE: ALL DIMENSIONS ARE IN mm

THE DRAWING & DESIGN IS THE PROPERTY OF NIHVA TECHNOLOGIES, NOT TO BE SOLD OR COPIED TO ANY OTHER CONCERN.

O.K.

Tube section sheet be as Per drawing submitted by VJ

Sagar gohil

Color scheme - PS5


Color - grey

O.K.

Sugus gokul

Color- as per our PEB sheet sample.

Color scheme - PS5

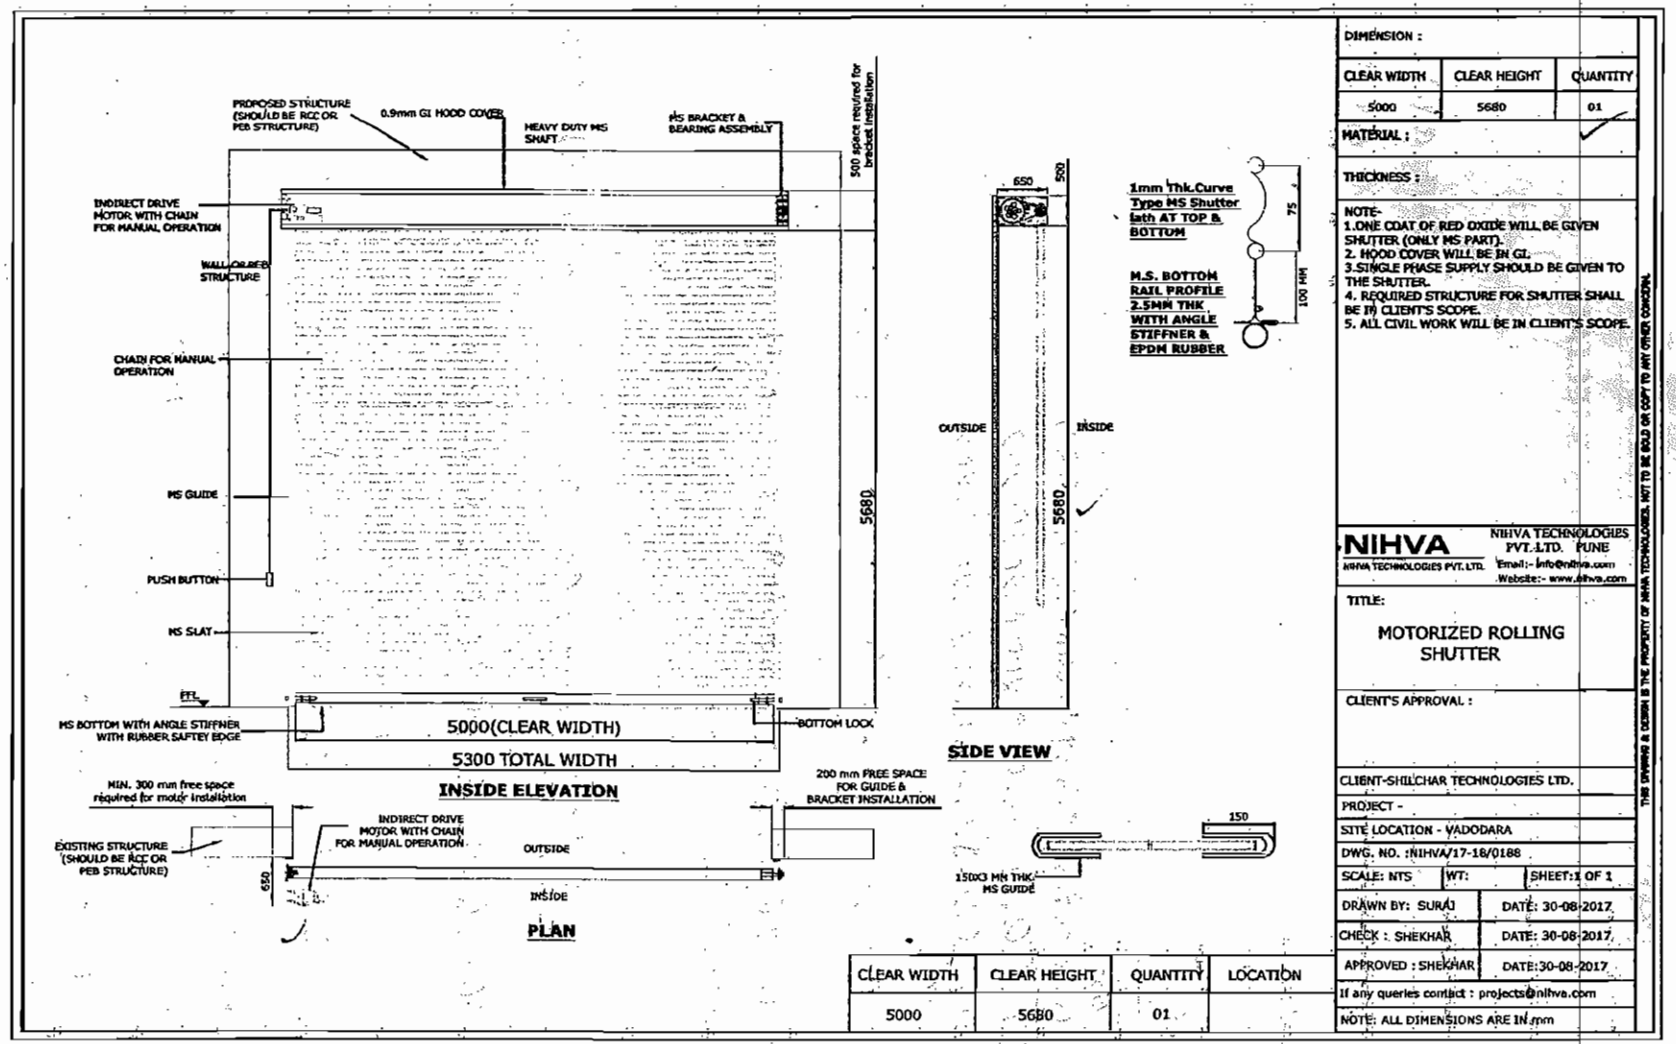

CLEAR WIDTH	CLEAR HEIGHT	QUANTITY	LOCATION
5000	5680	01	

DIMENSION :

CLEAR WIDTH	CLEAR HEIGHT	QUANTITY
5000	5680	01

MATERIAL :

THICKNESS :

NOTE-
1.ONE COAT OF RED OXIDE WILL BE GIVEN SHUTTER (ONLY MS PART).
2. HOOD COVER WILL BE IN GI.
3.SINGLE PHASE SUPPLY SHOULD BE GIVEN TO THE SHUTTER.
4. REQUIRED STRUCTURE FOR SHUTTER SHALL BE IN CLIENT'S SCOPE.
5. ALL CIVIL WORK WILL BE IN CLIENT'S SCOPE.

NIHVA
NIHVA TECHNOLOGIES PVT.LTD.

NIHVA TECHNOLOGIES PVT.LTD. PUNE
Email:- info@nihva.com
Website:- www.nihva.com

TITLE:
MOTORIZED ROLLING SHUTTER

CLIENT'S APPROVAL :

CLIENT-SHILCHAR TECHNOLOGIES LTD.

PROJECT -

SITE LOCATION - VADODARA

DWG. NO. :NIHVA/17-18/0188

SCALE: NTS | WT: | SHEET:1 OF 1

DRAWN BY: SURAJ | DATE: 30-08-2017

CHECK : SHEKHAR | DATE: 30-08-2017

APPROVED : SHEKHAR | DATE:30-08-2017

If any queries contact : projects@nihva.com

NOTE: ALL DIMENSIONS ARE IN mm

THE DRAWING & DESIGN IS THE PROPERTY OF NIHVA TECHNOLOGIES. NOT TO BE SOLD OR COPY TO ANY OTHER CONCERN.

Between Sheet : 1 & 6


O.K.

Sage grid

Color :- As per our PEB Sample.

Color scheme - PSS.

Note :- Guide shall be 50 mm wide.

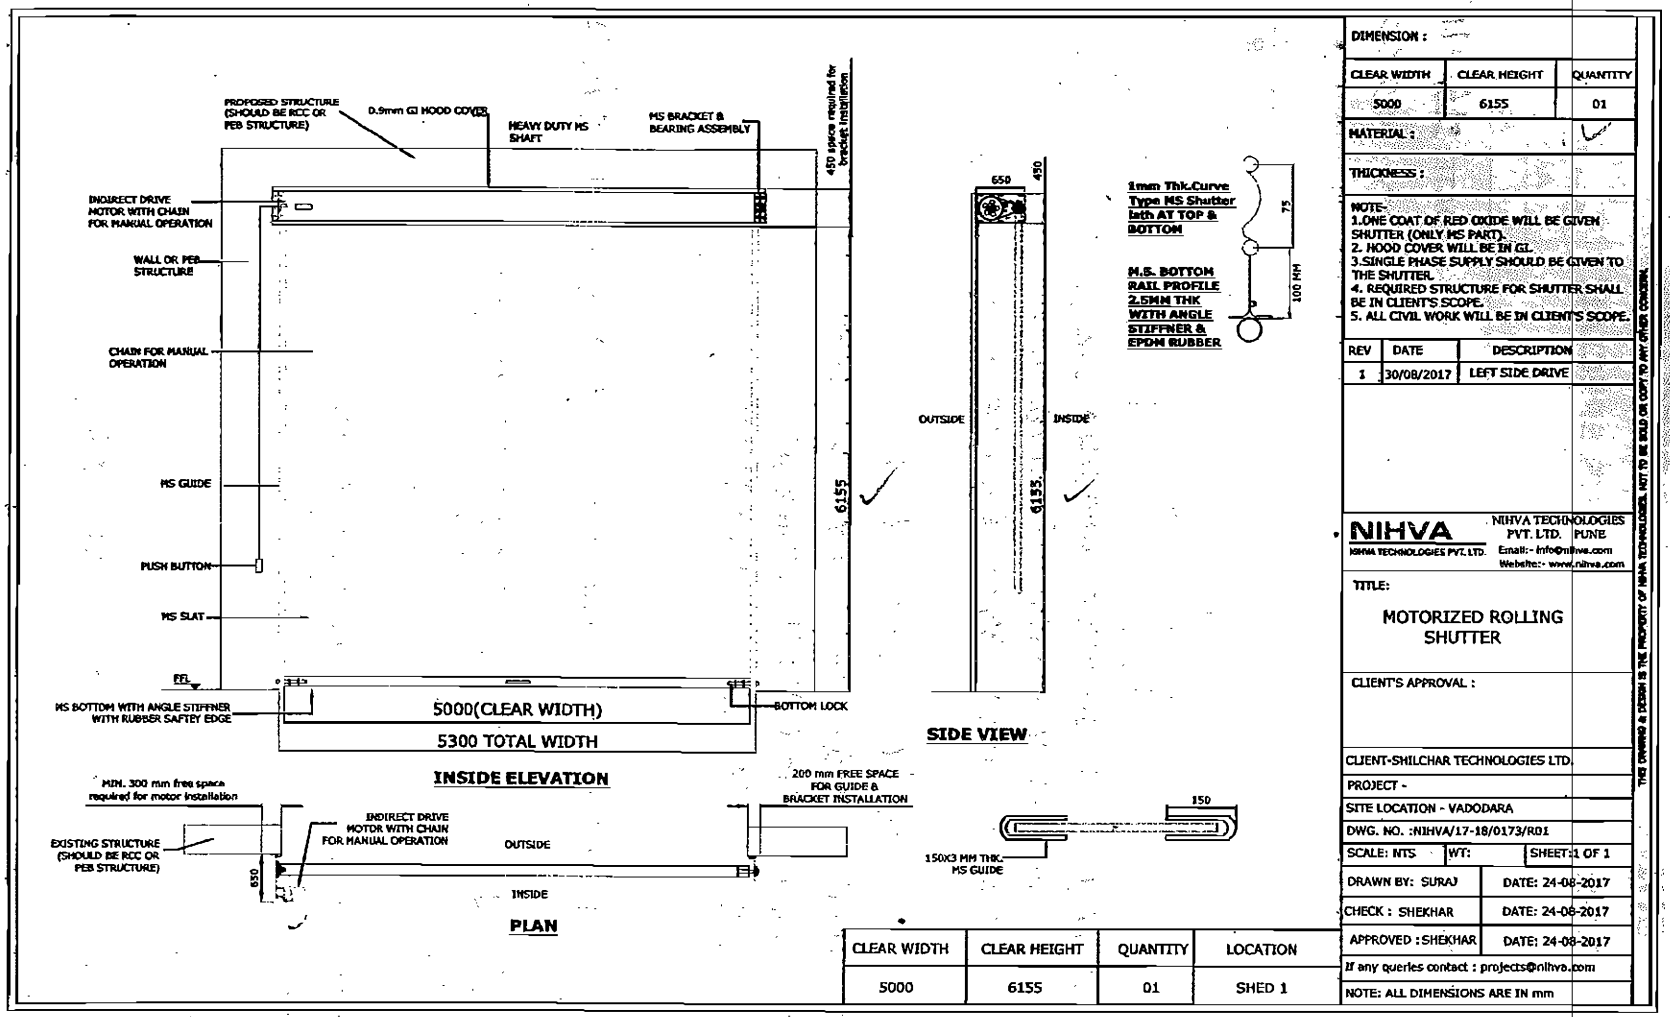

CLEAR WIDTH	CLEAR HEIGHT	QUANTITY	LOCATION
5000	6155	01	SHED 1

DIMENSION :

CLEAR WIDTH	CLEAR HEIGHT	QUANTITY
5000	6155	01

MATERIAL :

THICKNESS :

NOTE-
1.ONE COAT OF RED OXIDE WILL BE GIVEN SHUTTER (ONLY MS PART).
2. HOOD COVER WILL BE IN GI.
3.SINGLE PHASE SUPPLY SHOULD BE GIVEN TO THE SHUTTER.
4. REQUIRED STRUCTURE FOR SHUTTER SHALL BE IN CLIENT'S SCOPE.
5. ALL CIVIL WORK WILL BE IN CLIENT'S SCOPE.

REV	DATE	DESCRIPTION
1	30/08/2017	LEFT SIDE DRIVE

NIHVA
NIHVA TECHNOLOGIES PVT. LTD.
NIHVA TECHNOLOGIES PVT. LTD. PUNE
Email:- info@nihva.com
Website:- www.nihva.com

TITLE:
MOTORIZED ROLLING SHUTTER

CLIENT'S APPROVAL :

CLIENT-SHILCHAR TECHNOLOGIES LTD.
PROJECT -
SITE LOCATION - VADODARA
DWG. NO. :NIHVA/17-18/0173/R01
SCALE: NTS | WT: | SHEET:1 OF 1
DRAWN BY: SURAJ | DATE: 24-08-2017
CHECK : SHEKHAR | DATE: 24-08-2017
APPROVED :SHEKHAR | DATE: 24-08-2017
If any queries contact : projects@nihva.com
NOTE: ALL DIMENSIONS ARE IN mm

THIS DRAWING & DESIGN IS THE PROPERTY OF NIHVA TECHNOLOGIES, NOT TO BE SOLD OR COPY TO ANY OTHER CONCERN.

Shed # 1.

OIC


Sagar Gohil

Color scheme - PSS

Color - As per color PEB sample

Note: guide shall be 50 mm extra.

Drive location to be change

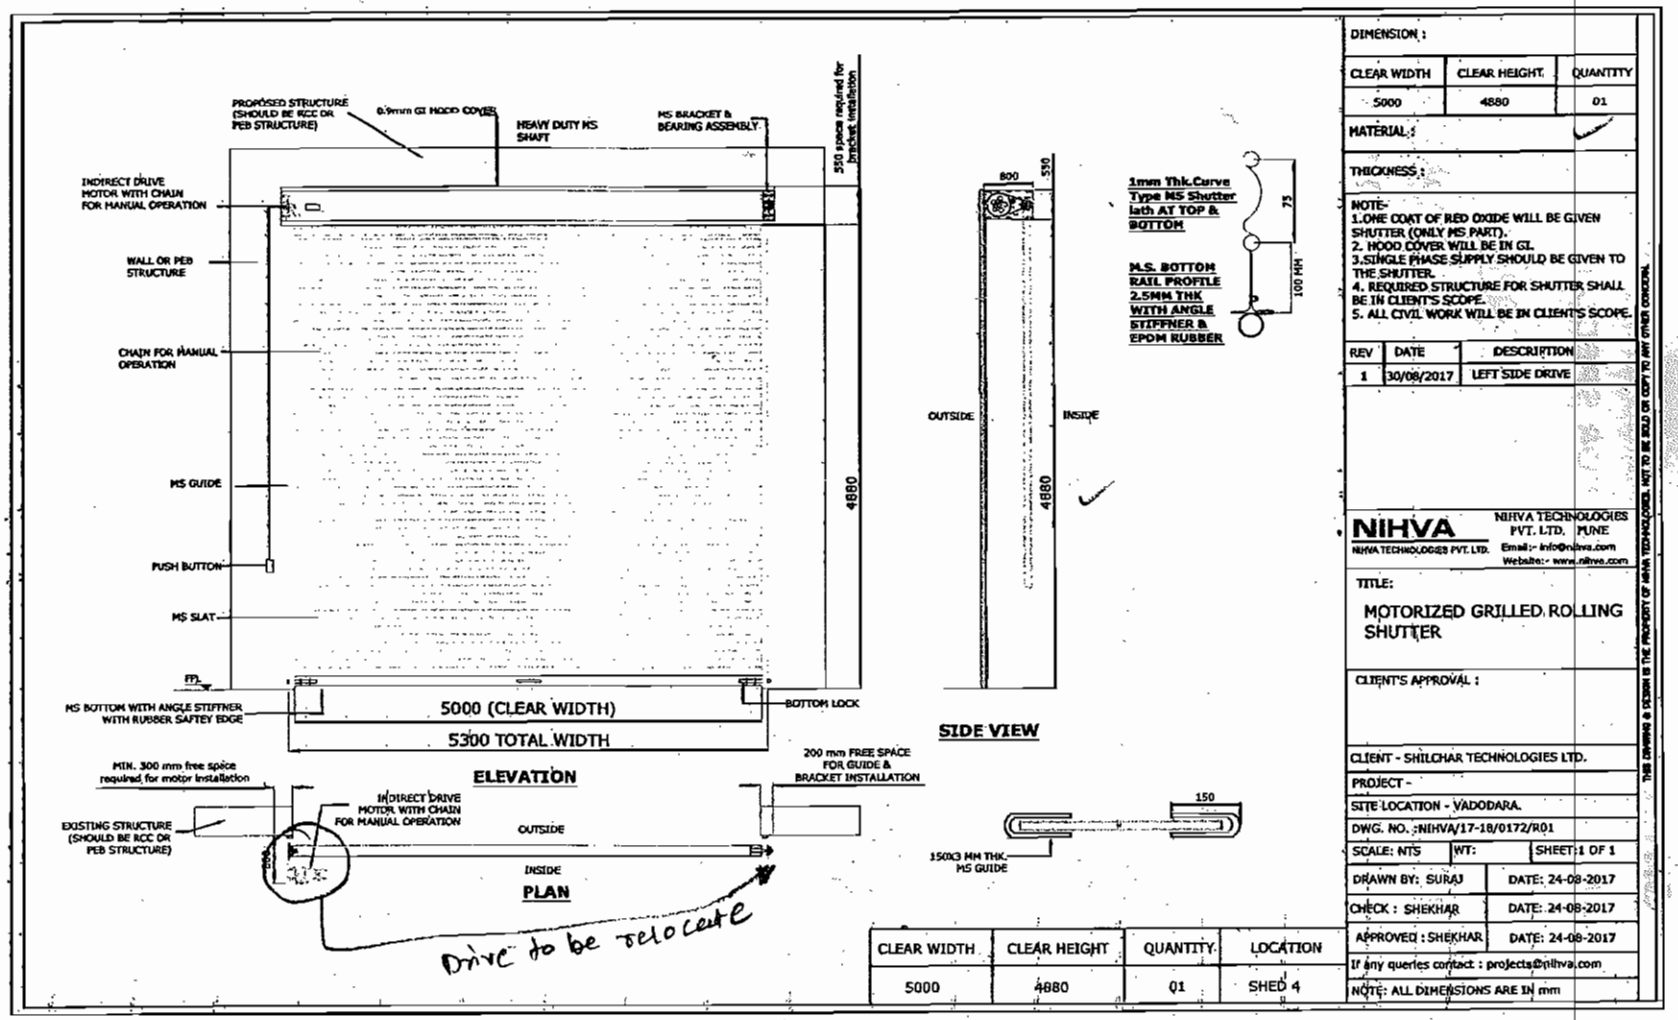

CLEAR WIDTH	CLEAR HEIGHT	QUANTITY	LOCATION
5000	4880	01	SHED 4

DIMENSION :

CLEAR WIDTH	CLEAR HEIGHT	QUANTITY
5000	4880	01

MATERIAL :

THICKNESS :

NOTE-
1.ONE COAT OF RED OXIDE WILL BE GIVEN SHUTTER (ONLY MS PART).
2. HOOD COVER WILL BE IN GI.
3.SINGLE PHASE SUPPLY SHOULD BE GIVEN TO THE SHUTTER.
4. REQUIRED STRUCTURE FOR SHUTTER SHALL BE IN CLIENT'S SCOPE.
5. ALL CIVIL WORK WILL BE IN CLIENT'S SCOPE.

REV	DATE	DESCRIPTION
1	30/08/2017	LEFT SIDE DRIVE

NIHVA
NIHVA TECHNOLOGIES PVT. LTD.
NIHVA TECHNOLOGIES PVT. LTD, PUNE
Email:- info@nihva.com
Website:- www.nihva.com

TITLE:
MOTORIZED GRILLED ROLLING SHUTTER

CLIENT'S APPROVAL :

CLIENT - SHILCHAR TECHNOLOGIES LTD.
PROJECT -
SITE LOCATION - VADODARA.
DWG. NO. :NIHVA/17-18/0172/R01

SCALE: NTS	WT:	SHEET:1 OF 1
DRAWN BY: SURAJ		DATE: 24-08-2017
CHECK : SHEKHAR		DATE: 24-08-2017
APPROVED : SHEKHAR		DATE: 24-08-2017

If any queries contact : projects@nihva.com
NOTE: ALL DIMENSIONS ARE IN mm

THIS DRAWING & DESIGN IS THE PROPERTY OF NIHVA TECHNOLOGIES. NOT TO BE SOLD OR COPY TO ANY OTHER CONCERN.


Shed # 4

OK

Sugar gated

Color Scheme: PS5

Color Shade: As per our PEB Sample.

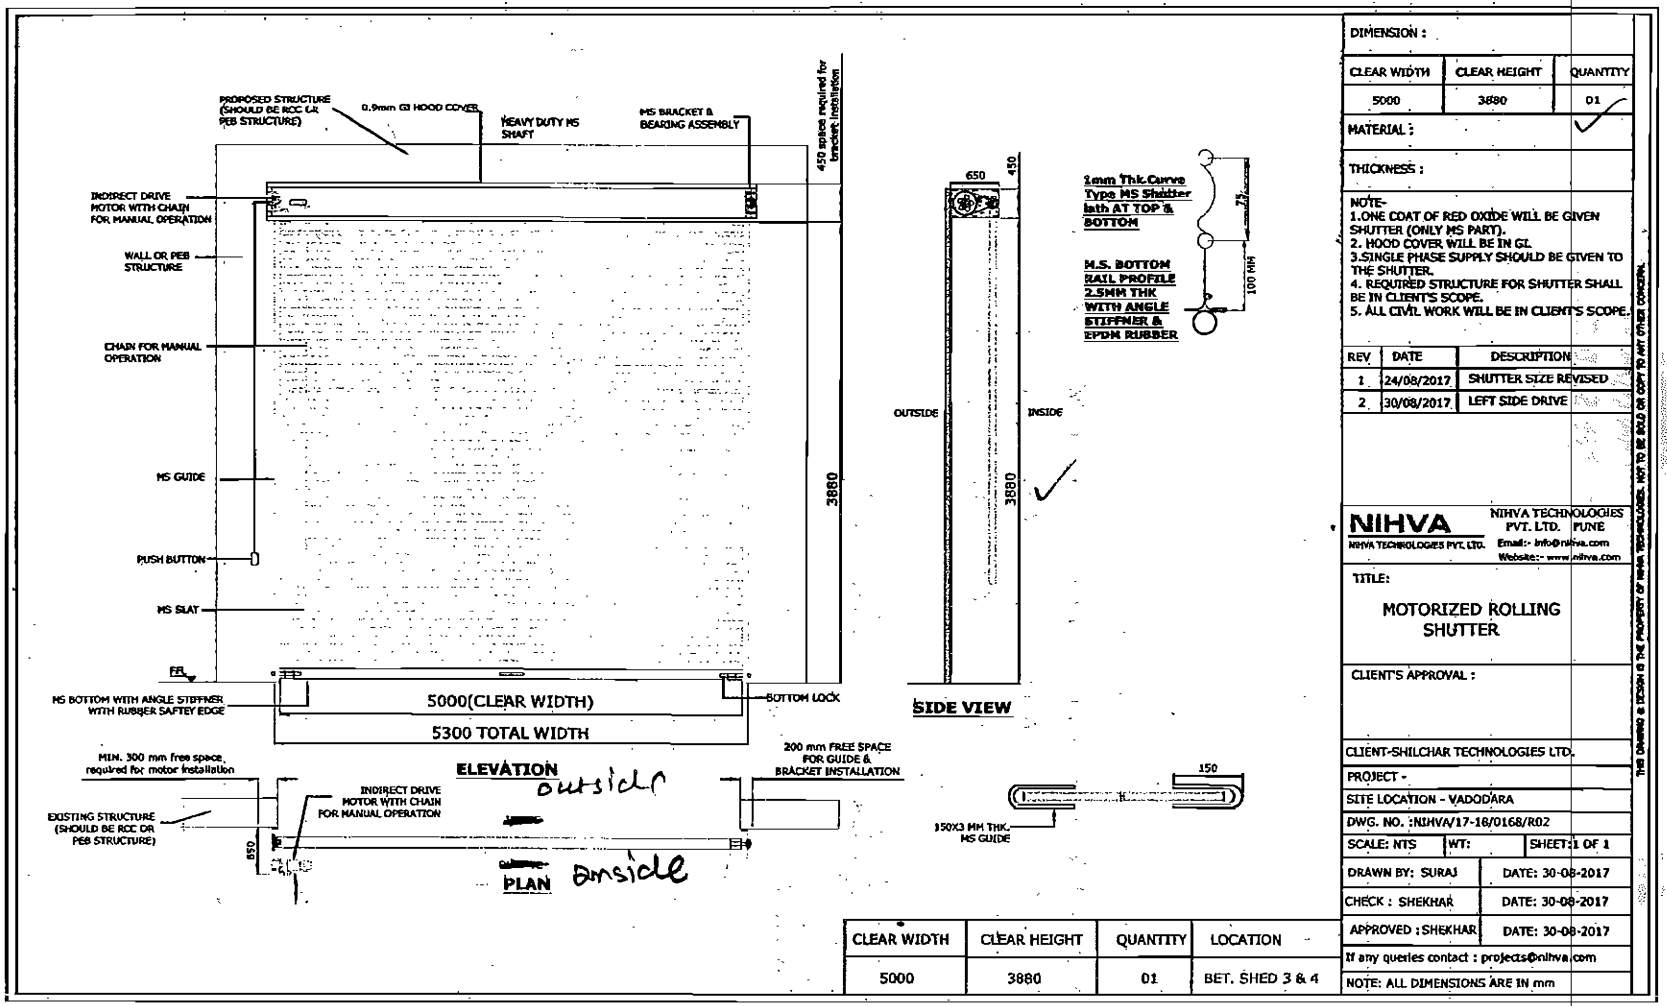

CLEAR WIDTH	CLEAR HEIGHT	QUANTITY	LOCATION
5000	3880	01	BET. SHED 3 & 4

DIMENSION :

CLEAR WIDTH	CLEAR HEIGHT	QUANTITY
5000	3880	01

MATERIAL :

THICKNESS :

NOTE-
1.ONE COAT OF RED OXIDE WILL BE GIVEN SHUTTER (ONLY MS PART).
2. HOOD COVER WILL BE IN GI.
3.SINGLE PHASE SUPPLY SHOULD BE GIVEN TO THE SHUTTER.
4. REQUIRED STRUCTURE FOR SHUTTER SHALL BE IN CLIENT'S SCOPE.
5. ALL CIVIL WORK WILL BE IN CLIENT'S SCOPE.

REV	DATE	DESCRIPTION
1	24/08/2017	SHUTTER SIZE REVISED
2	30/08/2017	LEFT SIDE DRIVE

NIHVA
NIHVA TECHNOLOGIES PVT. LTD.
NIHVA TECHNOLOGIES PVT. LTD. PUNE
Email:- info@nihva.com
Website:- www.nihva.com

TITLE:

MOTORIZED ROLLING SHUTTER

CLIENT'S APPROVAL :

CLIENT-SHILCHAR TECHNOLOGIES LTD.

PROJECT -

SITE LOCATION - VADODARA

DWG. NO. :NIHVA/17-18/0168/R02

SCALE: NTS	WT:	SHEET:1 OF 1
DRAWN BY: SURAJ		DATE: 30-08-2017
CHECK : SHEKHAR		DATE: 30-08-2017
APPROVED : SHEKHAR		DATE: 30-08-2017

If any queries contact : projects@nihva.com

NOTE: ALL DIMENSIONS ARE IN mm

THIS DRAWING & DESIGN IS THE PROPERTY OF NIHVA TECHNOLOGIES. NOT TO BE SOLD OR COPY TO ANY OTHER CONCERN.

Between Shed # 3 & 4

OK


Seen

Sagar Gohil.

Color scheme - PPS

Color Sheet : As Per

our PPS Sample.

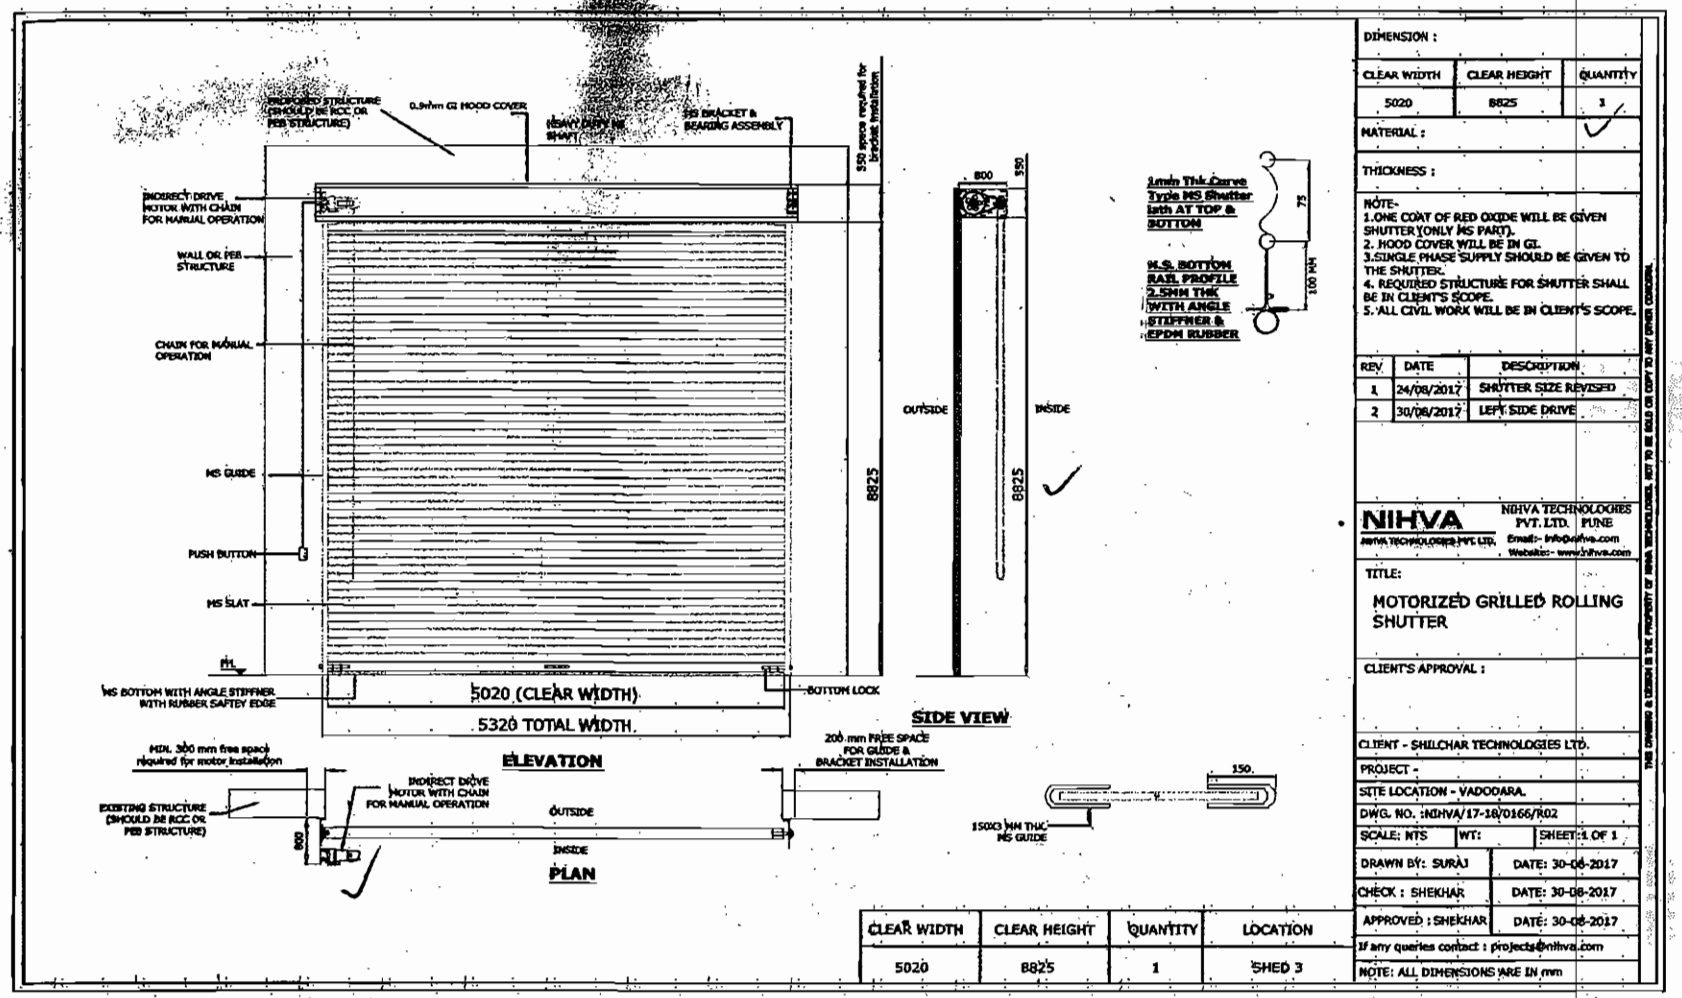

CLEAR WIDTH	CLEAR HEIGHT	QUANTITY	LOCATION
5020	8825	1	SHED 3

DIMENSION :

CLEAR WIDTH	CLEAR HEIGHT	QUANTITY
5020	8825	1

MATERIAL :

THICKNESS :

NOTE-
1.ONE COAT OF RED OXIDE WILL BE GIVEN SHUTTER (ONLY MS PART).
2. HOOD COVER WILL BE IN GI.
3.SINGLE PHASE SUPPLY SHOULD BE GIVEN TO THE SHUTTER.
4. REQUIRED STRUCTURE FOR SHUTTER SHALL BE IN CLIENT'S SCOPE.
5. ALL CIVIL WORK WILL BE IN CLIENT'S SCOPE.

REV.	DATE	DESCRIPTION
1	24/08/2017	SHUTTER SIZE REVISED
2	30/08/2017	LEFT SIDE DRIVE

NIHVA TECHNOLOGIES PVT. LTD. PUNE
NIHVA TECHNOLOGIES PVT. LTD. Email:- info@nihva.com Website:- www.nihva.com

TITLE:
MOTORIZED GRILLED ROLLING SHUTTER

CLIENT'S APPROVAL :

CLIENT - SHILCHAR TECHNOLOGIES LTD.
PROJECT -
SITE LOCATION - VADODARA.
DWG. NO. :NIHVA/17-18/0166/R02

SCALE: NTS	WT:	SHEET: 1 OF 1
DRAWN BY: SURAJ		DATE: 30-08-2017
CHECK : SHEKHAR		DATE: 30-08-2017
APPROVED : SHEKHAR		DATE: 30-08-2017

If any queries contact : projects@nihva.com
NOTE: ALL DIMENSIONS ARE IN mm

THIS DRAWING & DESIGN IS THE PROPERTY OF NIHVA TECHNOLOGIES, NOT TO BE SOLD OR COPY TO ANY OTHER CONCERN.

Shed #3


OIC

Sugges Approved.

Color Scheme - PES

Color Shade - As Per ours PEB Sample.

Note: guide shall be 50 mm wide (center).

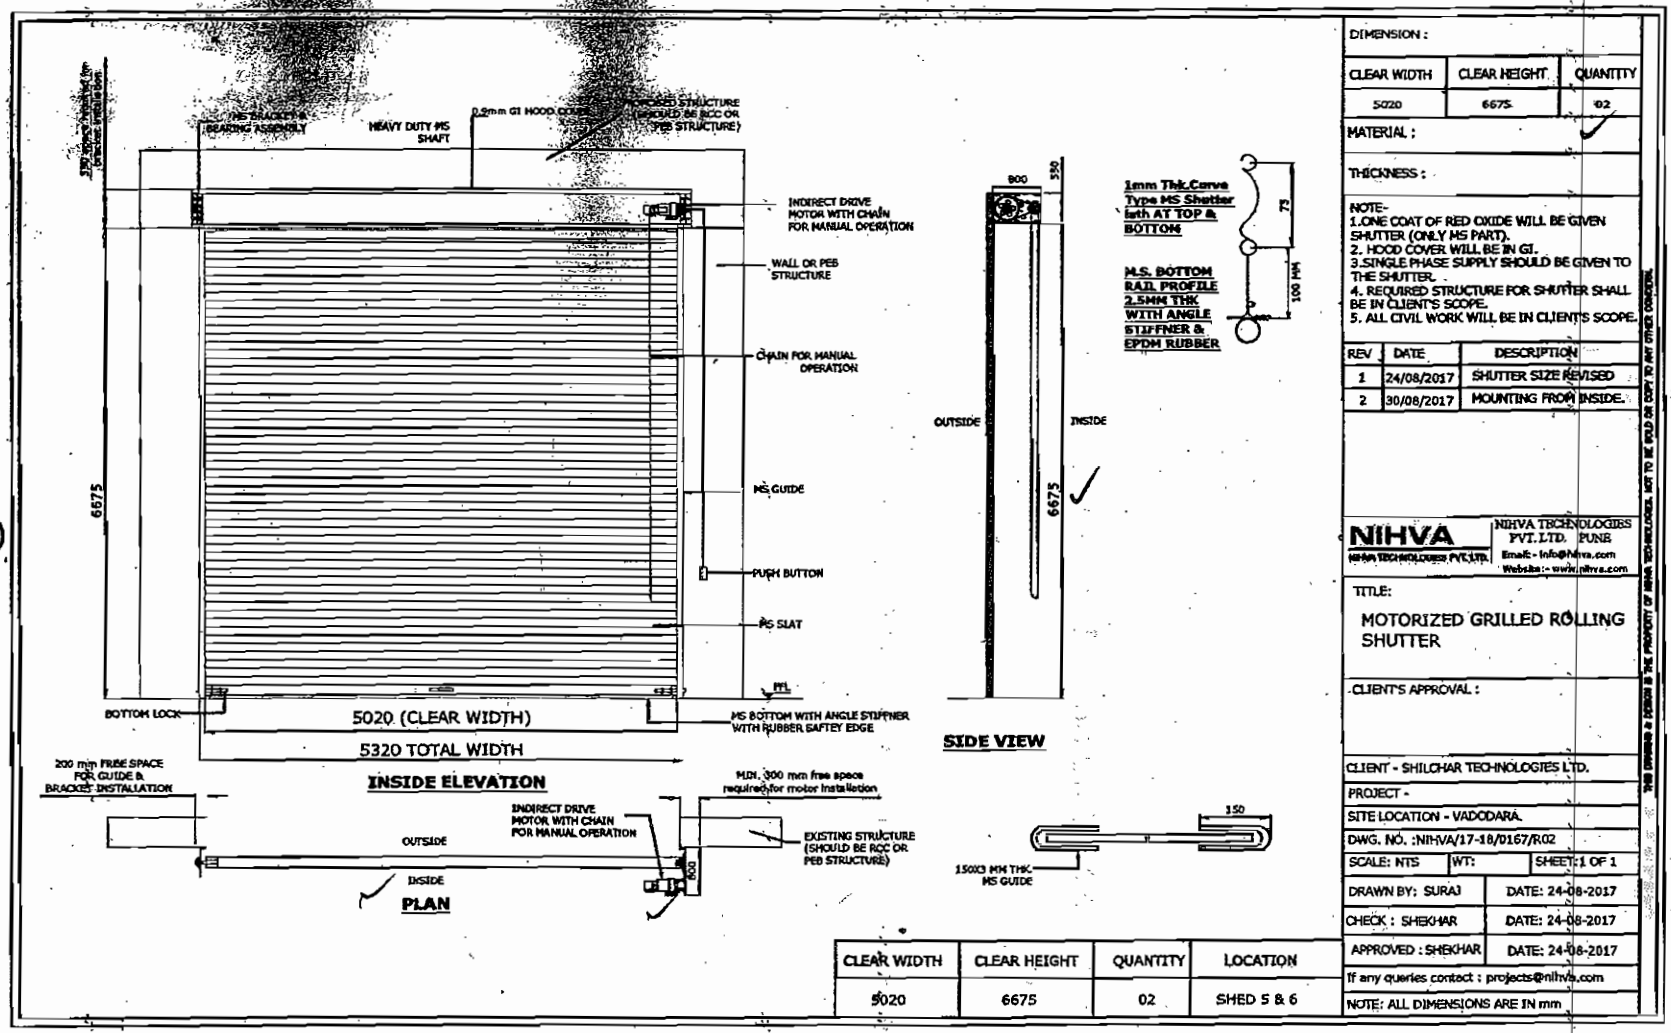

DIMENSION :

CLEAR WIDTH	CLEAR HEIGHT	QUANTITY
5020	6675	02

MATERIAL :

THICKNESS :

NOTE-
1.ONE COAT OF RED OXIDE WILL BE GIVEN SHUTTER (ONLY MS PART).
2. HOOD COVER WILL BE IN GI.
3.SINGLE PHASE SUPPLY SHOULD BE GIVEN TO THE SHUTTER.
4. REQUIRED STRUCTURE FOR SHUTTER SHALL BE IN CLIENT'S SCOPE.
5. ALL CIVIL WORK WILL BE IN CLIENT'S SCOPE.

REV	DATE	DESCRIPTION
1	24/08/2017	SHUTTER SIZE REVISED
2	30/08/2017	MOUNTING FROM INSIDE.

NIHVA TECHNOLOGIES PVT.LTD.
NIHVA TECHNOLOGIES PVT.LTD. PUNE
Email:- info@Nihva.com
Website:- www.nihva.com

TITLE:
MOTORIZED GRILLED ROLLING SHUTTER

CLIENT'S APPROVAL :

CLIENT - SHILCHAR TECHNOLOGIES LTD.
PROJECT -
SITE LOCATION - VADODARA.
DWG. NO. :NIHVA/17-18/0167/R02
SCALE: NTS | WT: | SHEET: 1 OF 1
DRAWN BY: SURAJ | DATE: 24-08-2017
CHECK : SHEKHAR | DATE: 24-08-2017
APPROVED : SHEKHAR | DATE: 24-08-2017
If any queries contact : projects@nihva.com
NOTE: ALL DIMENSIONS ARE IN mm

THIS DRAWING & DESIGN IS THE PROPERTY OF NIHVA TECHNOLOGIES, NOT TO BE SOLD OR COPY TO ANY OTHER CONCERN.

CLEAR WIDTH	CLEAR HEIGHT	QUANTITY	LOCATION
5020	6675	02	SHED 5 & 6

Shed # 5
Shed # 6.