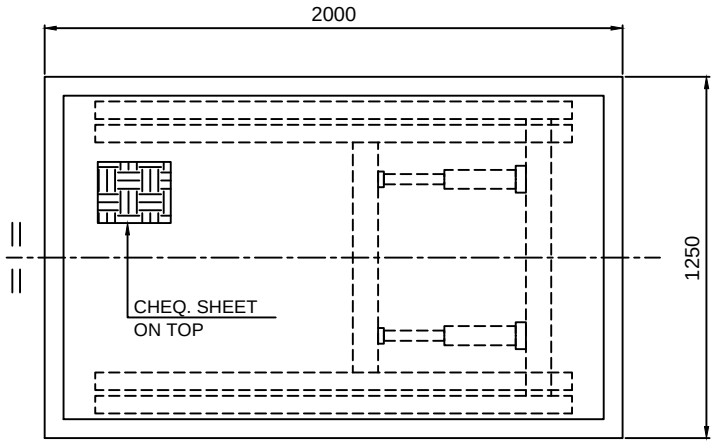

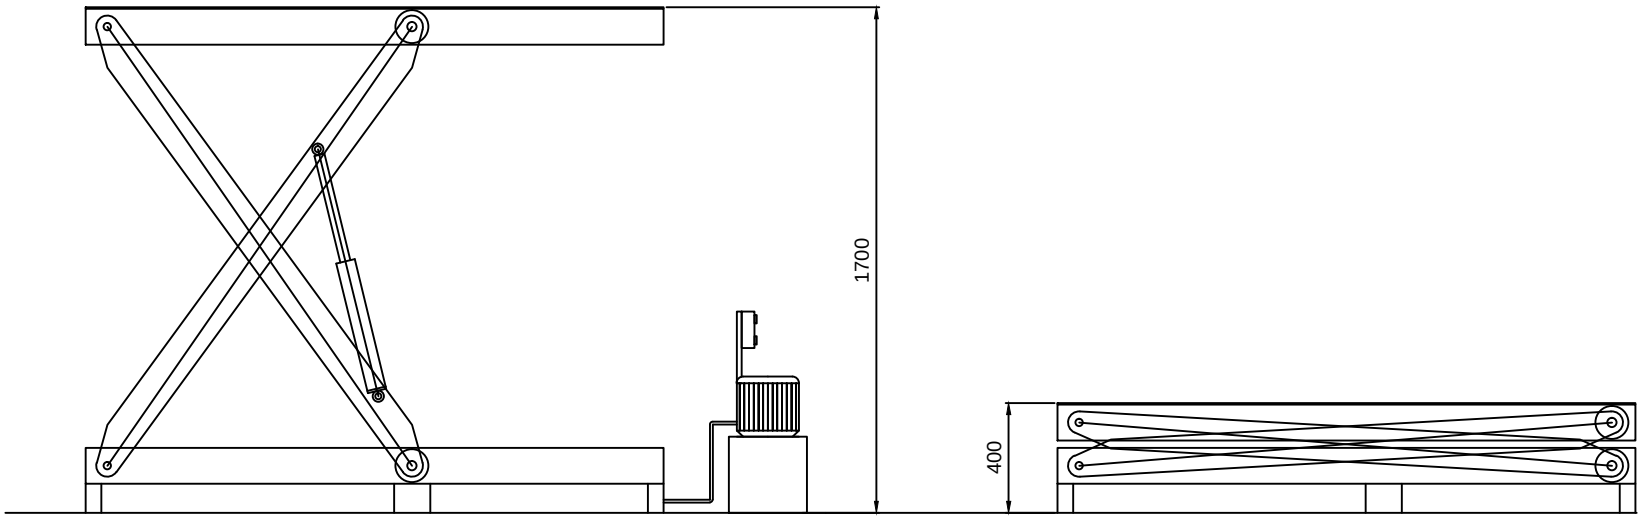

POWER PACK	3 HP, 3 PH
LIFT HT	1300 MM
MAX HT	1700 MM
SHUT HT	400 MM
PLATFORM SIZE	2000L x 1250W
CAPACITY	2 TON

NOTE :
1. COLOR : GOLDEN YELLOW
RAL : 1004.
2. OPERATION : INCHING MODE.

This drawing & design is the property of NIHVA TECHNOLOGIES. Not to be sold or copied to any other concern.

TITLE
FLOOR MOUNTED
SCISSOR LIFT GA DRAWING

	NAME	SIGN	DATE
DRAWN	P.V.A		29.05.2019
CHECK	V.M.T		29.05.2019
APPRD.			

If any queries contact : design@nihva.com

ALL DIMENSION ARE IN mm

NIHVA
NIHVA TECHNOLOGIES PVT. LTD.

NIHVA TECHNOLOGIES
PVT. LTD. PUNE
Tel : 020 66304033
Email:- info@nihva.com
Website:- www.nihva.com

CLIENT - KERKOLL
PROJECT -
SITE LOCATION - VADODARA
DWG. NO. : NIHVA/19-20/0025 | REV- 0
SCALE: NTS | WT: | SHEET: 01 OF 01