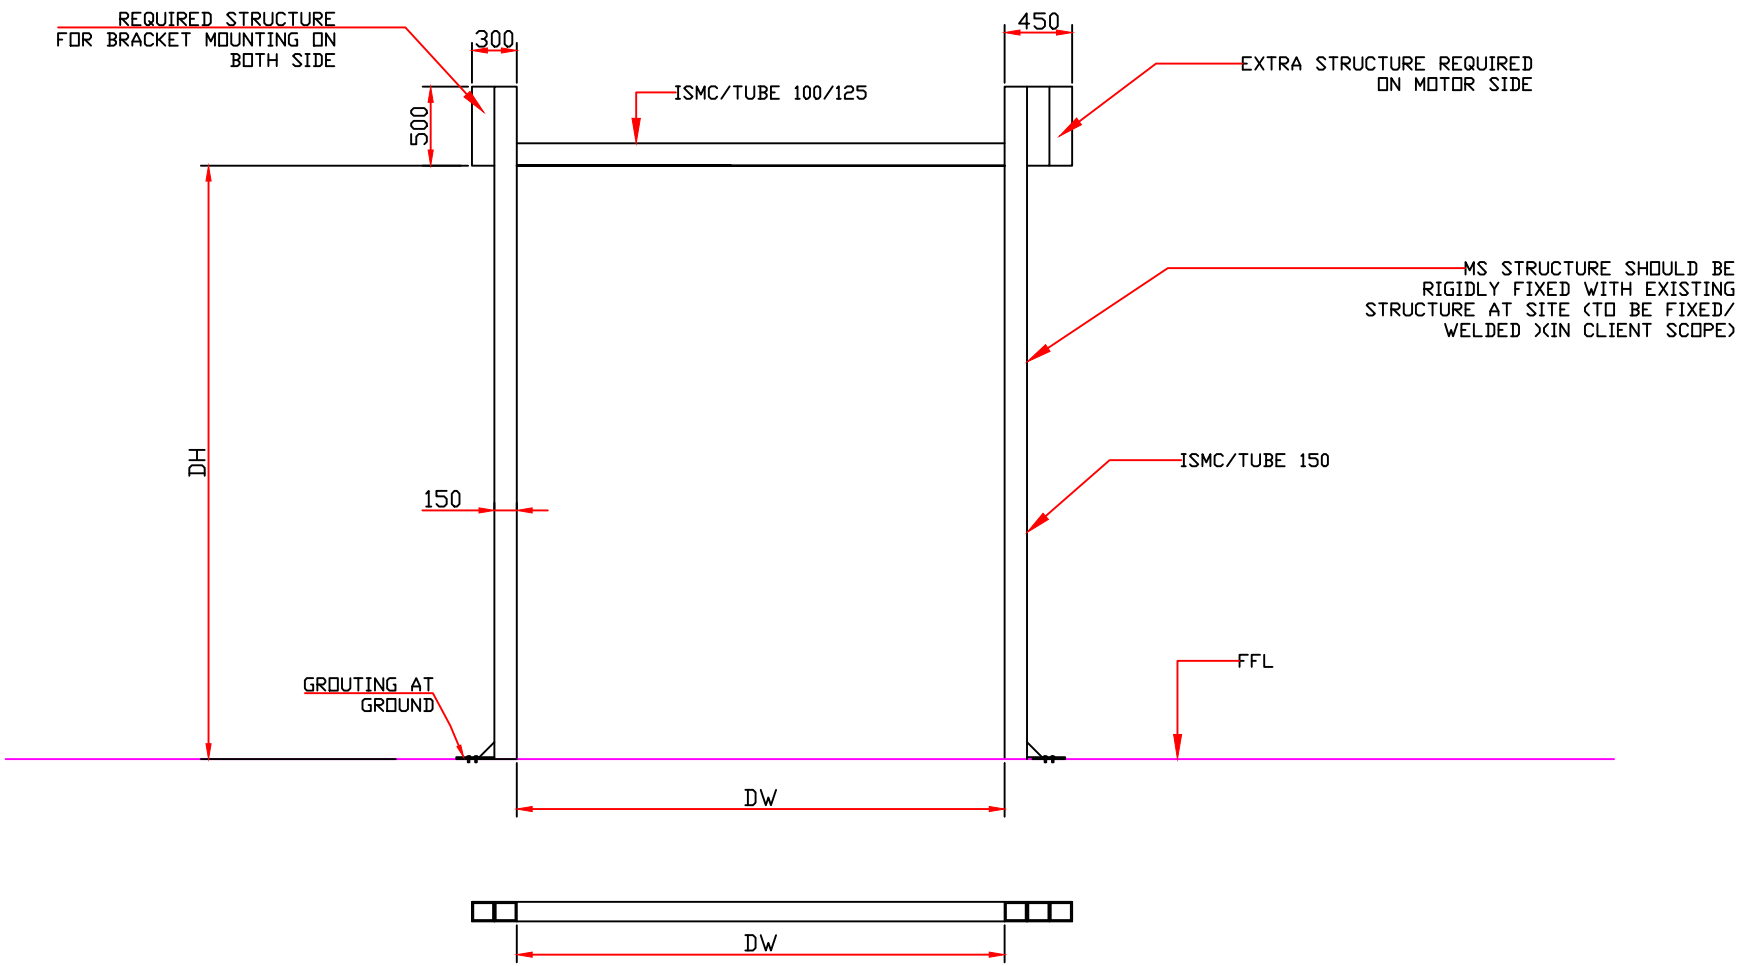


NOTE-
(1) MS STRUCTURE , FITTING & ALL CIVIL WORK IN CLIENT SCOPE.
(2) HIGH SPEED DOOR WILL BE ONLY INSTALLED AFTER READINESS OF STRUCTURE AS PER DRAWING PROVIDED.
(3) MS STRUCTURE SHOULD BE RIGID & FIXED TO THE STRUCTURE AT SITE (IN CLIENT SCOPE) .

SR NO	DW	DH	QUANTITY
1	2500	2500	1
2	3000	3000	1

Tolerance ±3 mm (for all dimensions)
Dimensions in [ ] ==> clearance for installation

This drawing & design is the property of NIHVA TECHNOLOGIES. Not to be sold or copied to any other concern.

TITLE - RR300 PLUS ALU HSD STRUCTURE

NIHVA TECHNOLOGIES PVT. LTD.
NIHVA TECHNOLOGIES PVT. LTD. PUNE
Tel : 020 66304033
Email:- info@nihva.com
Website:- www.nihva.com

	NAME	SIGN	DATE
DRAWN	S.M.S.		12.12.20
CHECK	S.B.		12.12.20
APPROVED			

CLIENT - TRANS ENGG. PVT LTD
PROJECT - TRANS ENGG. PVT LTD
LOCATION - BANER , PUNE
If any queries contact:sales@nihva.com
DWG. NO. -NIHVA/20-21/0110
REV- R00
ALL DIMENSION ARE IN mm
SCALE:NTS
WT:
SHEET: