
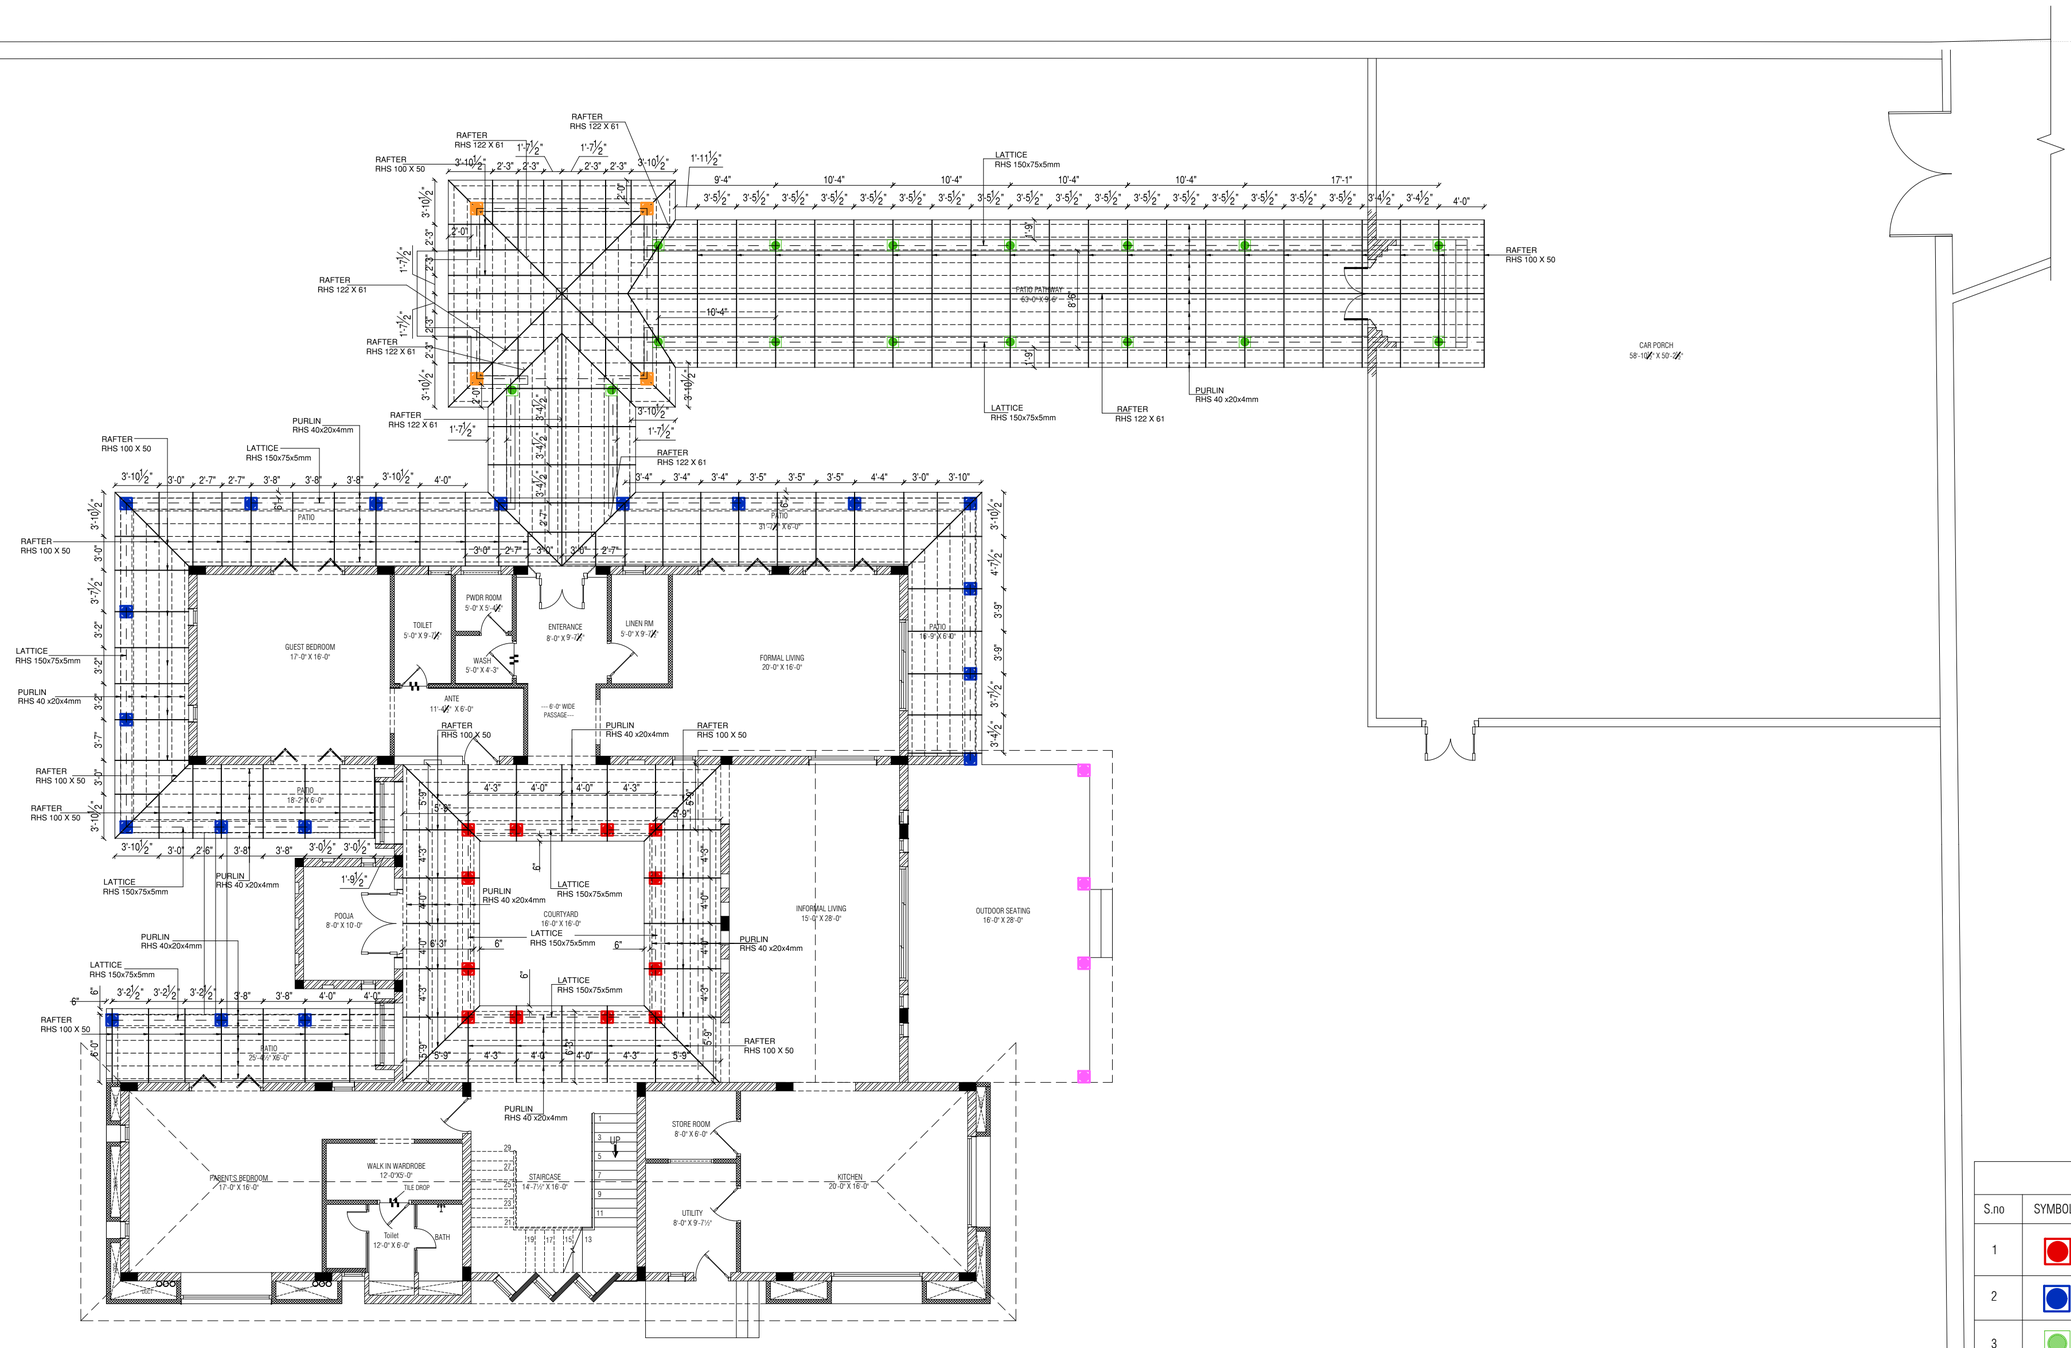


GROUND FLOOR - PATIO ROOFING LAYOUT

LEGENDS				
S.no	SYMBOLS	COULMNS IN	HT FROM LEVEL	NUMBERS
1		COURTYARD	6'-0" HT FROM +5'-0" LEVEL	12 NOS
2		PATIO	6'-8" HT FROM +4'-8" LEVEL	19 NOS
3		PATIO PATHWAY	8'-0" HT FROM +3'-6" LEVEL	16 NOS
4		PATIO - KRISHNA STATUE	5'-0" HT FROM WALL	4 NOS
5		OUTDOOR SEATING	9'-0" HT FROM +4'-8" LEVEL	4 NOS

COPYRIGHT :
THIS DRAWING IS A COPYRIGHT. IT IS NOT TO BE REPRODUCED, COPIED, HANDED OVER TO A THIRD PARTY OR USED FOR ANY OTHER PURPOSE OTHER THAN FOR THE PROJECT INVOLVED WITHOUT THE KNOWLEDGE OF THE ARCHITECT.

NOTES:
ALL DIMENSIONS TO BE CHECKED AT SITE.
DO NOT SCALE THE DRAWING
IN THE EVENT OF ANY DISCREPANCIES OR DIFFERENCES BETWEEN ARCHITECTURAL DRAWINGS,STRUCTURAL DRAWINGS AND SITE CONDITIONS, IMMEDIATE REFERENCE IS TO BE MADE TO THE ARCHITECT PRIOR TO THE EXECUTION OF WORK AT THE SITE.

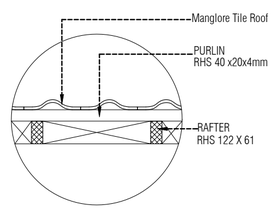

SECTION - 'CC'

STRUCTURAL CONSULTANT:

ARCHITECT:

CLIENT:

PROJECT:


DRAWING TITLE:


GROUND FLOOR - PATIOS AND COURTYARD ROOF LAYOUT

	INITIALS:	SIGNED BY:	DATE:
DRAWN BY:			
CHECKED BY:			
APPROVED BY:			


SCALE: | JOB NO: | REV:

DRAWING NUMBER:

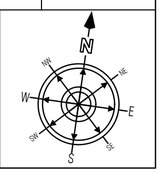

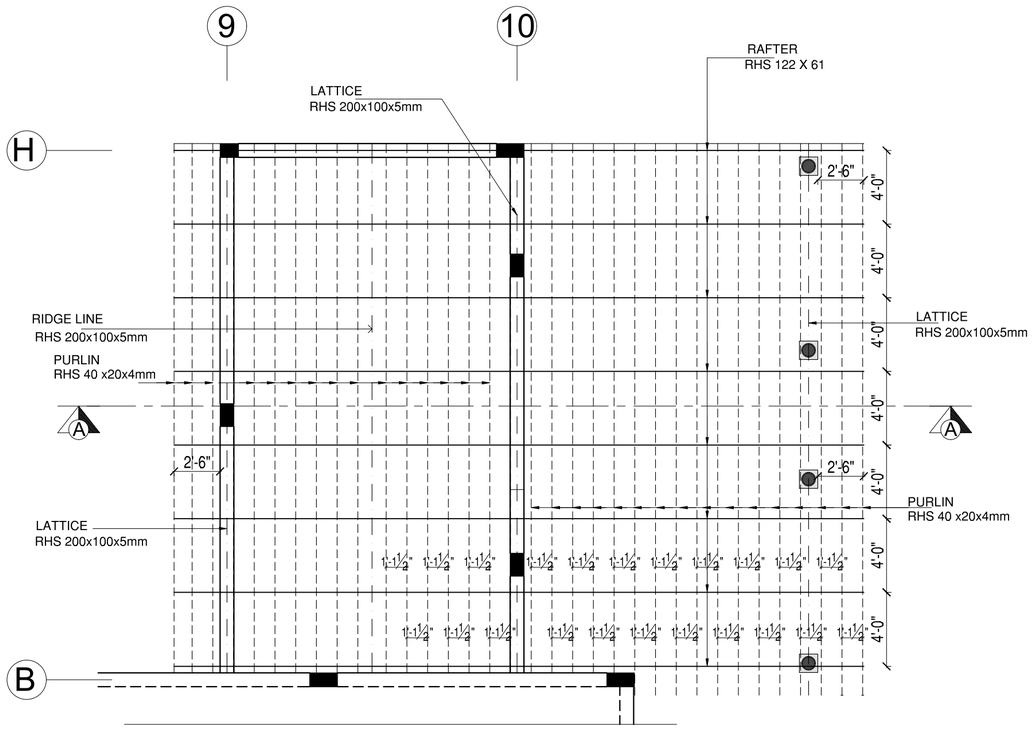

TRUSS & PURLIN LAYOUT
OUT DOOR SEATING AREA

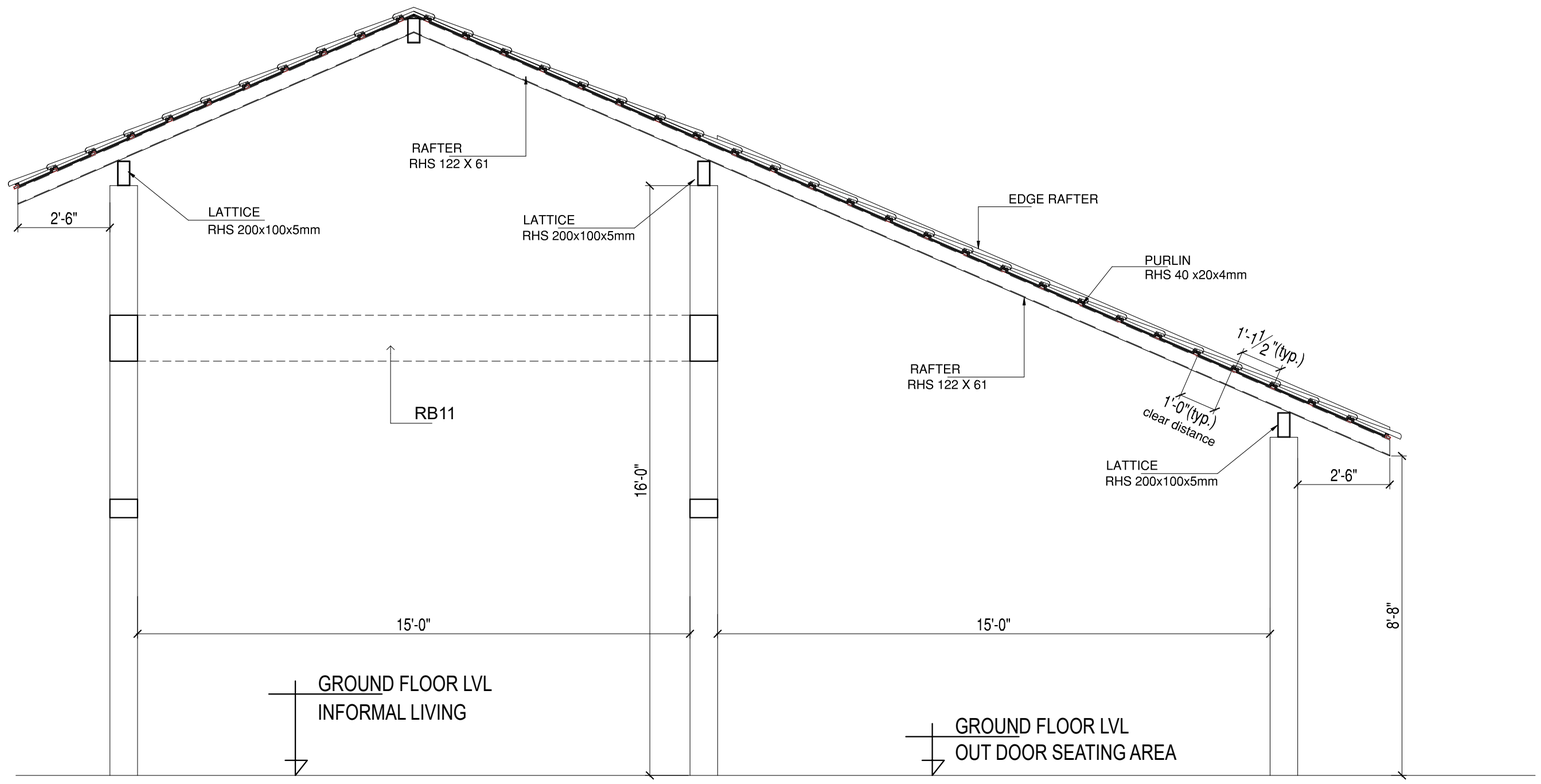

SECTION "A-A"

IMPORTANT NOTES :

1.ALL DIMENSIONS ARE IN FEET AND INCHES UNLESS OTHERWISE STATED.
2.DIMENSIONS ARE NOT TO BE SCALED.
3.ALL DIMENSIONS ARE TO BE VERIFIED PROPERLY AT SITE.
4.ALL DRAWINGS ARE TO BE READ IN CONJUNCTION WITH ALL OTHER RELEVANT DRAWINGS.
5.ANY DISCREPANCY IN THE DRG.SHALL BE BROUGHT TO CONSULTANTS NOTES BEFORE EXECUTION.
6.Y - DIA OF TOR STEEL
7.CLEAR COVER TO MAIN REINFORCEMENT(MILD EXPOSURE)
a) FOR BEAMS = 25 mm b) FOR SLABS = 20 mm
8.LAPPING
a) LAP LENGTH SHALL BE = 50 x DIA OF BAR.
b) DEVELOPMENT LENGTH SHALL BE = 50 x DIA OF BAR.
9.PROVIDE CHAIR RODS WHEREVER NECESSARY
10.PROVIDE SPACER RODS OF 25mm Ø (min) AT 1000mm C/C
11.GRADE OF CONCRETE IS M25
12.GRADE OF REINFORCING STEEL IS Fe 500
13.ALL THE LEVELS MENTIONED ARE FROM THE F.F.L. OF THE RESPECTIVE FLOOR
14.FLOOR FINISH ALLOWANCE SHALL BE 50 / 75 mm FROM THE RAW SLAB AS PER SITE INSTRUCTIONS.
13. REINFORCEMENT FABRICATION SHOULD BE DONE AS PER STANDARD DUCTILE DETAIL PROVIDED.
14. PROVISION OF CONDUITS / SLEEVES / CORECUTS TO BE PROVIDED AS PER SERVICE (ELECTRICAL / PLUMBING / HVAC) CONSULTANT'S DETAIL /DRAWINGS DULY APPROVED BY THE ARCHITECT / STRUCTURAL ENGINEER

GENERAL NOTES:

ALL DIMENSIONS TO BE CHECKED AT SITE.
DO NOT SCALE THE DRAWING
IN THE EVENT OF ANY DISCREPANCIES OR DIFFERENCES BETWEEN ARCHITECTURAL DRAWINGS,STRUCTURAL DRAWINGS AND SITE CONDITIONS, IMMEDIATE REFERENCE IS TO BE MADE TO THE STRUCTURAL ENGINEER PRIOR TO THE EXECUTION OF WORK AT THE SITE.
ONLY APPROVED DRAWINGS(i.e., SEALED AND DULLY SIGNED AS GOOD FOR CONSTRUCTION) MUST BE USED FOR EXECUTION OF WORKS AT SITE.
CLIENT / BUILDER ENSURES THAT STRICT ADHERENCE TO THE GOOD CONSTRUCTION PRACTICE IS FOLLOWED AT SITE AS PER THE RELEVANT B.I.S CODES.STRUCTURAL ENGINEER'S RESPONSIBILITY IS LIMITED TO DESIGNING & ISSUAL OF STRUCTURAL DRAWINGS ONLY.

COPYRIGHT :

THIS DRAWING IS A COPYRIGHT.
IT IS NOT TO BE REPRODUCED, COPIED, HANDED OVER TO A THIRD PARTY OR USED FOR ANY OTHER PURPOSE OTHER THAN FOR THE PROJECT INVOLVED WITHOUT THE KNOWLEDGE OF THE STRUCTURAL ENGINEER.

REV	REVISION DESCRIPTION	DATE

STRUCTURAL CONSULTANT:

Team 3 Associates
Architecture | Engineering | Interior | Landscape
JKR Towers,Door No: 5/6,
Moonlight Gardens,
Sitra-Kalapatti Rl,Kalapatti,
Coimbatore - 641048, India.
E-mail : drafting@t3associates.in
Phone : +91-0422-4206657

CLIENT:
KRISHNA AISHWARYAM,
COIMBATORE.

PROJECT:
PROPOSED RESIDENTIAL BUILDING
AT COIMBATORE.

DRAWING TITLE:
OutDoor Seating- TILE ROOF TRUSS DETAIL

	INITIALS:	SIGNED BY:	DATE:
DRAWN BY:			
CHECKED BY:			
APPROVED BY:			

SCALE: NTS	JOB NO: 26 - KA - 01	REV: 00

REFERENCE:

DRAWING NUMBER:	SHEET NUMBER:
ST - RF- GF - 02	01