




DETAIL AT- B

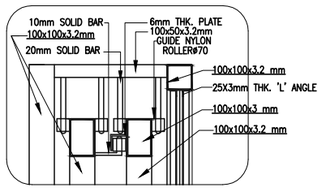


DETAIL – C

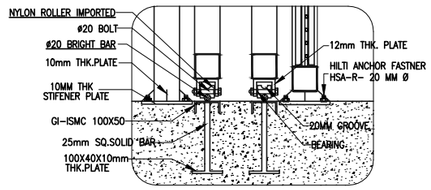


DETAIL – D

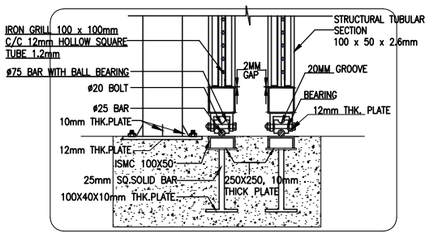


DETAIL – E

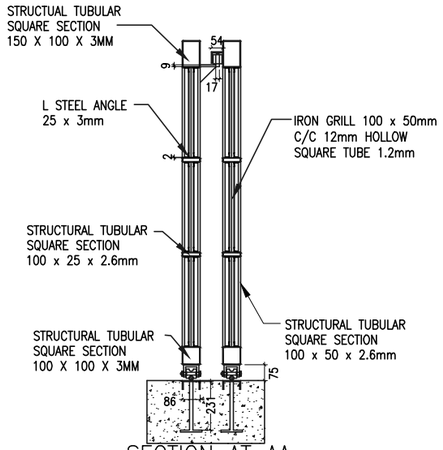


SECTION AT AA
SCALE 1:25

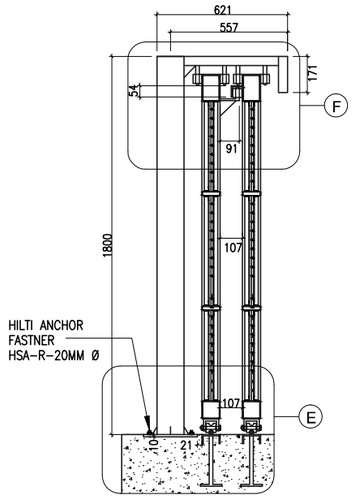


SECTION AT BB
SCALE 1:25

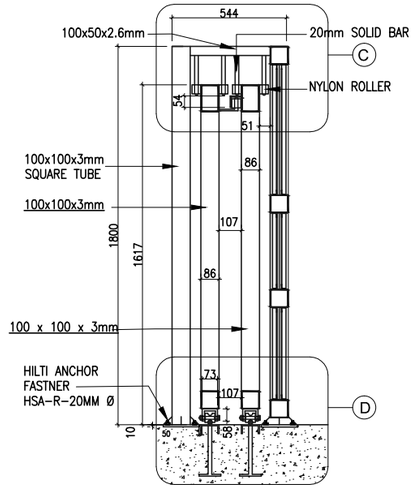


SECTION AT CC
SCALE 1:25

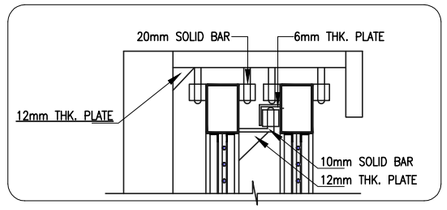

DETAIL – F

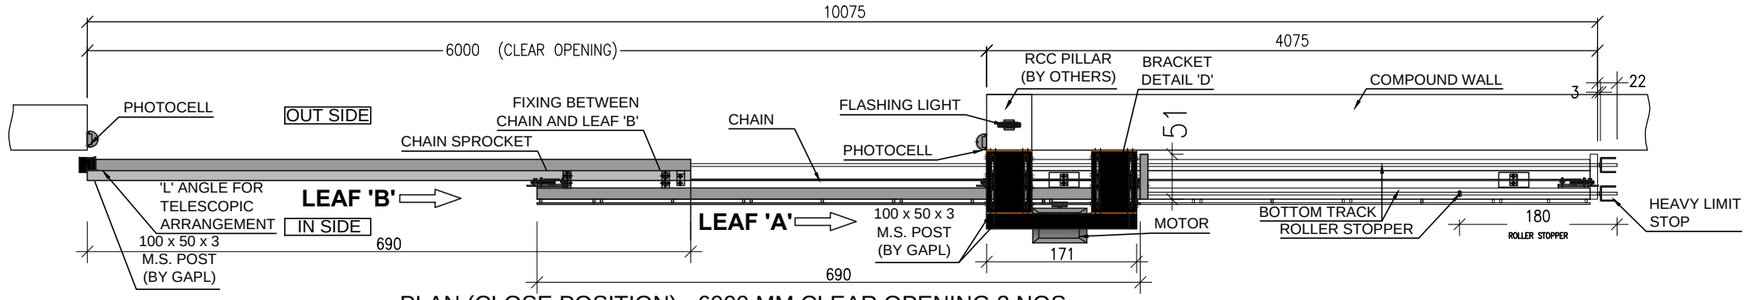


PLAN (CLOSE POSITION) - 6000 MM CLEAR OPENING 2 NOS

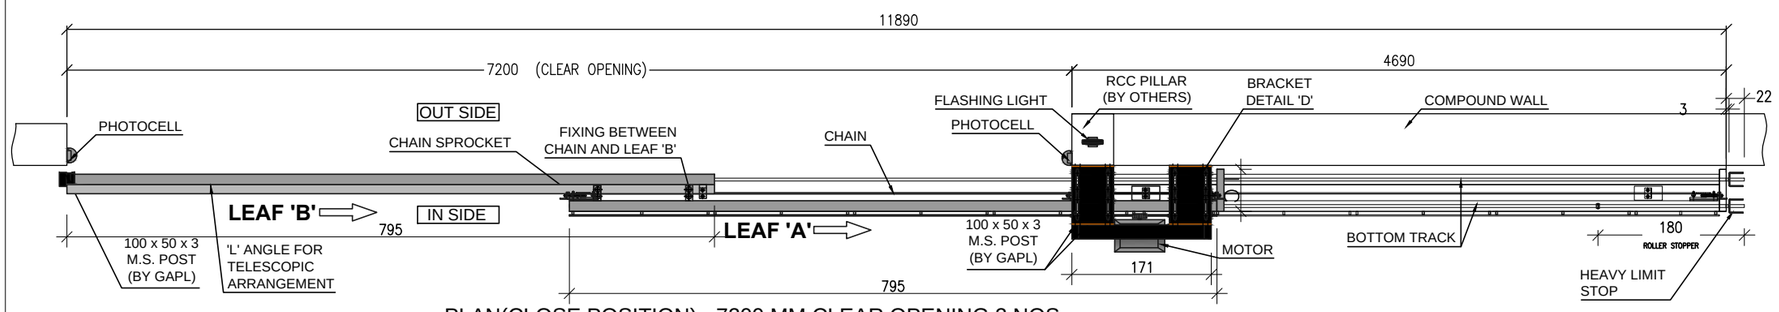

PLAN(CLOSE POSITION) - 7200 MM CLEAR OPENING 2 NOS

KEY PLAN :-

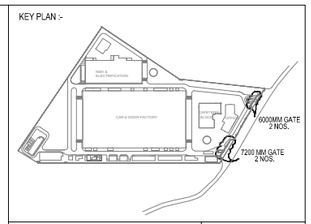

N

GENERAL NOTES :

- ALL DIMENSIONS ARE IN MILLIMETRES AND ARE UNFINISHED DIMENSIONS UNLESS OTHERWISE SPECIFIED.
- ALL LEVELS ARE IN METRES AND ARE UNFINISHED LEVELS UNLESS OTHERWISE SPECIFIED.
- DO NOT SCALE DRAWINGS. ONLY WRITTEN DIMENSIONS SHALL BE FOLLOWED. ANY DISCREPANCIES NOTED SHALL BE BROUGHT TO THE NOTICE OF THE ARCHITECT PRIOR TO EXECUTION.

REV.	DESCRIPTION	DATE	BY	CHD.
T2	ISSUED FOR TENDER	02.03.17	SV	VA
T1a	ISSUED FOR CLIENT REVIEW	25.11.16	SV	VA
T1	ISSUED FOR TENDER	01.04.15	MB	VA

AMENDMENT

GRAPHIC SCALE: 0 1M 4M 6M / 1M 0 2M 6M 10M

CLIENT:
KONE ELEVATOR INDIA PVT. LTD.

PROJECT:
PROPOSED KONE ELEVATOR FACTORY
AT PILLAIPAKKAM, NEAR CHENNAI.

DRAWING TITLE:
STANDARD DETAILS -
TELESCOPIC SLIDING GATE DETAIL

SCALE : 1: 100 ; 75	DRAWN : MB	REV
DATE : 01.04.2015	CHKD : V.A.	
DRAWING NO: KEIPL-P-FAC-AR20-50-01-191822		T2

ARCHITECTURE • INTERIOR DESIGN • ENGINEERING • PLANNING • CONSTRUCTION MANAGEMENT
C R NARAYANA RAO
10, KARPAGAMBAL NAGAR,
MYLAPORE, CHENNAI-600 004

B.Arch. (Hons.), M.Arch., (Calif.), F.I.I.A., IntlAssoc.A.I.A.,
Registered Architect.

STANDARD DETAILS