

Weitergabe sowie Vervielfältigung dieses Dokuments, Verwertung und Mitteilung seines Inhalts sind nur nach vorheriger ausdrücklicher schriftlicher Zustimmung von SMS Meer GmbH gestattet. Das Dokument ist vor unberechtigtem Zugriff Dritter zu schützen. Zuwiderhandlungen verpflichten zu Schadenersatz. Alle Rechte aus Patent-/Gebrauchsmuster-/Markenschutz vorbehalten.


Schnitt (Section) S14-01 - S14-01

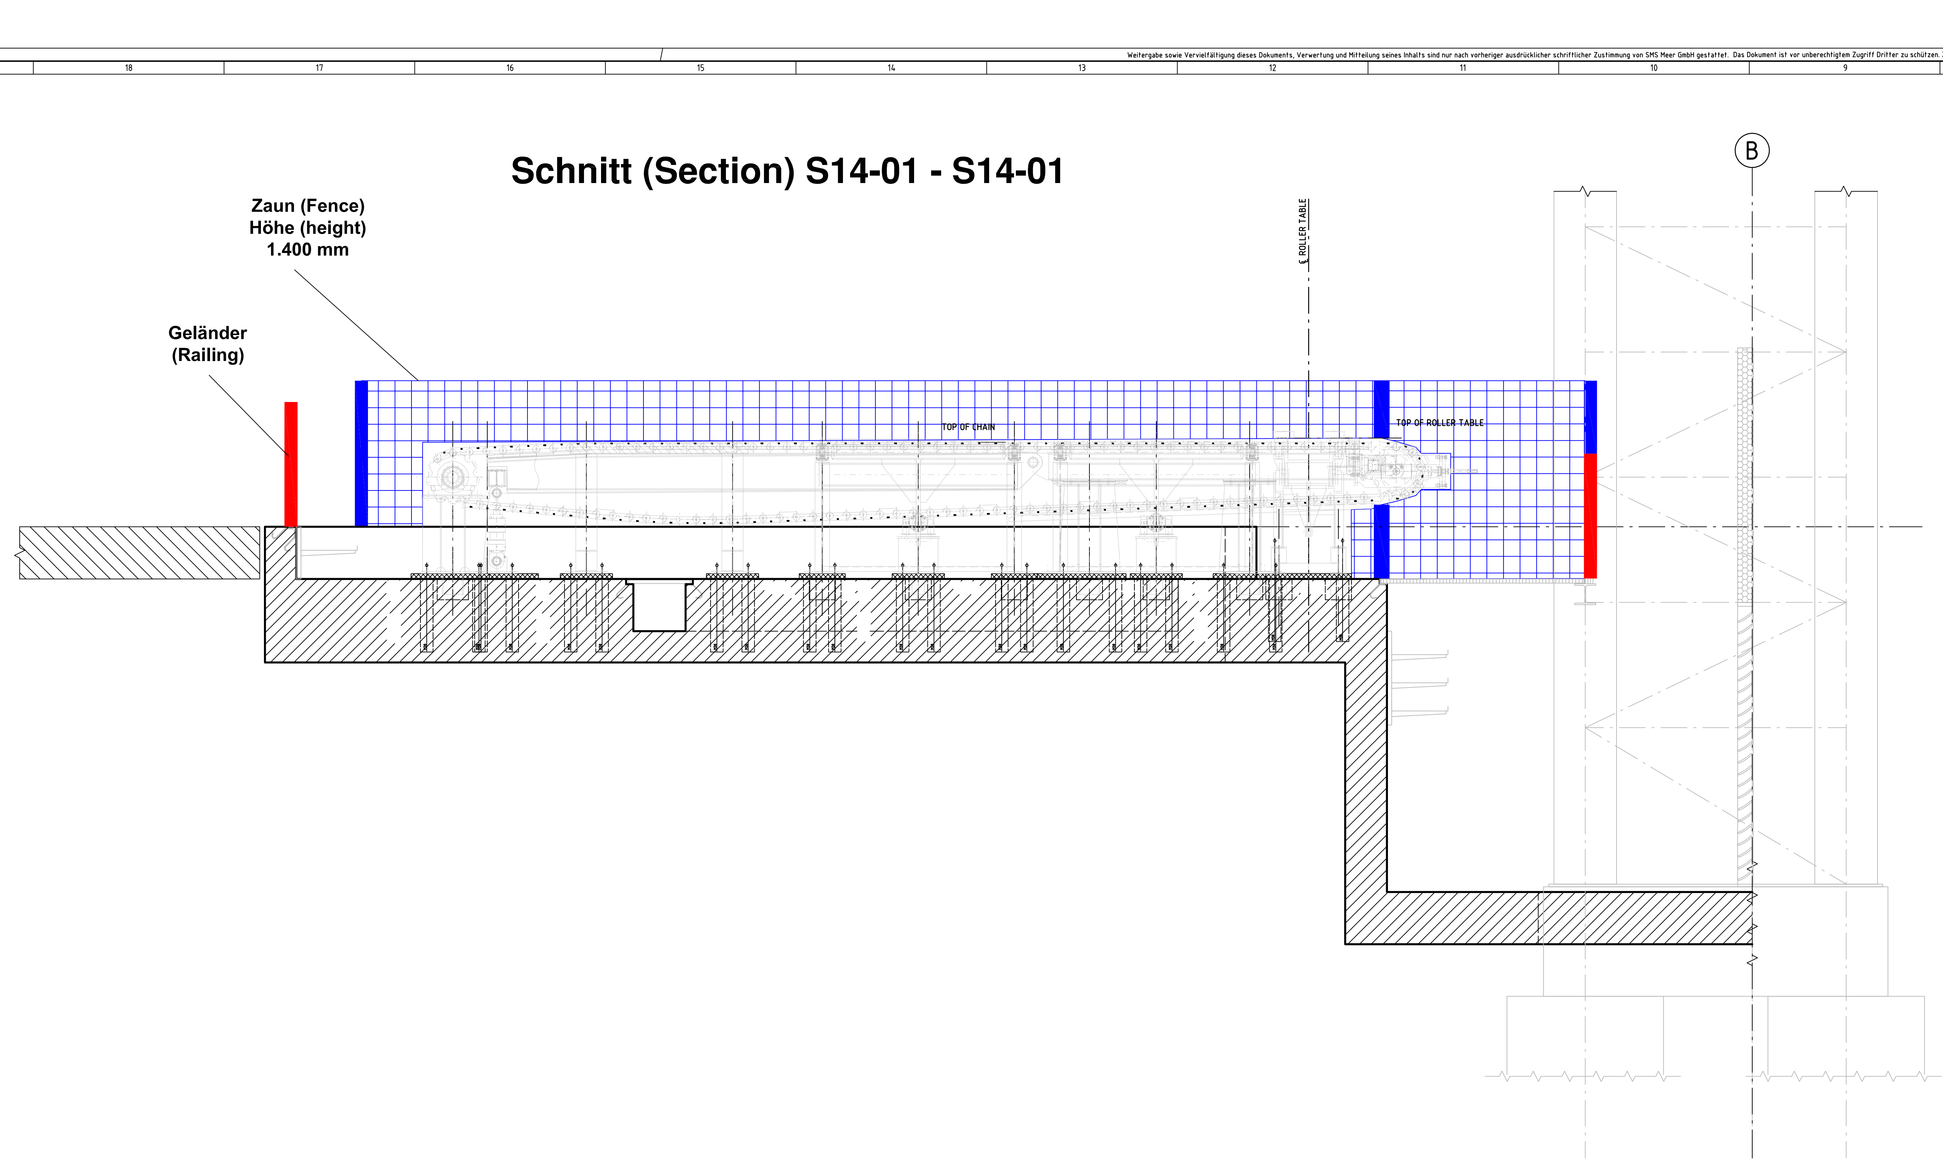


Schnitt (Section) S14-02 - S14-02

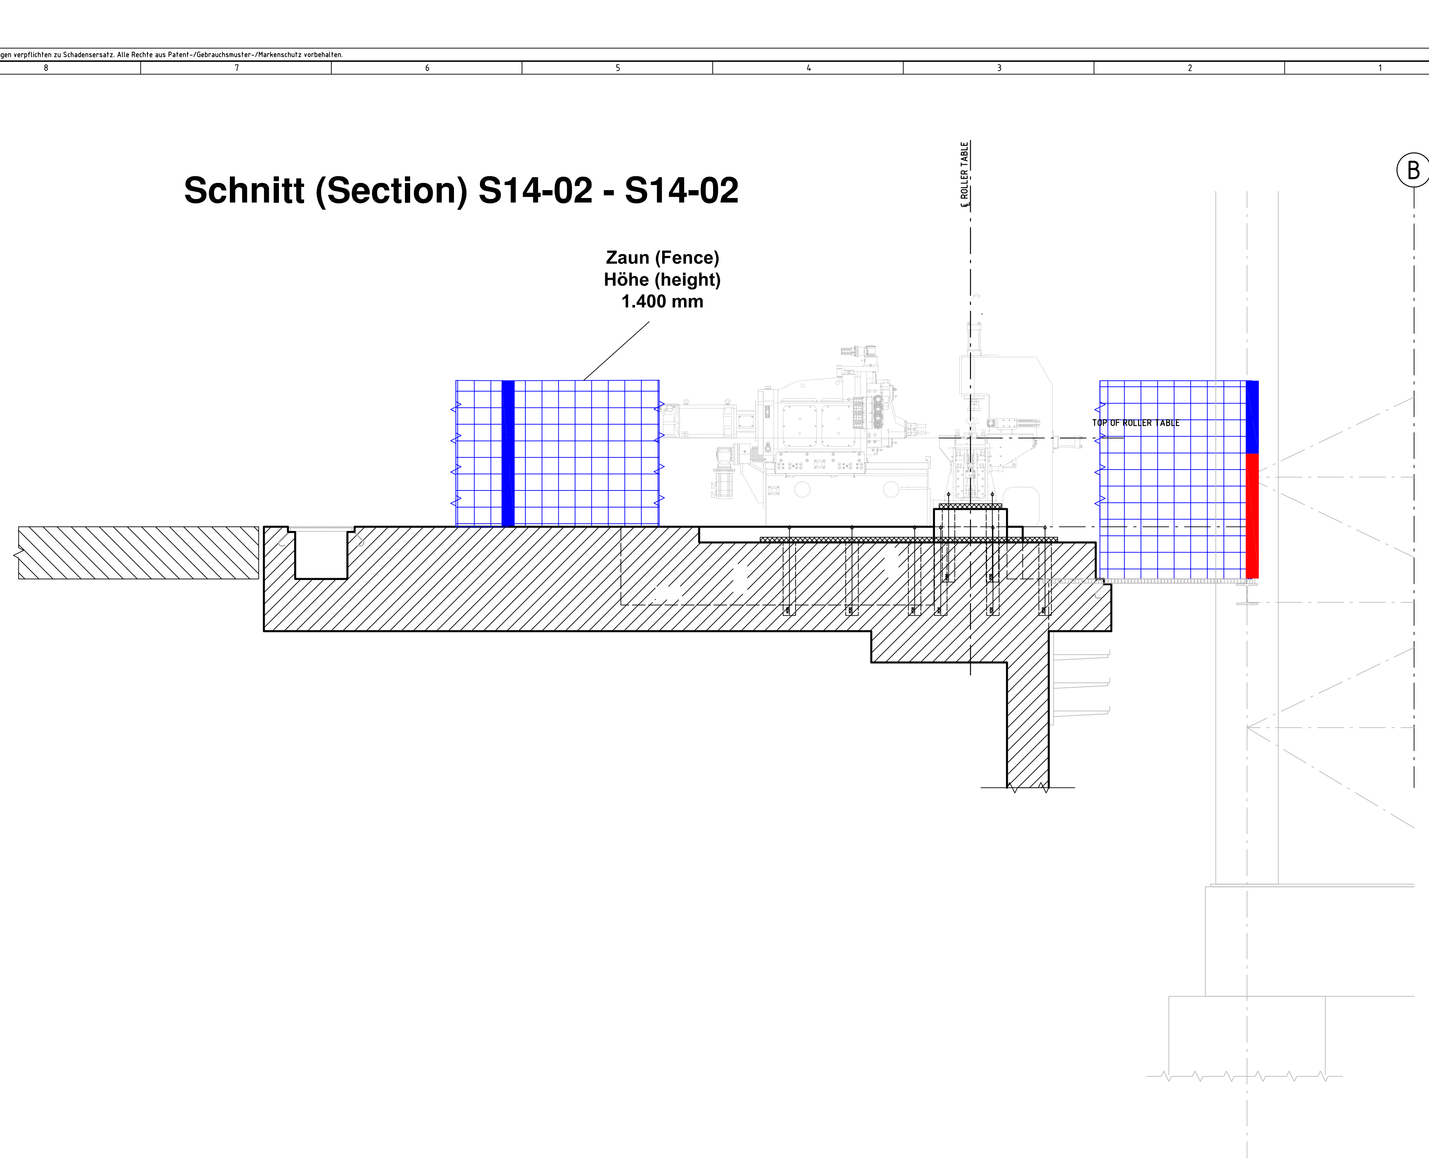

Schnitt (Section) S14-03 - S14-03

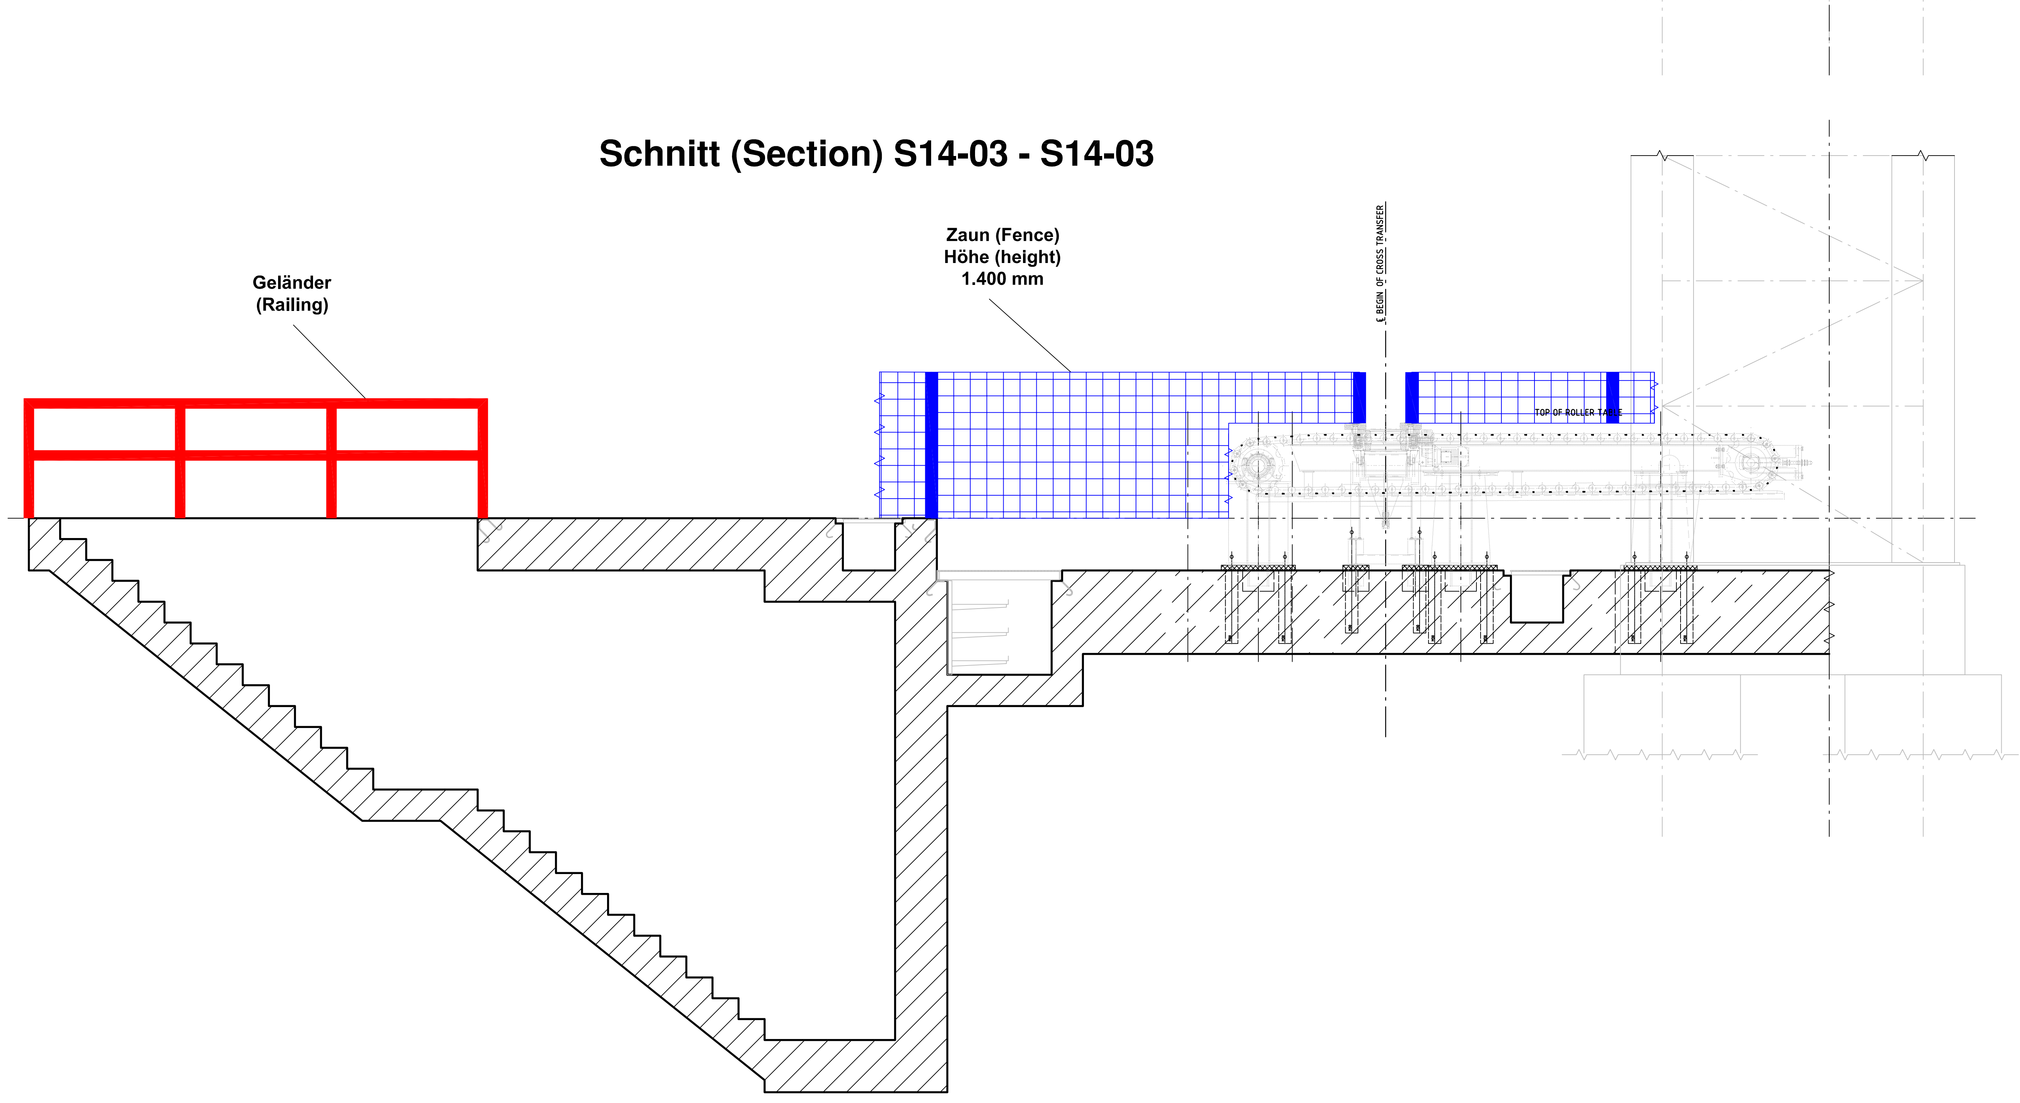

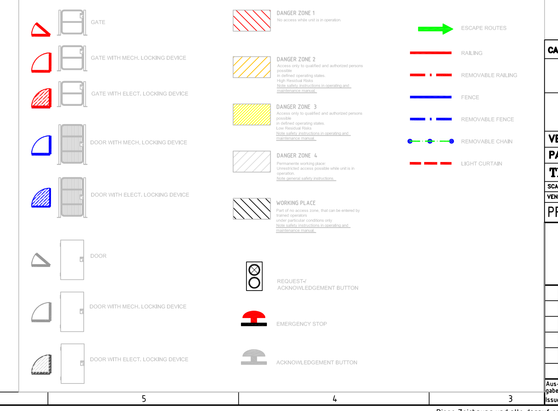

9463 0000/ RAILBHL

CATEGORY OF DRWG.	APPROVAL	INFORMATION	REFERENCE	RECORD	CONSTRUCTION

BHILAI STEEL PLANT, BHILAI, CHATTISGARH
7,0 MTPA EXPANSION

मेकॉन लिमिटेड
MECON LIMITED

VENDOR'S NAME:	SMS Meer/SMS Meer India/ABB
PACKAGE DESCRIPTION:	UNIVERSAL RAIL MILL (Pkg No-047)
TITLE OF DRAWING.	PARTITION 14, Safety Layout
KHUD/ VENDOR'S DRG NO.:	
PROJECT DRG. NO.	BSP-SMS Meer-08-047-21-130-35-BE-06661
REV.	

Fertigungsvorschriften / Manufacturing Instructions: SN 200

Ursprung / Origin | Fertiggewicht / Finished weight: kg | Modell-Nr. / Pattern-No. | Projektionsmethode / First angle projection method ISO 128

Werkstoff / Material

	Datum / Date	Name
Bearb. / Drawn	19.10.11	Piratzel
Gepr. / Checked	19.10.11	Piratzel
Norm / Appd.		

Typ / Type: Safety Layout | Maßstab / Scale: 1:25

Bezeichnung / Title: Teilbereich, 14

Title: PARTITION 14

Sach-Nr. / Drawing-No.: 0100133-00.661

Blatt / Sheet: 1 | Blattzahl / Sheets: 2

Ersatz für / Supersedes:

Ersetzt durch / Superseded by:

SMS MEER, SMS group

Änderung / Revision	Datum / Date	Name
Aen. Index / Mod.		

Diese Zeichnung und alle darauf enthaltenen Informationen sind vertraulich. This drawing and all information on it is confidential.