



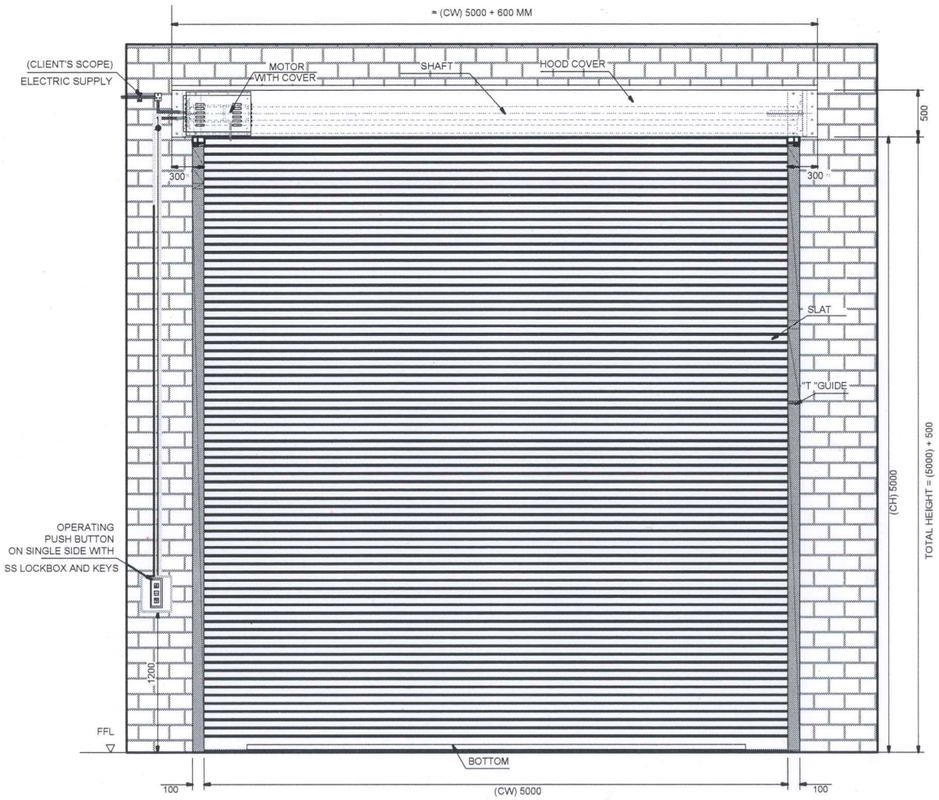

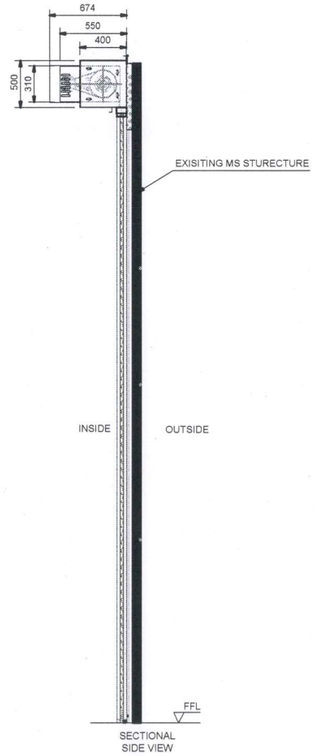

INSIDE ELEVATION

TECHNICAL SPECIFICATION:-

SR.	SPECIFICATION	DETAILS
1.	Description & Drive	Motorised Rolling Shutter (direct Drive)
2.	Location Area	Inside
3.	Mounting Surface	WALL MOUNTING
4.	Slat	AS PER NIHVA STD.
5.	Bottom Profile	MS Plate 100 x 2.5 mm thick with Angle Stiffner with rubber seal
6.	Guide Profile	M.S." T " Shape profile 100 x 3 mm Thk.
7.	Hood Cover & Motor Cover	Made of GI Sheet Thickness 0.9 mm
8.	Surface finish	PRIMER + 1 LAYER OF QD PAINT
9	Accessories	Push Button Single side

AR update AS PER PEB DWG.

RS1 = 5 X 5m

SHUTTER SIZES :-

SR.	CLEAR WIDTH	CLEAR HEIGHT	QTY.
01	5000 mm	5000 mm	3

SHAH & TALATI VADODARA Design Engineering

Hrd Dogra D-30/01/25


Note :-
1. All Dimension are in mm
2. This drawing is only for understanding purpose

This drawing & designing is the property of NIHVA TECHNOLOGIES. Not to be sold or copied to any other concern.

TITLE :- MOTORISED ROLLING SHUTTER


NIHVA TECHNOLOGIES PVT. LTD. PUNE
Tel : 020 66304033
Email:- info@nihva.com
Website:- www.nihva.com

	NAME	DATE	
			CLIENT - SMP INFRASTRUCTURE PVT. LTD.
DRAWN	B.S.	24/01/2025	PROJECT - ROLLING SHUTTER
CHECK	V.M.	24/01/2025	FORMAT NO - NIHVA-DD-F-03
APPROVAL	V.T.	24/01/2025	DWG. NO. : NIHVA/24-25/SMP/250124 REV-00
			SCALE: NTS WT: SHEET: 01 OF 01
ALL DIMENSION ARE IN mm			If any queries contact : design@nihva.com

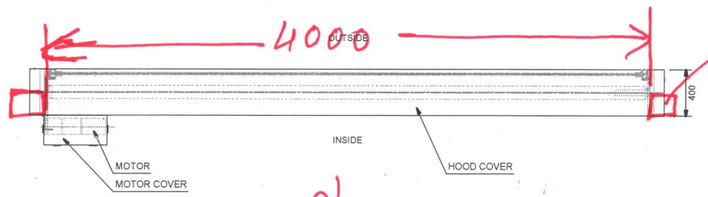


150X150 BOX STRUCTURE AS PER PEB DWG. (TYP. comments)


Plan :-

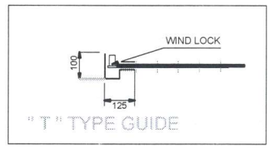

SHS

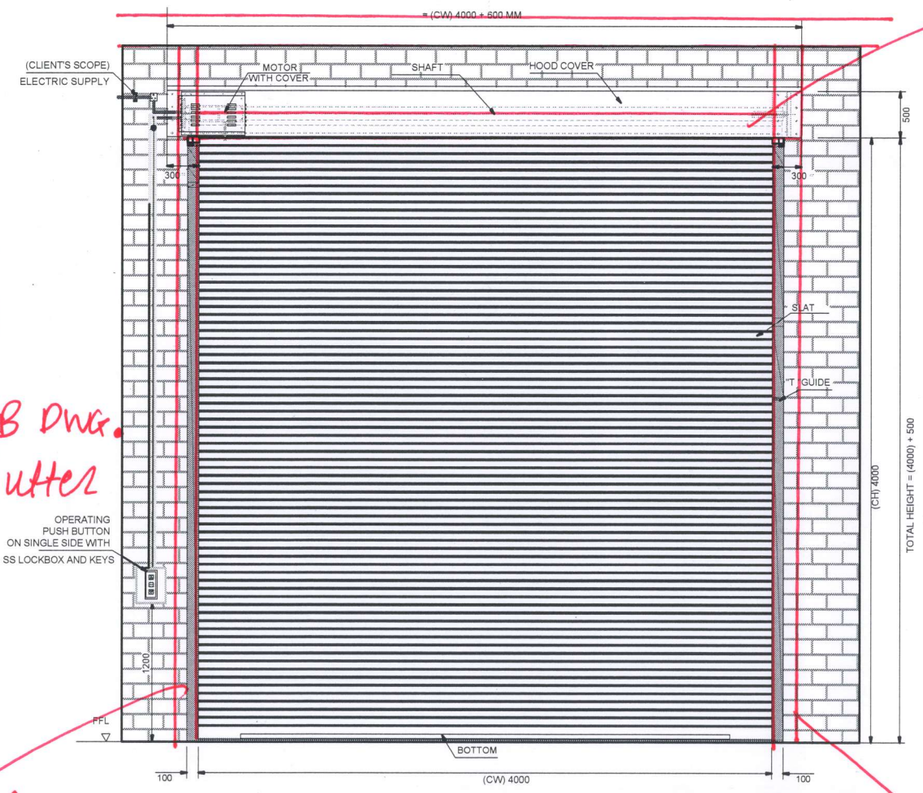

OR UPDATE Elevation AS PER PEB DWG. Rolling shutter Frame.

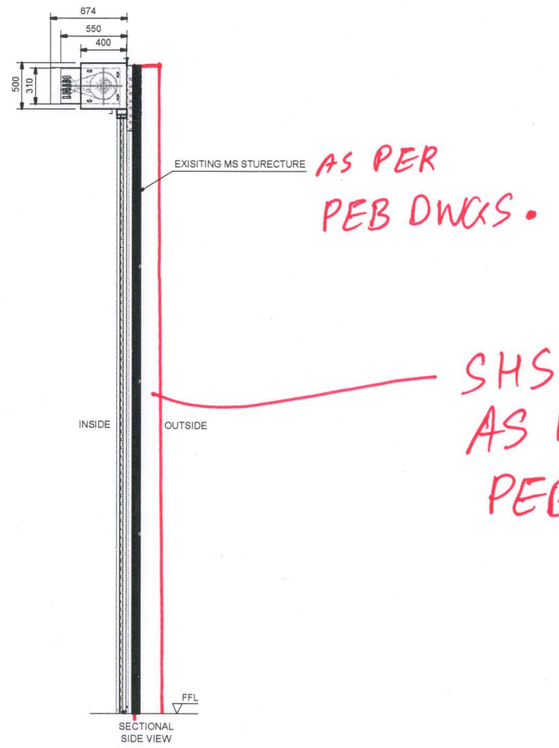

AS PER PEB DWGS.

SHS AS PER PEB.

SHS

INSIDE ELEVATION

TECHNICAL SPECIFICATION:-

SR.	SPECIFICATION	DETAILS
1.	Description & Drive	Motorised Rolling Shutter (direct Drive)
2.	Location Area	Inside
3.	Mounting Surface	WALL MOUNTING SHS 150x150 size AS PER PEB.
4.	Slat	AS PER NIHVA STD.
5.	Bottom Profile	MS Plate 100 x 2.5 mm thick with Angle Stiffner with rubber seal
6.	Guide Profile	M.S." T " Shape profile 100 x 3 mm Thk.
7.	Hood Cover & Motor Cover	Made of GI Sheet Thickness 0.9 mm
8.	Surface finish	PRIMER + 1 LAYER OF QD PAINT
9	Accessories	Push Button Single side

SHAH & TALATI VADODARA Design Engineering Data

D -30/01/25

RS02 = 4 X 4m

SHUTTER SIZES :-


SR.	CLEAR WIDTH	CLEAR HEIGHT	QTY.
01	4000 mm	4000 mm	1


Note :-


1. All Dimension are in mm
2. This drawing is only for understanding purpose

This drawing & designing is the property of NIHVA TECHNOLOGIES. Not to be sold or copied to any other concern


TITLE :- MOTORISED ROLLING SHUTTER			NIHVA TECHNOLOGIES PVT. LTD. PUNE Tel : 020 66304033 Email:- info@nihva.com Website:- www.nihva.com
	NAME	DATE	CLIENT - SMP INFRASTRUCTURE PVT. LTD.
DRAWN	B.S.	24/01/2025	PROJECT - ROLLING SHUTTER
CHECK	V.M.	24/01/2025	FORMAT NO - NIHVA-DD-F-03
APPROVAL	V.T.	24/01/2025	DWG. NO. : NIHVA/24-25/SMP/250124 — REV-00
			SCALE: NTS — WT: — SHEET: 01 OF 01
ALL DIMENSION ARE IN mm			If any queries contact : design@nihva.com

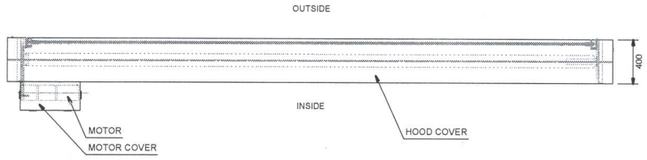

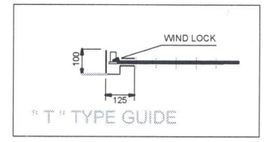

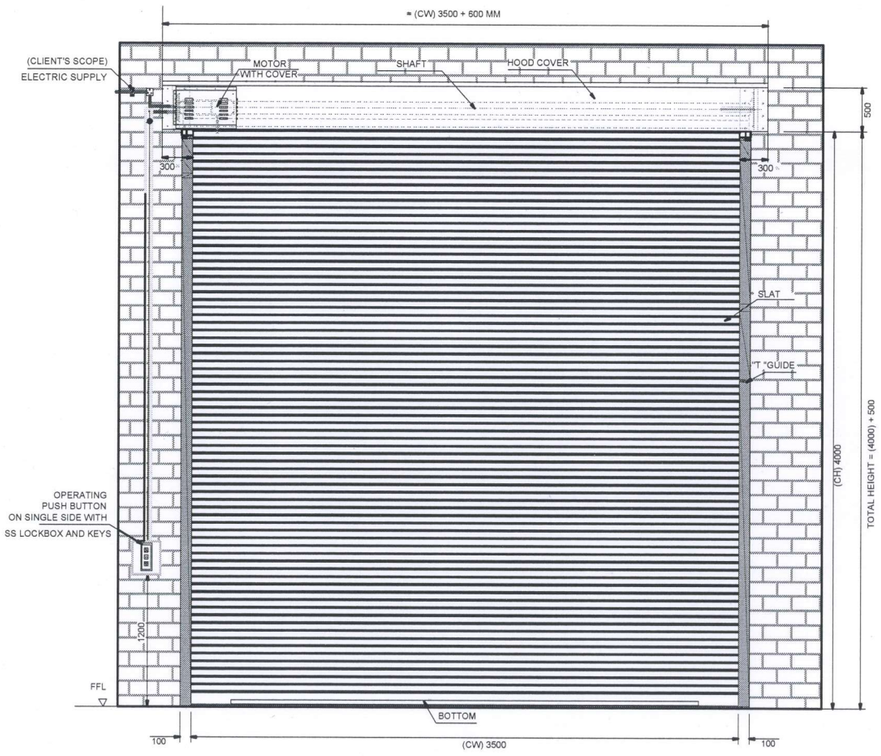

INSIDE ELEVATION

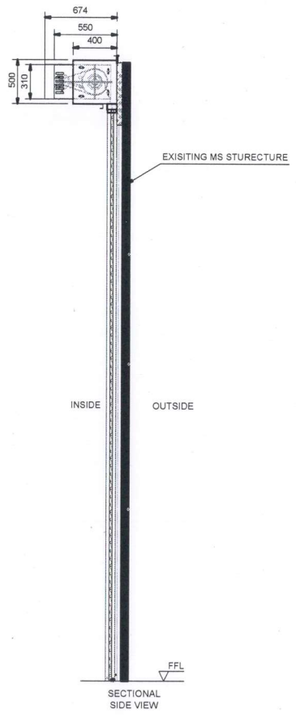

TECHNICAL SPECIFICATION:-

SR.	SPECIFICATION	DETAILS
1.	Description & Drive	Motorised Rolling Shutter (direct Drive)
2.	Location Area	Inside
3.	Mounting Surface	WALL MOUNTING
4.	Slat	AS PER NIHVA STD.
5.	Bottom Profile	MS Plate 100 x 2.5 mm thick with Angle Stiffner with rubber seal
6.	Guide Profile	M.S." T " Shape profile 100 x 3 mm Thk.
7.	Hood Cover & Motor Cover	Made of GI Sheet Thickness 0.9 mm
8.	Surface finish	PRIMER + 1 LAYER OF QD PAINT
9	Accessories	Push Button Single side

SHS 150 X 150 SIZE AS PER PEB DWG.

RS03 = 3.5 X 4.0 m

SHUTTER SIZES :-

SR.	CLEAR WIDTH	CLEAR HEIGHT	QTY.
01	3500 mm	4000 mm	3

SHAH & TALATI Design Engineering VADODARA

Vrad Vora 30/01/25

RAL 9002 color code For All RS (TYP. comments)

Note :-

1. All Dimension are in mm
2. This drawing is only for understanding purpose


This drawing & designing is the property of NIHVA TECHNOLOGIES. Not to be sold or copied to any other concern

TITLE :- MOTORISED ROLLING SHUTTER

NIHVA TECHNOLOGIES PVT. LTD. PUNE
Tel : 020 66304033
Email:- info@nihva.com
Website:- www.nihva.com


	NAME	DATE	
DRAWN	B.S.	24/01/2025	CLIENT - SMP INFRASTRUCTURE PVT. LTD.
CHECK	V.M.	24/01/2025	PROJECT - ROLLING SHUTTER
APPROVAL	V.T.	24/01/2025	FORMAT NO - NIHVA-DD-F-03
			DWG. NO. : NIHVA/24-25/SMP/250124 REV-00
			SCALE: NTS WT: SHEET: 01 OF 01
ALL DIMENSION ARE IN mm			If any queries contact : design@nihva.com

BRICK WALL

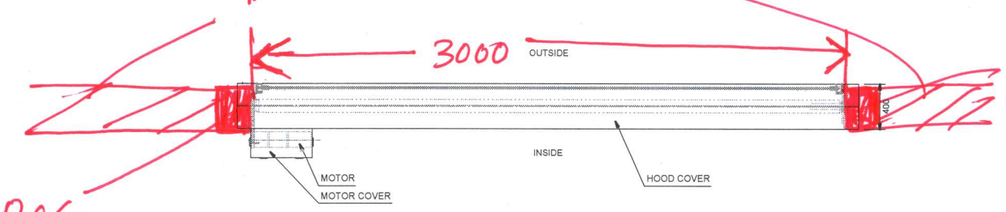

RCC column

RCC column

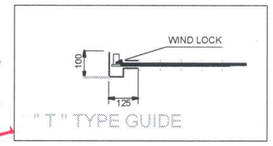


BRICK WALL


450 RCC BEAM

BRICK masonry

450 concrete beam

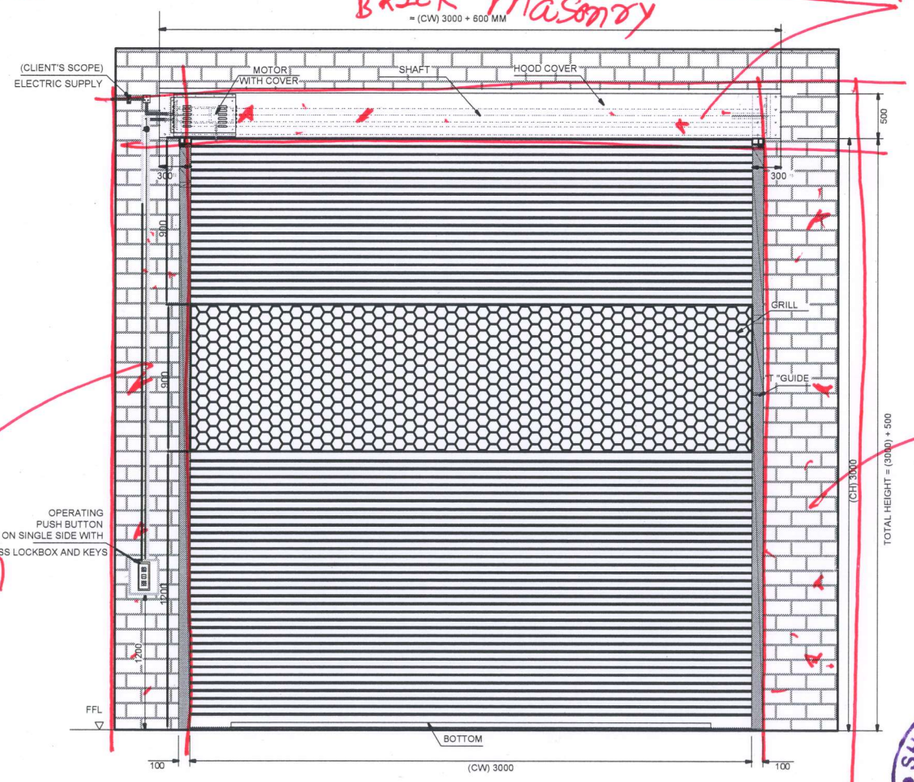

RCC column

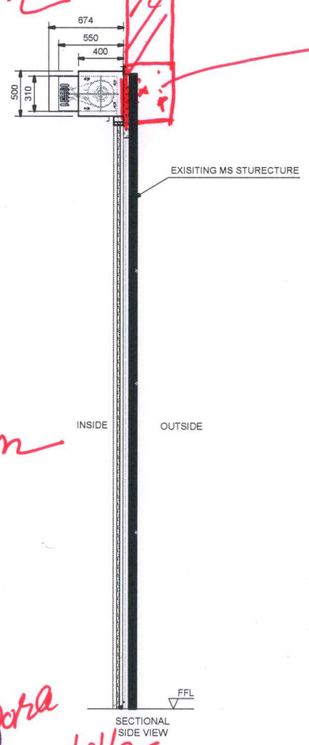

INSIDE ELEVATION

SHAH & TALATI VADODARA Design Engineering

D-30/01/25

TECHNICAL SPECIFICATION:-

SR.	SPECIFICATION	DETAILS
1.	Description & Drive	Motorised Rolling Shutter (direct Drive) European Make Motors
2.	Location Area	Inside
3.	Mounting Surface	WALL MOUNTING + RCC column
4.	Slat	AS PER NIHVA STD.
5.	Bottom Profile	MS Plate 100 x 2.5 mm thick with Angle Stiffner with rubber seal
6.	Guide Profile	M.S." T " Shape profile 100 x 3 mm Thk.
7.	Hood Cover & Motor Cover	Made of GI Sheet Thickness 0.9 mm
8.	Surface finish	PRIMER + 1 LAYER OF QD PAINT — Synthetic Enamel Paint AS PER BOQ.
9	Accessories	Push Button Single side

RS04 = 3X3m

SHUTTER SIZES :-

SR.	CLEAR WIDTH	CLEAR HEIGHT	QTY.
01	3000 mm	3000 mm	1

* ALL Technical Specifications shall be considered AS PER BOQ. (TYP. comments FOR ALL RS)

Note :-

1. All Dimension are in mm
2. This drawing is only for understanding purpose


This drawing & designing is the property of NIHVA TECHNOLOGIES. Not to be sold or copied to any other concern.


TITLE :- MOTORISED ROLLING SHUTTER


NIHVA TECHNOLOGIES PVT. LTD. PUNE
Tel : 020 66304033
Email:- info@nihva.com
Website:- www.nihva.com

	NAME	DATE
DRAWN	B.S.	24/01/2025
CHECK	V.M.	24/01/2025
APPROVAL	V.T.	24/01/2025


CLIENT - SMP INFRASTRUCTURE PVT. LTD.
PROJECT - ROLLING SHUTTER
FORMAT NO - NIHVA-DD-F-03
DWG. NO. : NIHVA/24-25/SMP/250124 | REV-00
SCALE: NTS | WT: | SHEET: 01 OF 01
ALL DIMENSION ARE IN mm
If any queries contact : design@nihva.com

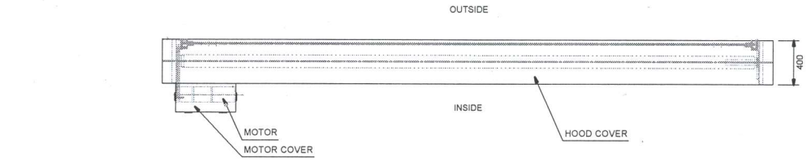

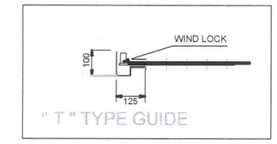

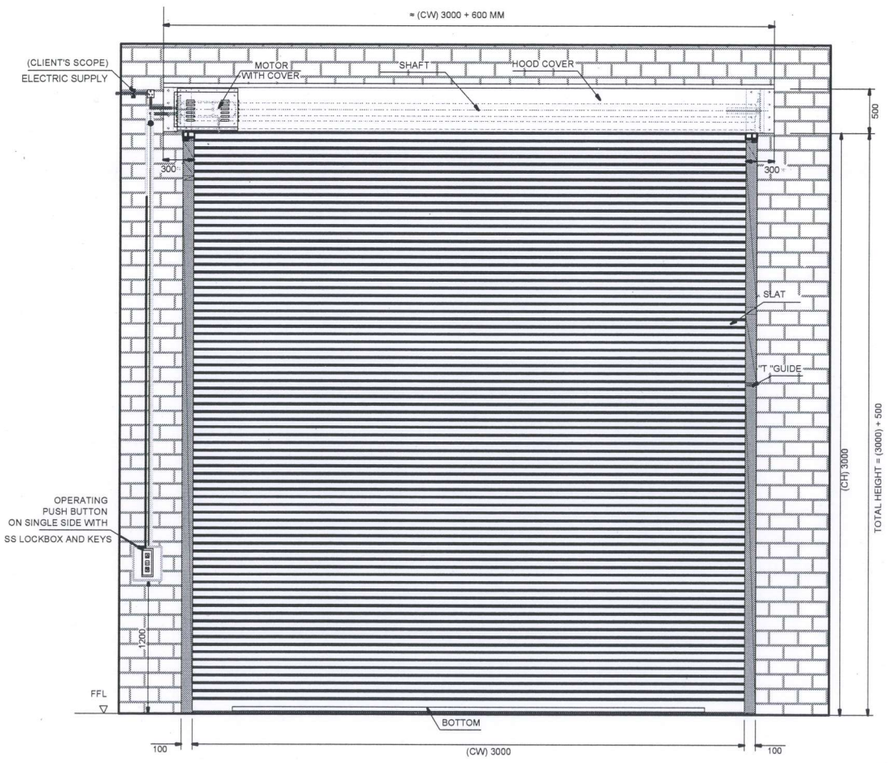

INSIDE ELEVATION

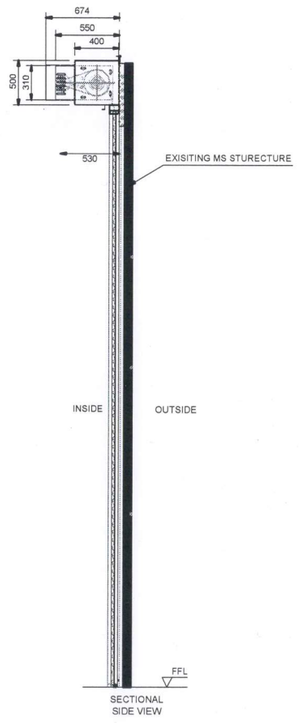

TECHNICAL SPECIFICATION:-

SR.	SPECIFICATION	DETAILS
1.	Description & Drive	Motorised Rolling Shutter (direct Drive)
2.	Location Area	Inside
3.	Mounting Surface	WALL MOUNTING
4.	Slat	AS PER NIHVA STD.
5.	Bottom Profile	MS Plate 100 x 2.5 mm thick with Angle Stiffner with rubber seal
6.	Guide Profile	M.S." T " Shape profile 100 x 3 mm Thk.
7.	Hood Cover & Motor Cover	Made of GI Sheet Thickness 0.9 mm
8.	Surface finish	PRIMER + 1 LAYER OF QD PAINT
9	Accessories	Push Button Single side

update AS PER PEB DWG. SHS 150 x 150 size

RS05 = 3 x 3m

SHAH & TALATI VADODARA Design Engineering Dept. D - 30/01/25

SHUTTER SIZES :-

SR.	CLEAR WIDTH	CLEAR HEIGHT	QTY.
01	3000 mm	3000 mm	2

Note :-
1. All Dimension are in mm
2. This drawing is only for understanding purpose

This drawing & designing is the property of NIHVA TECHNOLOGIES. Not to be sold or copied to any other concern


TITLE :- MOTORISED ROLLING SHUTTER


NIHVA TECHNOLOGIES PVT. LTD. PUNE
NIHVA TECHNOLOGIES PVT. LTD.
Tel : 020 66304033
Email:- info@nihva.com
Website:- www.nihva.com


	NAME	DATE	
DRAWN	B.S.	24/01/2025	CLIENT - SMP INFRASTRUCTURE PVT. LTD.
CHECK	V.M.	24/01/2025	PROJECT - ROLLING SHUTTER
APPROVAL	V.T.	24/01/2025	FORMAT NO - NIHVA-DD-F-03
			DWG. NO. : NIHVA/24-25/SMP/250124 — REV-00
			SCALE: NTS — WT: — SHEET: 01 OF 01

ALL DIMENSION ARE IN mm


If any queries contact : design@nihva.com

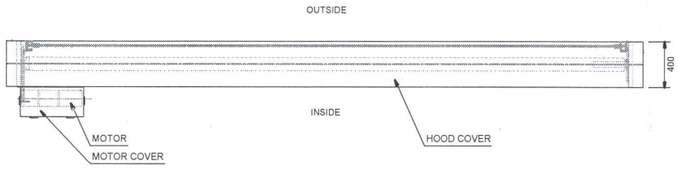

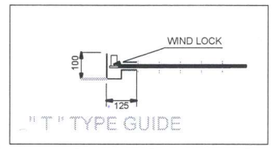

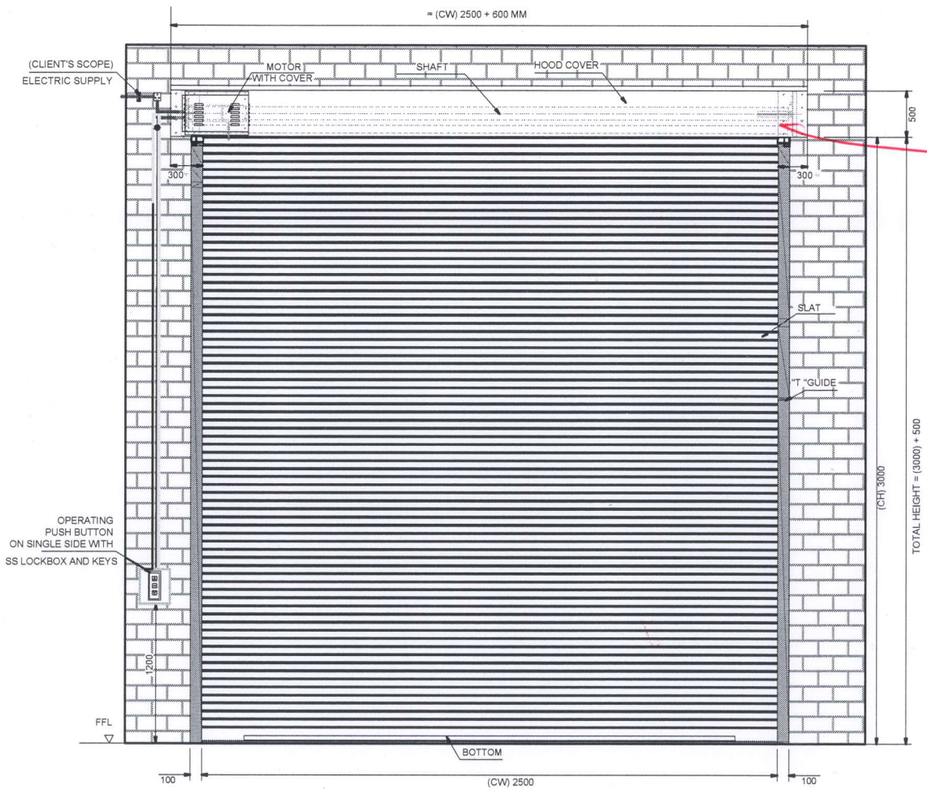

INSIDE ELEVATION

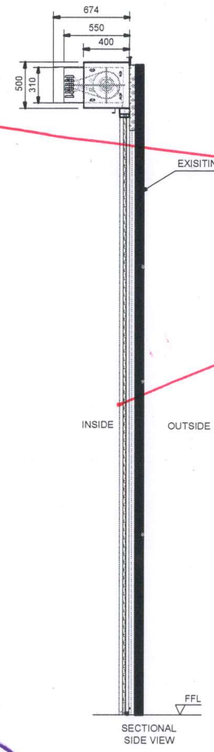

Update Elevation & side view AS PER PEB Rolling Shutter Frame. DWG. (TYP.) Comments) FOR ROLLING SHUTTERS.

SHAH & TALATI VADODARA Design Engineering

Dhaval Patel D-30/01/25

TECHNICAL SPECIFICATION:-

SR.	SPECIFICATION	DETAILS
1.	Description & Drive	Motorised Rolling Shutter (direct Drive)
2.	Location Area	Inside
3.	Mounting Surface	WALL MOUNTING SHS 150 X 150 SIZE AS PER PEB.
4.	Slat	AS PER NIHVA STD.
5.	Bottom Profile	MS Plate 100 x 2.5 mm thick with Angle Stiffner with rubber seal
6.	Guide Profile	M.S." T " Shape profile 100 x 3 mm Thk.
7.	Hood Cover & Motor Cover	Made of GI Sheet Thickness 0.9 mm
8.	Surface finish	PRIMER + 1 LAYER OF QD PAINT
9	Accessories	Push Button Single side

RS06 = 2500 X 3000

SHUTTER SIZES :-

SR.	CLEAR WIDTH	CLEAR HEIGHT	QTY.
01	2500 mm	3000 mm	1

Note :-
1. All Dimension are in mm
2. This drawing is only for understanding purpose

This drawing & designing is the property of NIHVA TECHNOLOGIES. Not to be sold or copied to any other concern.

TITLE :- MOTORISED ROLLING SHUTTER			NIHVA TECHNOLOGIES PVT. LTD. PUNE Tel : 020 66304033 Email:- info@nihva.com Website:- www.nihva.com
	NAME	DATE	CLIENT - SMP INFRASTRUCTURE PVT. LTD.
DRAWN	B.S.	24/01/2025	PROJECT - ROLLING SHUTTER
CHECK	V.M.	24/01/2025	FORMAT NO - NIHVA-DD-F-03
APPROVAL	V.T.	24/01/2025	DWG. NO. : NIHVA/24-25/SMP/250124 REV-00
			SCALE: NTS WT: SHEET: 01 OF 01
ALL DIMENSION ARE IN mm			If any queries contact : design@nihva.com