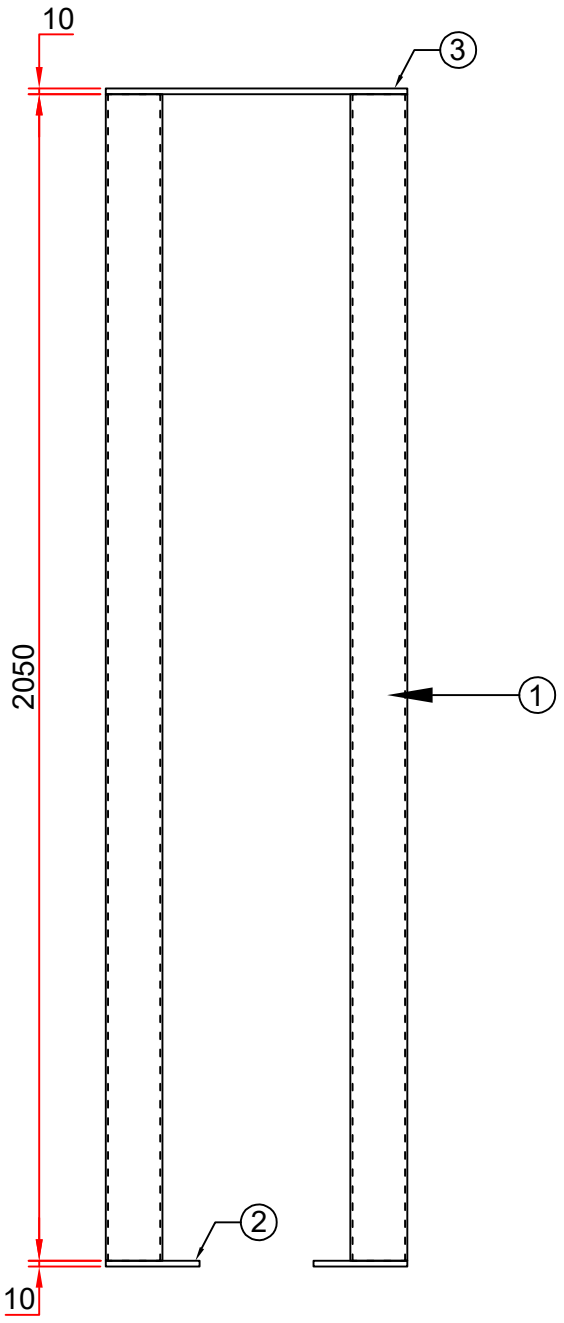
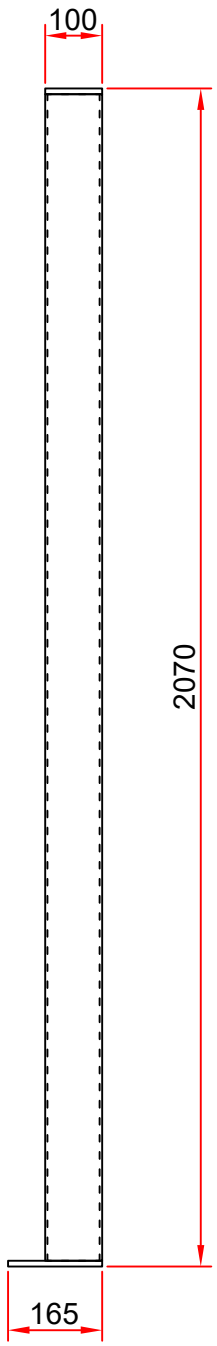



| BOM FOR POST | | | |
|---|---|---|---|
| SL NO. | DESCRIPTION | SPECIFICATION | QTY |
| 1 | MS SQ. TUBE | 100X100X4X2050L | 2NOS |
| 2 | POST SUPPORT PLATE | 165X165X10THK | 2NOS |
| 3 | ROLLER SUPPORT PLATE | 530X100X10THK | 1NO |

| Rev No. | Revision | Date | Revised By |
|---|---|---|---|
| | | | |

This drawing & design is the property of NIHVA TECHNOLOGIES. Not to be sold or copied to any other concern.

TITLE:- POST

| | NAME | DATE | SIGN |
|---|---|---|---|
| DRAWN | SUJATA | 20/07/2022 | |
| CHECK | M.S | 20/07/2022 | |
| APPRD. | A.K | 20/07/2022 | |

If any queries contact : design@nihva.com

ALL DIMENSION ARE IN mm

NIHVA TECHNOLOGIES PVT. LTD.
NIHVA TECHNOLOGIES PVT. LTD, PUNE
Tel : 020 66304033
Email:- info@nihva.com
Website:- www.nihva.com

CLIENT - OC Specialities

LOCATION - Solapur

PRODUCT - End Post 2 | QTY:-1 NO

DWG NO:-NIHVA/22-23/MFG/0041 | REV- 0

SCALE: NTS | SCALE:-- 1:1 | SHEET: 01 OF 01