
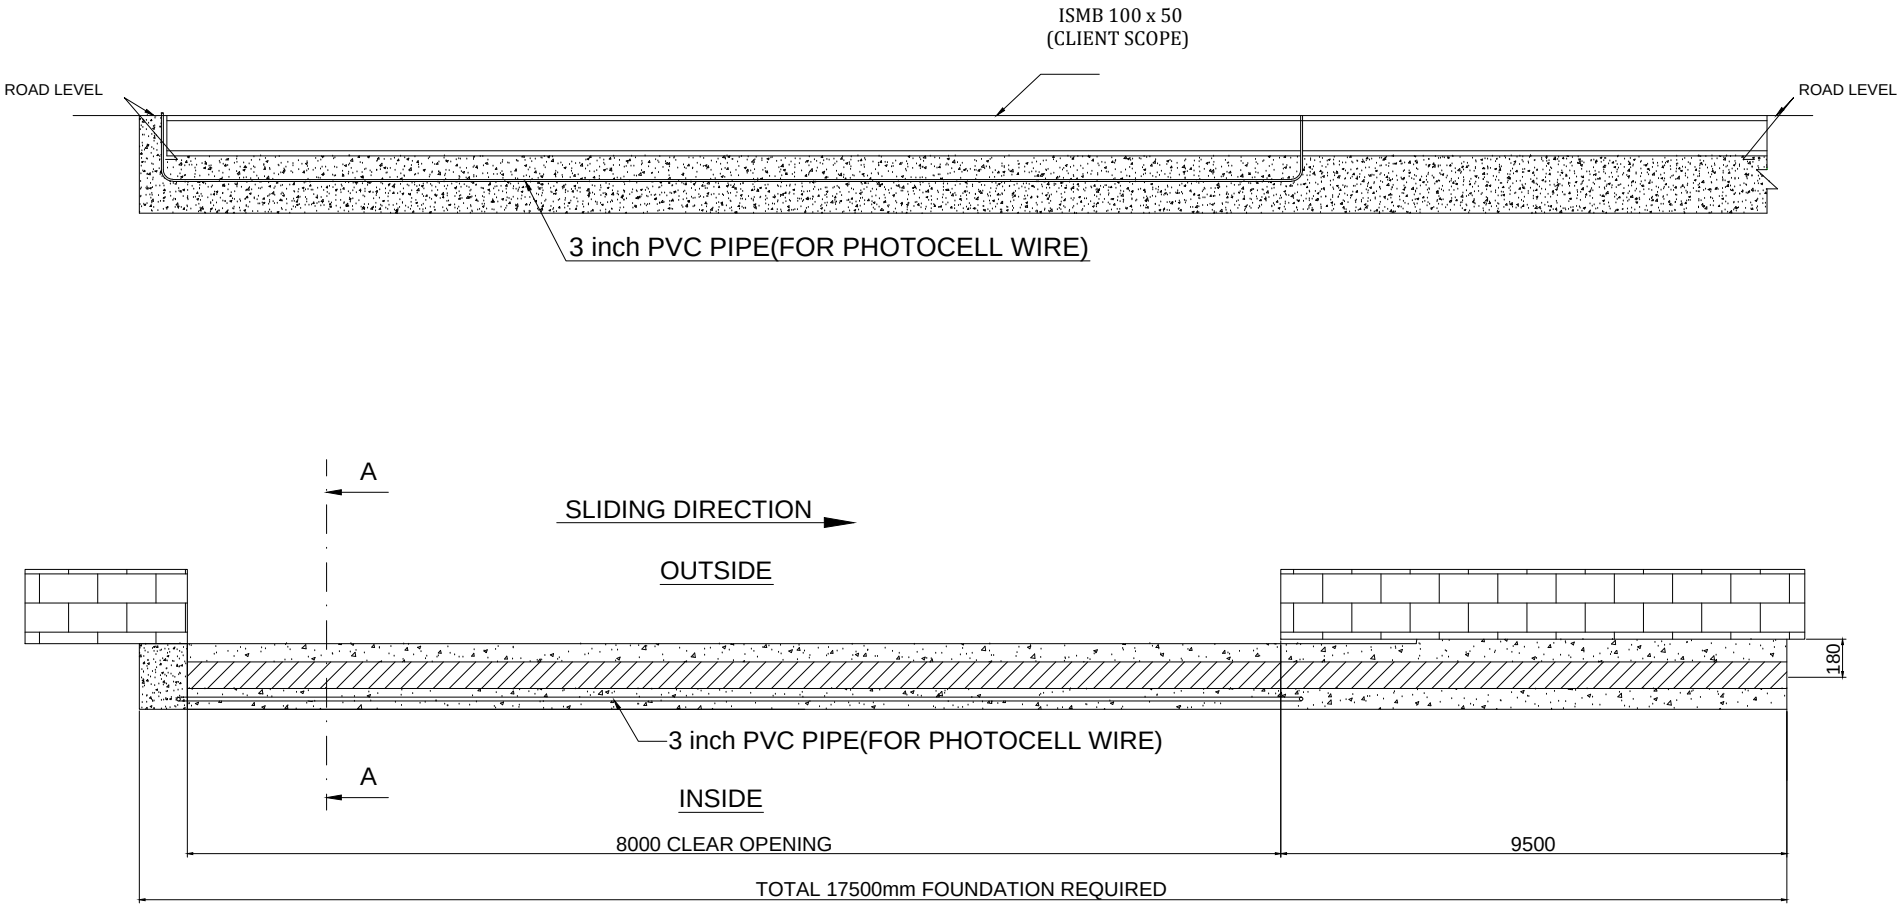


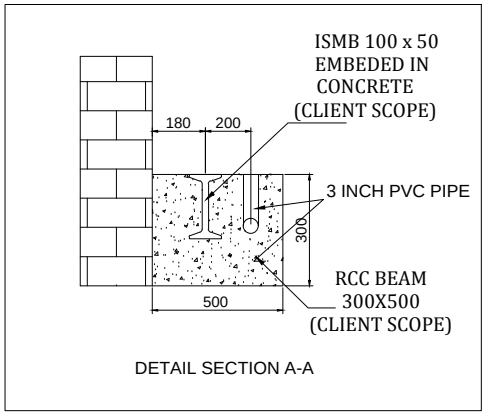

DETAIL SECTION A-A

This drawing & designing is the property of NIHVA TECHNOLOGIES. Not to be sold or copied to any other concern.

TITLE: SLIDING GATE FOUNDATION DRAWING			
	Name	SIGN	DATE
DRAWN	P.A		31.01.20
CHECK	G.J		31.01.20
APPROVAL			
If any queries contact : design@nihva.com			
ALL DIMENSION ARE IN mm			

NIHVA TECHNOLOGIES PVT. LTD.
NIHVA TECHNOLOGIES PVT. LTD. PUNE
Tel : 020 66304033
Website:- www.nihva.com
Email:- info@nihva.com

CLIENT - DESAI CONSTRUCTION			
PROJECT -			
SITE LOCATION - GUJARAT			
DWG. NO. : NIHVA/19-20/0203			REV.:- 0
SCALE: NTS	WT:		SHEET: 01 OF 01