




01a MEZZANINE PLAN (+05.250)
SCALE 1:150

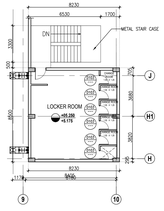

01b MEZZANINE PLAN (+05.250)
SCALE 1:150

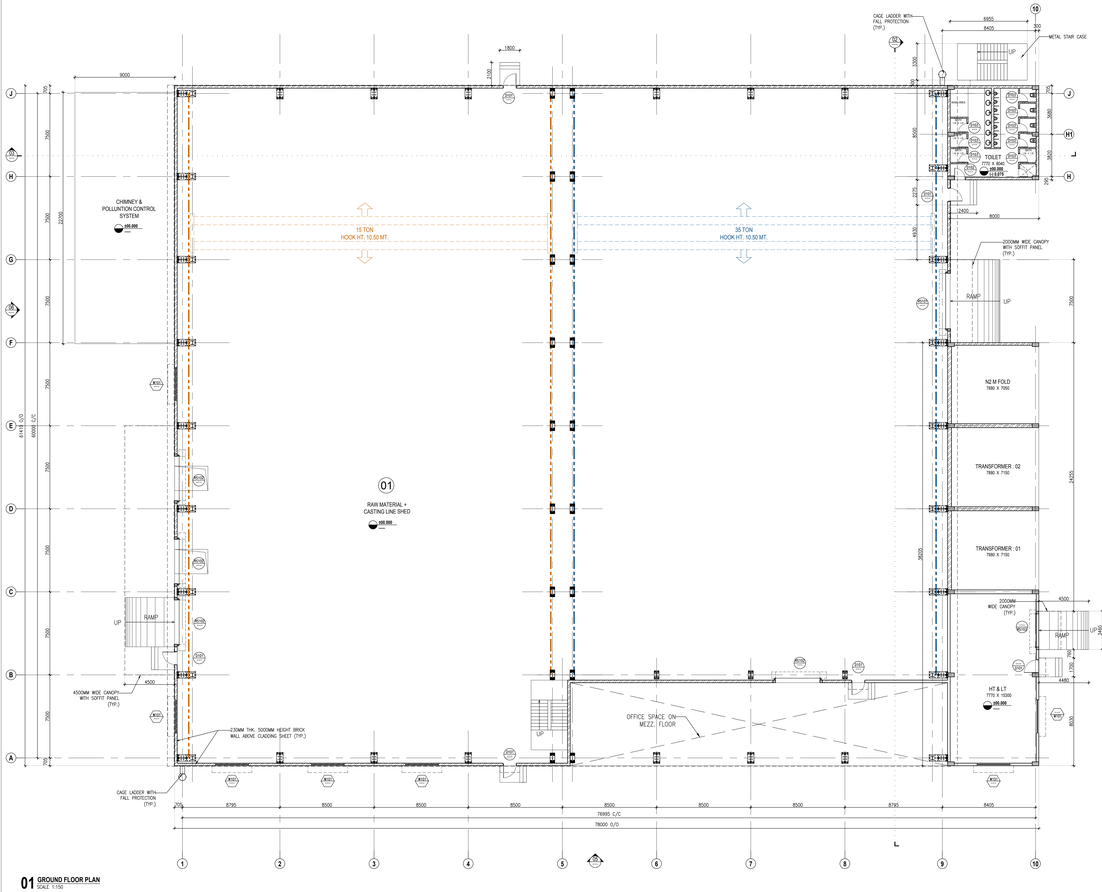

01 GROUND FLOOR PLAN
SCALE 1:150

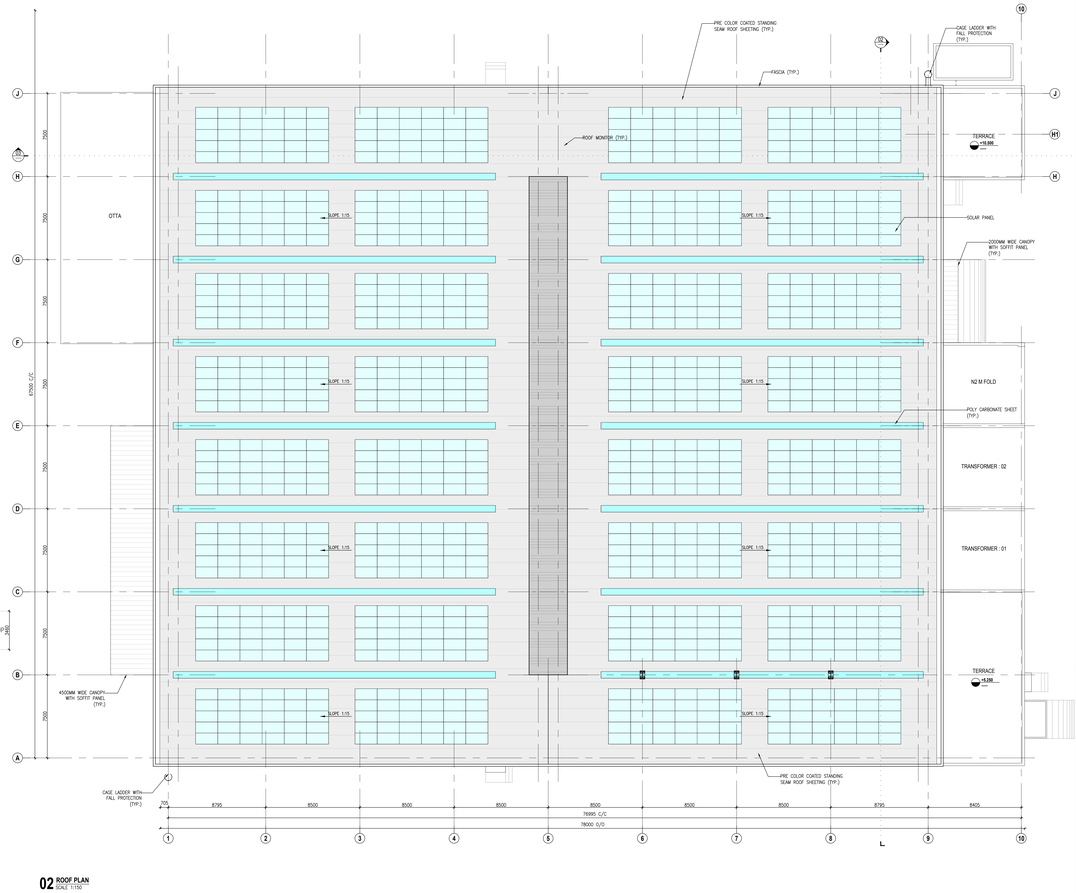

02 ROOF PLAN
SCALE 1:150

THIS DRAWING & DESIGN IS THE SOLE PROPERTY OF VMS & SHALL NOT BE COPIED, TRACED OR REPRODUCED BY ANY MEANS WITHOUT PRIOR WRITTEN CONSENT OF THE FIRM.

GENERAL NOTES :

1. ALL THE DIMENSIONS ARE UNFINISHED DIMENSIONS.
2. ALL DIMENSIONS ARE IN MILLIMETRES OF UNLESS OTHERWISE MENTIONED.
3. ALL THE DIMENSIONS SHALL BE READ & NOT TO BE MEASURED.
4. IN CASE OF ANY DISCREPANCY, BRING IT TO THE NOTICE OF THE ARCHITECT IMMEDIATELY.
5. DETAIL DRAWING PRECEDES THE GENERAL DRAWING.

STANDARD DRAWING SYMBOLS:

- FINISHED LEVEL / UNFINISHED LEVEL
- SECTION SYMBOL, UPPER HALF INDICATES DIAGRAM NO. IN DRAWING SHEET & LOWER HALF INDICATES DRAWING NO.
- ELEVATION SYMBOL, UPPER HALF INDICATES DIAGRAM NO. IN DRAWING SHEET & LOWER HALF INDICATES DRAWING NO.
- WINDOW SYMBOL, UPPER HALF INDICATES WINDOW NO. & LOWER HALF INDICATES DRAWING NO.
- DOOR SYMBOL, UPPER HALF INDICATES DOOR NO. & LOWER HALF INDICATES DRAWING NO.

GRAPHIC LEGEND :

- MASONRY CUT IN PLAN/SECTION.
- RCC COLUMN CUT IN PLAN.

SCHEDULE OF OPENINGS:


MK.D.	SIZE	SILL HT.	LINTEL HT.	TOTAL NO.	REMARKS
RS101	5000x4000	-----	----	1	ROLLING SHUTTER
RS102	4000x4000	-----	----	4	ROLLING SHUTTER
RS103	3000x4000	-----	----	1	ROLLING SHUTTER
D101	1200x2400	-----	2400	6	FIRE DOOR
D102	1000x2400	-----	2400	2	--
D103	800x2400	-----	2400	14	--
W101	3000x1500	900	2400	8	------

FOR TENDER

NO.	DATE	DESCRIPTION	DRAWN BY	CHECKED BY

REVISION HISTORY

KEY PLAN
SCALE : N.T.S.

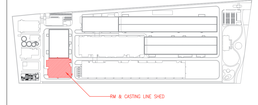

REFERENCE DRAWINGS :

01. ARCHITECTURAL :	-
02. STRUCTURAL :	-
03. HVAC :	-
04. ELECTRICAL :	-
05. UTILITIES :	-

FLOOR PLAN

RM & CASTING LINE SHED

AGRAWAL METAL WORKS(P) LTD.

PROJECT NO.	SCALE :	DRAWN :	ASHISH C.
3824	1:150	CHECKED:	BHAKTI B.
	DATE : 03-12-2024	APPROVED:	DARSH D.
		COORDINATION CHECKED	DARSH D.

VMS ENGINEERING & DESIGN SERVICES (P) LTD.
CHITRAKOOT FLATS, B/H TIMES OF INDIA, OFF ASHRAM ROAD,
AHMEDABAD-380 009. PHONE: +91 (079) 2658-6826, 4023-6208
WWW.VMSCONSULTANTS.COM

SHEET SIZE	DRAWING NO.	TENDER	REVISION
841x 1500	T.A.1.101	T	R0