
DWG.NO: SALT_1714_STR_01_R1

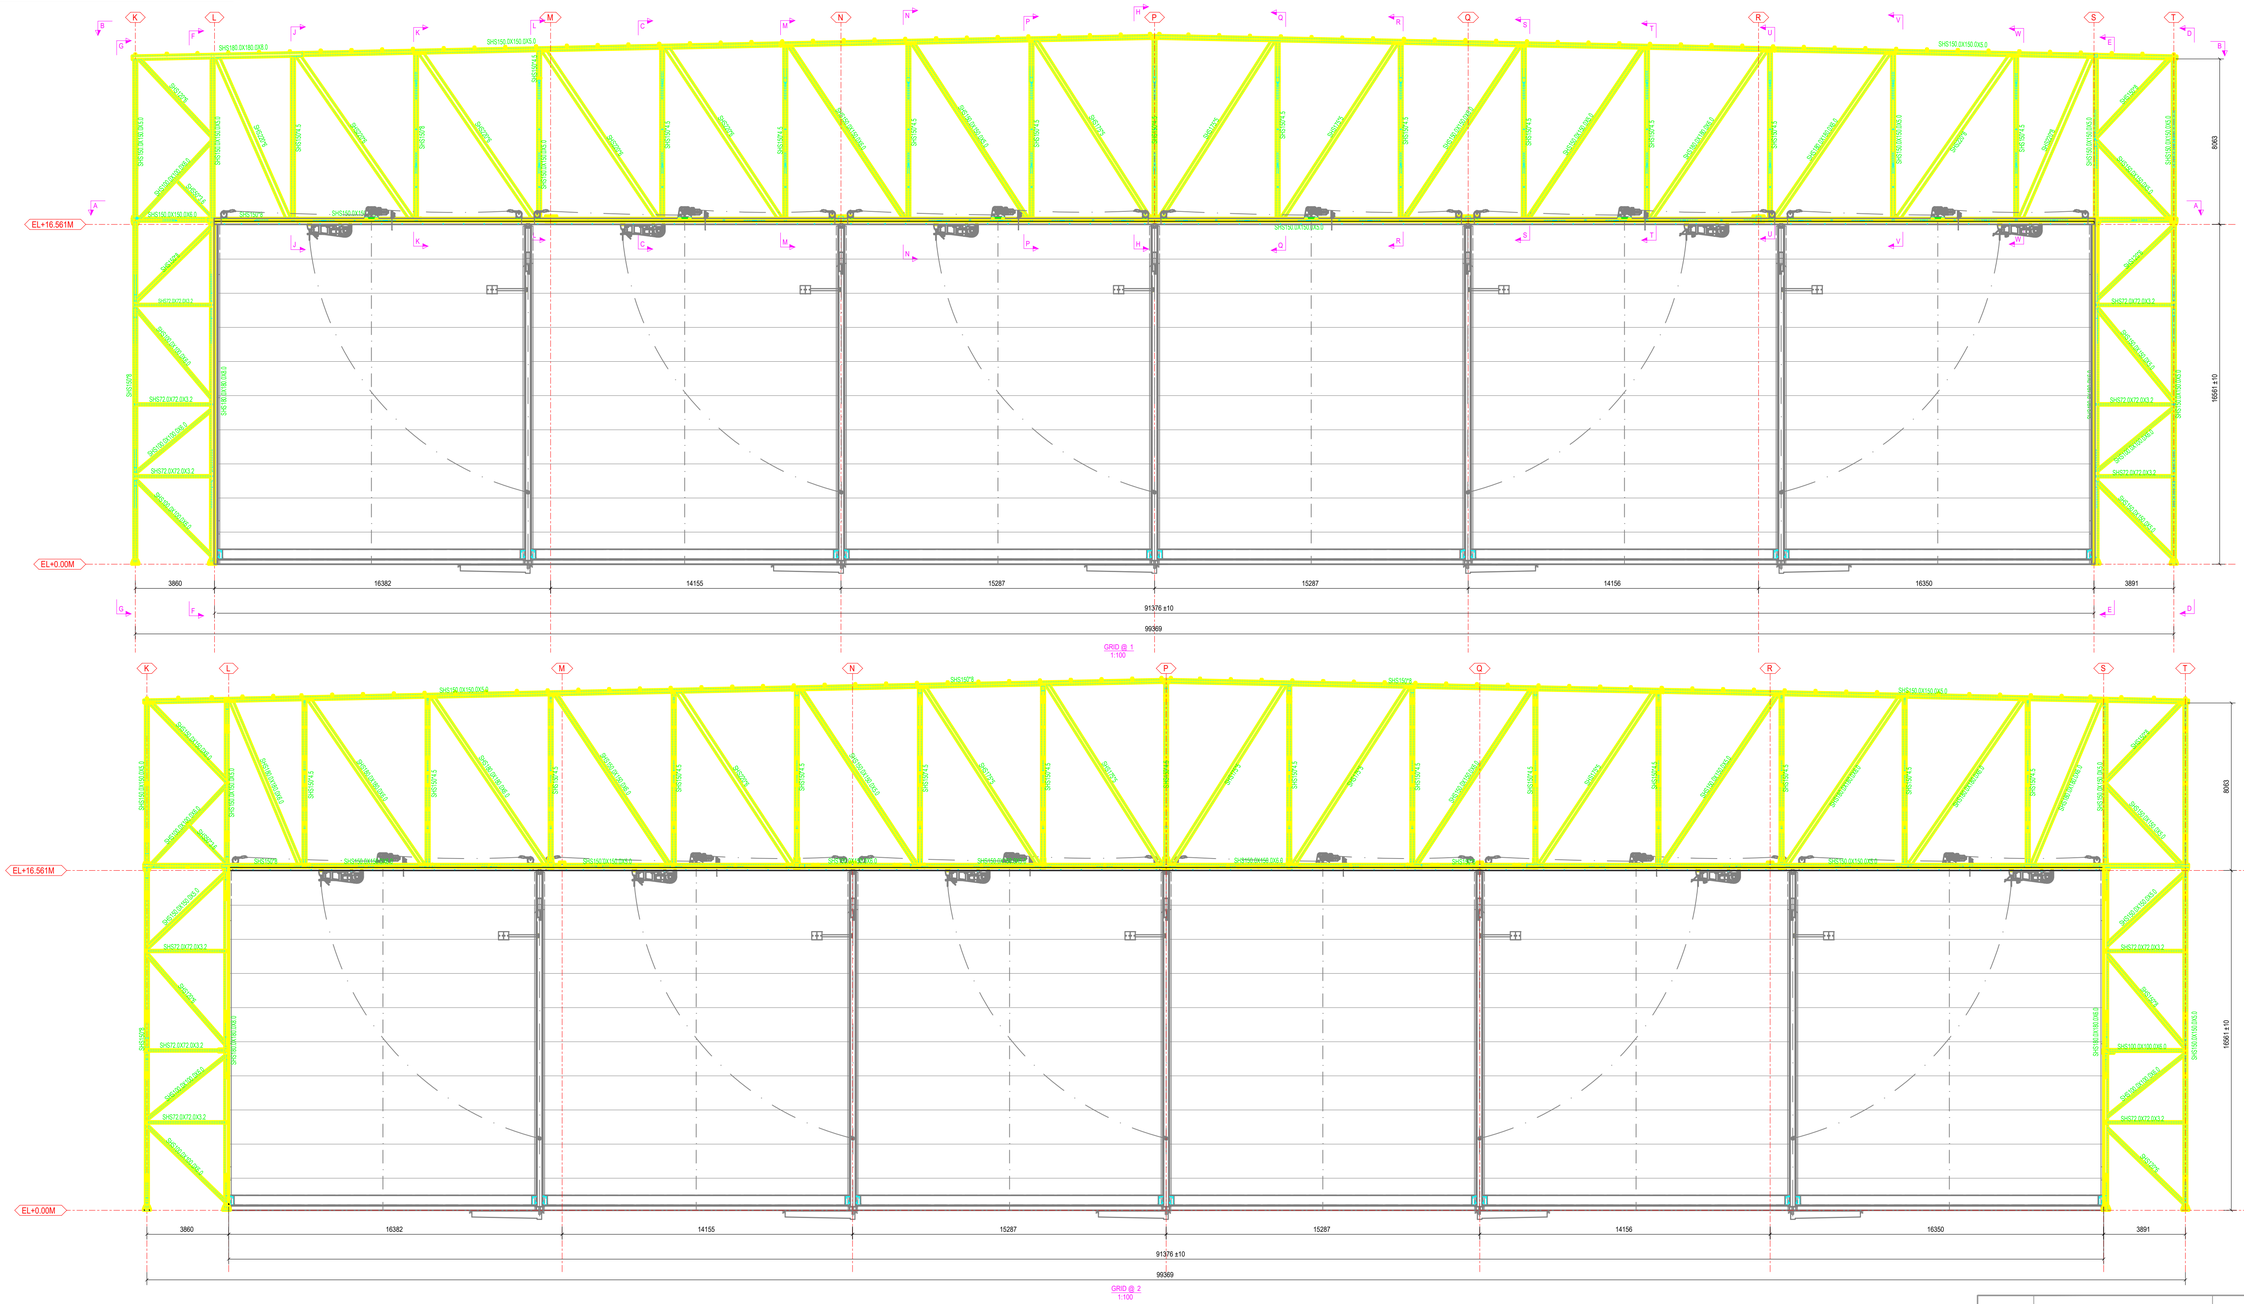


| REV.NO. | DESCRIPTION. | REV.DATE | DRAWN. | CHKD. | APPD. |
|---|---|---|---|---|---|
| 0 | GA DRAWING FOR APPROVAL | 05.11.22 | MEGHA | HAB | HAB |

DWG.TITLE :- GA DRAWING FOR DOOR FRAME (99M)

| | |
|---|---|
| PROJECT | MEGADOOR INSTALLATION AT HYDRABAD AIRPORT |
| CLIENT | GMR |


SALT Design Services
NIHVA NIHVA TECHNOLOGIES PVT. LTD.

SALT DESIGN SERVICES NIHVA TECHNOLOGIES PVT. LTD. PUNE
Tel : 020 66304033
Email:- info@nihva.com
Website:- www.nihva.com


| | | |
|---|---|---|
| DRAWN :RRK | CHECKED : HAB | SCALE: 1:100 |
| APPROVED : HAB | JOB CODE. : 1729 | DATE: 05.11.2022 |
| DWG.NO: SALT_1729_GA_01_R0 | (SH-1OF2) | REV. - R0<br>SIZE. - A0 |

A1 [841 x 594]