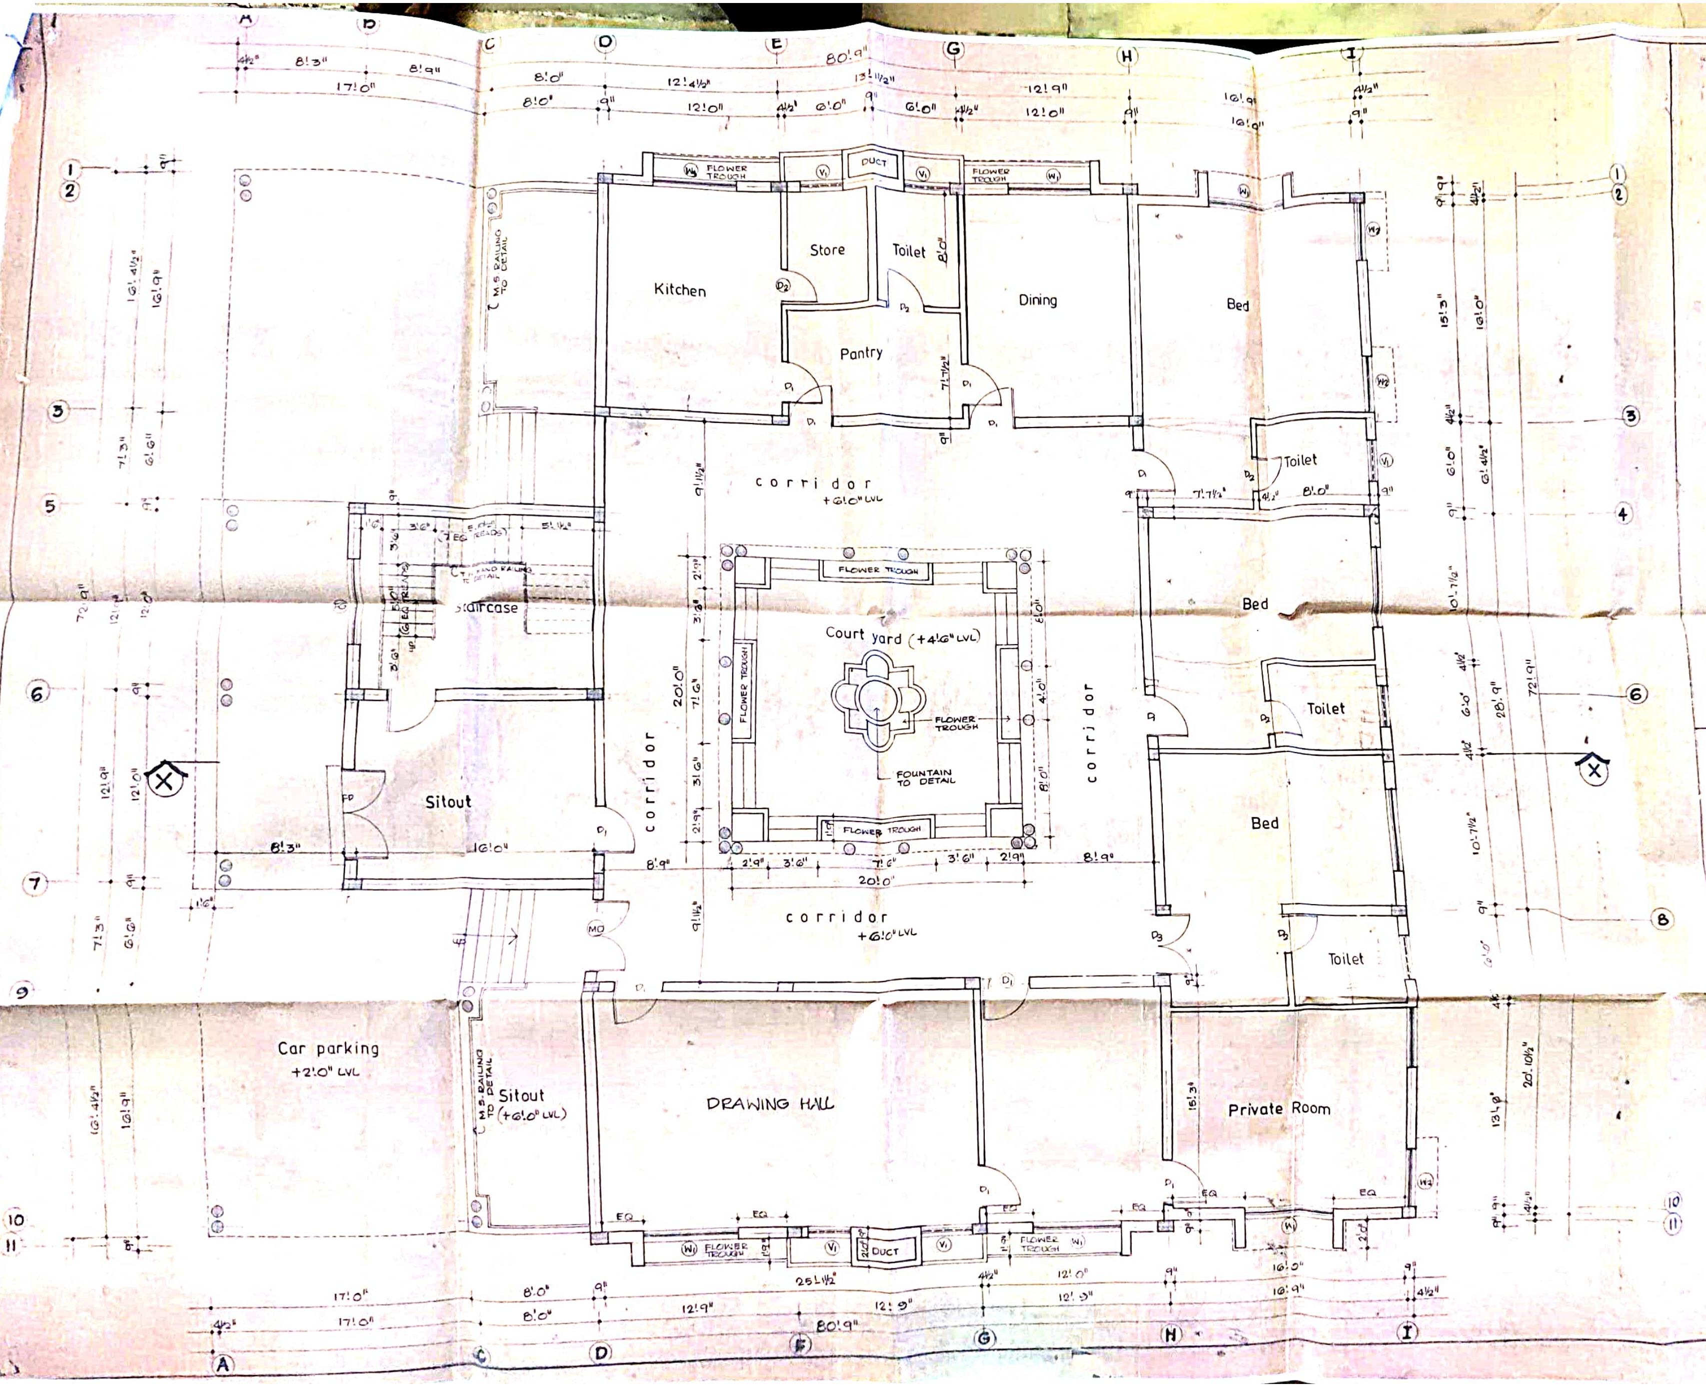

Ground floor

32/99

K. VIVEKANANDAN, D.C.E.
Consulting Engineer &
Licensed Surveyor
SARATHA CONSTRUCTIONS
67, Perumal Kovil St.
Near Bharathan Theatre
TENKASI - 627 811.

PROPOSED GUEST HOUSE AT CUTTRALAM.

GROUND FLOOR PLAN

Scale 1"=4'0"	Date 26.4.99	Job No 219/99
Sheet No 1	Drawn	Chkd by

Per MOHAN BREWERIES & DISTILLERIES LTD.
M. Nandagopal
M. NANDAGOPAL
Managing Director

Architects

VISTHA
No.1, Munirathnam street,
Aminjikarai,
Chennai - 29
Ph : 4834200

PLAN SHOWING PROPOSED CONSTRUCTION OF WATCH MAN QUARTERS IN RS NO 1133 AT FIVE FALLS ROAD IN COURTALLAM TOWNPANCHAYAT

OWNER. Sree. NANDAGOPAL

SITE AREA		
PLINTH AREA	731.0 SFT	67.93 M^2
CARPET AREA	602.3 "	55.98 "

DOOR	3'6" x 7'0"
DOOR	3'0" x 7'0"
DOOR	2'6" x 7'0"
WINDOW	4'0" x 4'6"
WINDOW	3'0" x 4'6"
JOLLY	2'0" x 2'0"

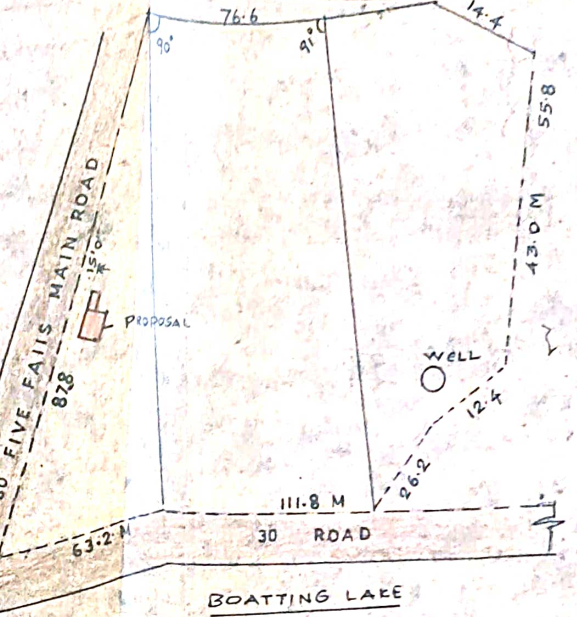

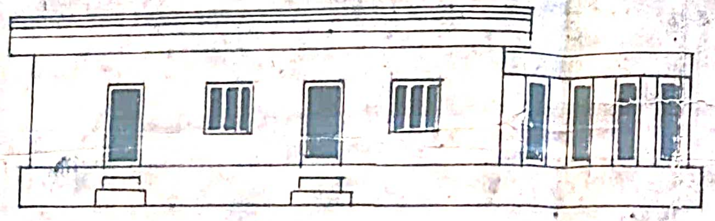

ELEVATION

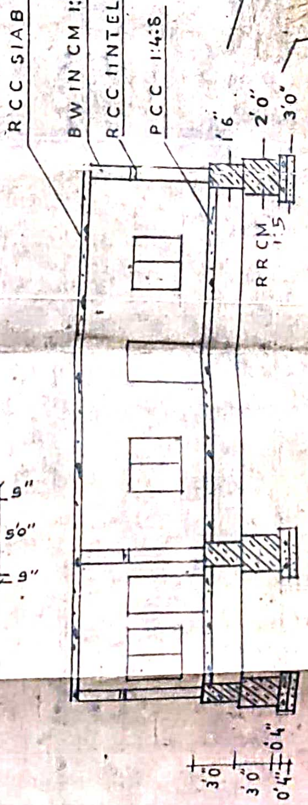

CROSSECTION ON "AB"

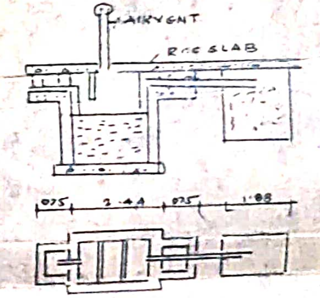

▨ ROAD

▨ PROPOSAL

▨ BOUNDARY

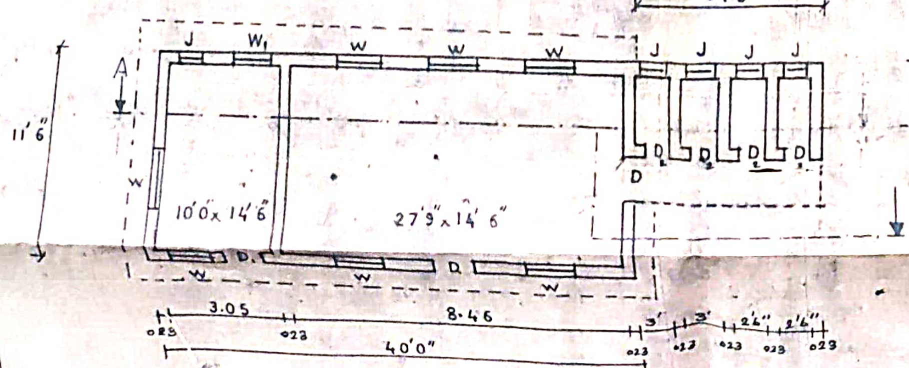

PLAN

அனுமதி வழங்கப்பட்டது
ந.க. எண் 38/99-2000
நாள் 2.9.99
நிர்வாக அதிகாரி
பேரூராட்சி குற்றாலம்

OWNER

VISTHA

CHENNAI 29
PHONE 4834200

K. VIVEKANANDAN, B.E.,
Consulting Engineer &
Licensed Surveyor
SARATHA CONSTRUCTIONS,
6/1, Perumal Kovil St.
Near Bharathan Theatre,
TENKASI - 627 811.

SURVEYOR

ARCHITECTS

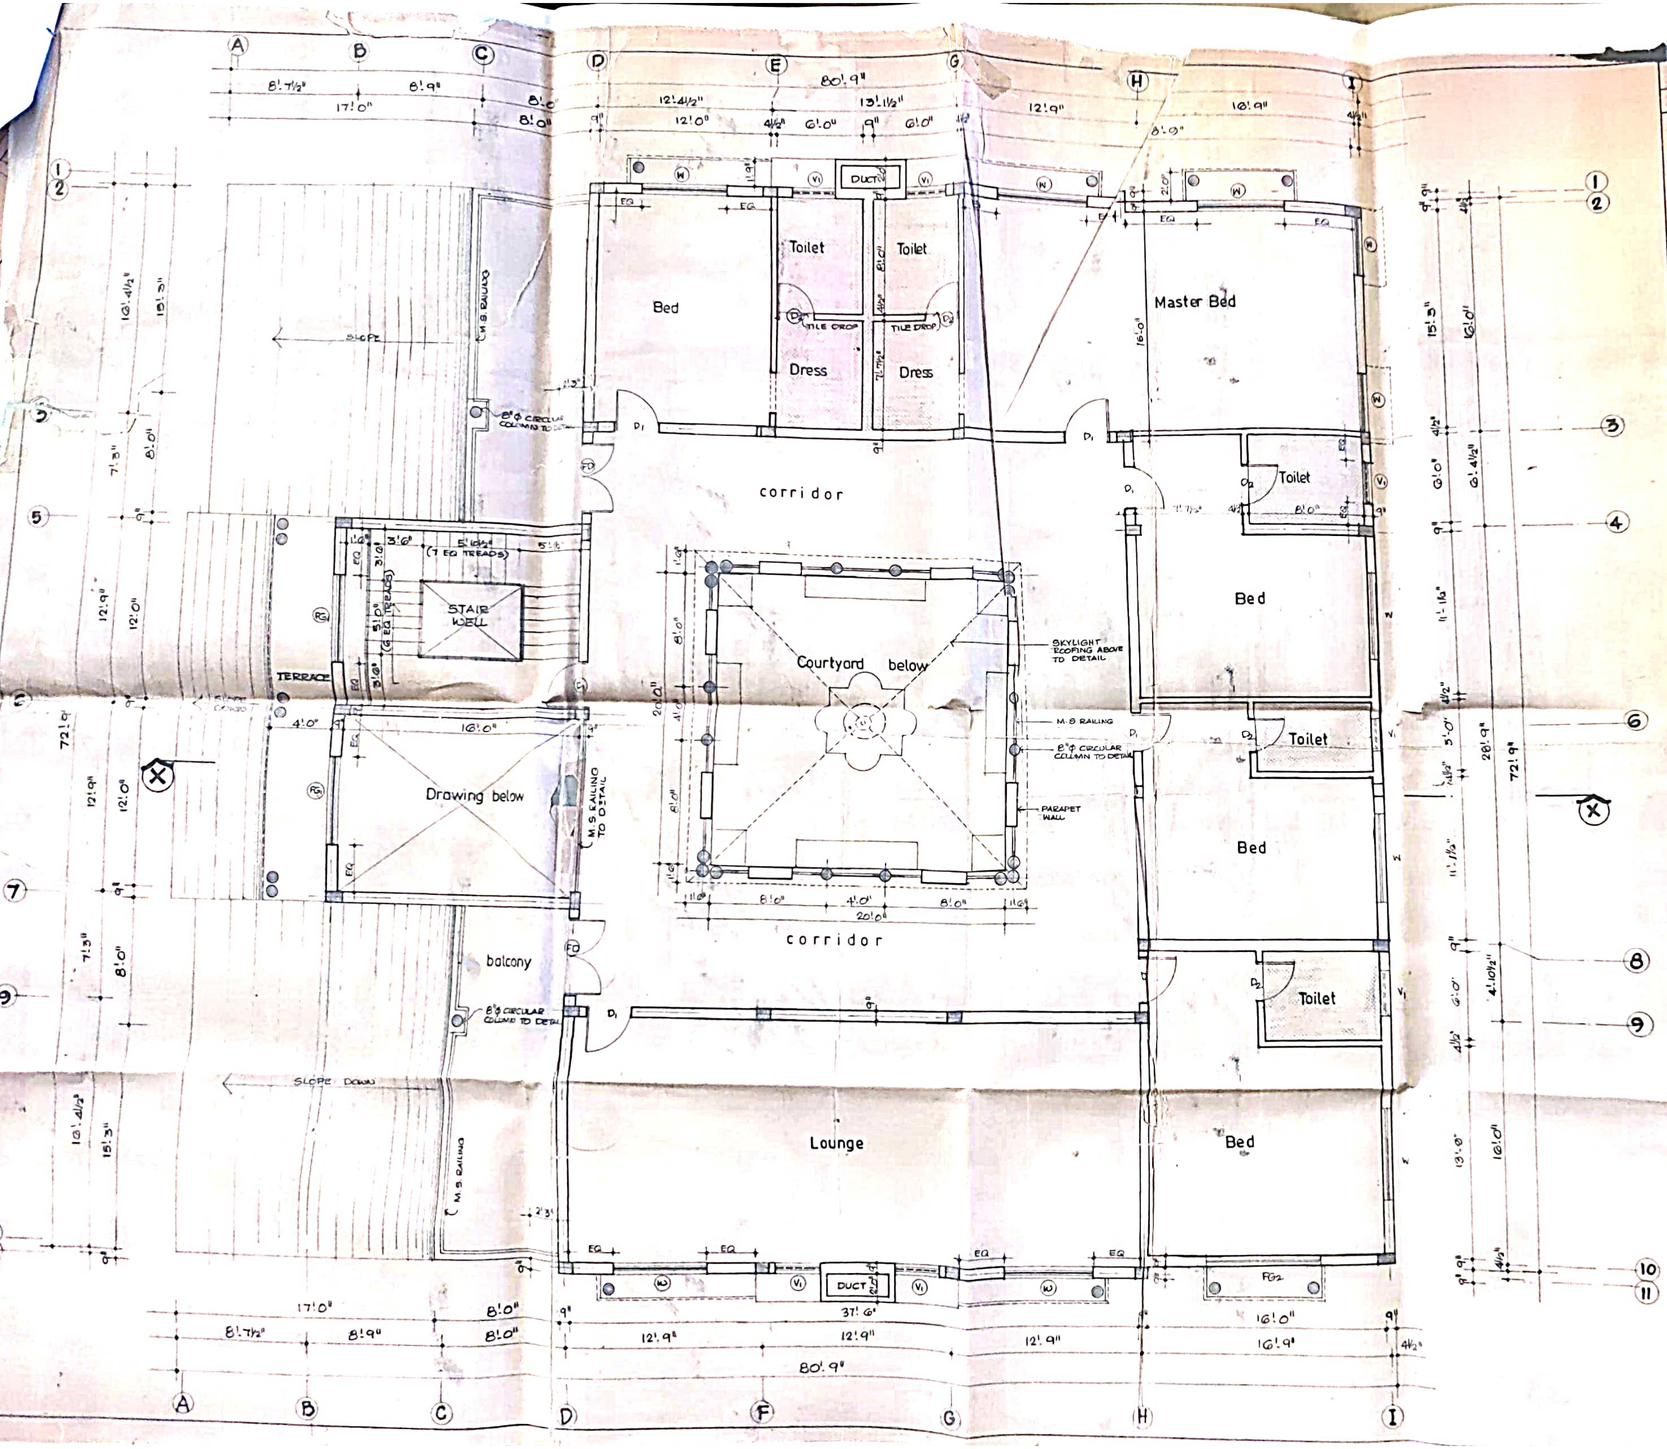

SCHEDULE OF

TYPE	DESCRIPTION	SIZE
MD	MAIN DOOR	5'.0" x 7'.0"
D_1	DOOR	3'.3" x 7'.0"
D	DOOR	3'.0" x 7'.0"
D_2	DOOR	2'.6" x 7'.0"
FD	FRENCH DOOR	6'.0" x 7'.0"
FD_1	FRENCH DOOR	5'.0" x 7'.0"
W_1	WINDOW	6'.0" x 4'.6"
W_2	WINDOW	4'.0" x 4'.6"
W_3	KITCHEN WINDOW	6'.0" x 3'.6"
V	VENTILATOR	3'.0" x 2'.0"
FG	FIXED GLAZING	6'.0" x 6'.6"
FG_1	FIXED GLAZING TO DETAIL	
FG_2	FIXED GLAZING	6'.0" x 4'.6"
BW	BAY WINDOW	8'.0" x 4'.6"
D_3	DOOR	4'.0" x 7'.0"
AD	ARCH DOOR	6'.6" WIDE
GD	GRILL / GRILL DOOR	6'.6" WIDE

[illegible]
[illegible] 28
[illegible] 2010
[illegible]
/ /999

K. VIVEKANANDAN, B.C.E.,
Consulting Engineer &
SARADHA CONSTRUCTIONS
61, Perumal Koil St,
Near Bharathan Theatre,
TENKASI - 627 8[illegible]

PROPOSED GUEST HOUSE
AT CUTTRALAM

FIRST FLOOR PLAN.

Scale 1" = 4'.0"	Date 28.4.99	Job No 219/99
Sheet No 2	Drawn Jayanthi	Chkd by

19/20 D. Nandagopal
FOR MOHAN BREWERIES
AND DISTILLERIES LTD

Architects

VISTHA
No. 1 Munirathnam street
Aminjikarai,
Chennai 29
Ph 4834200

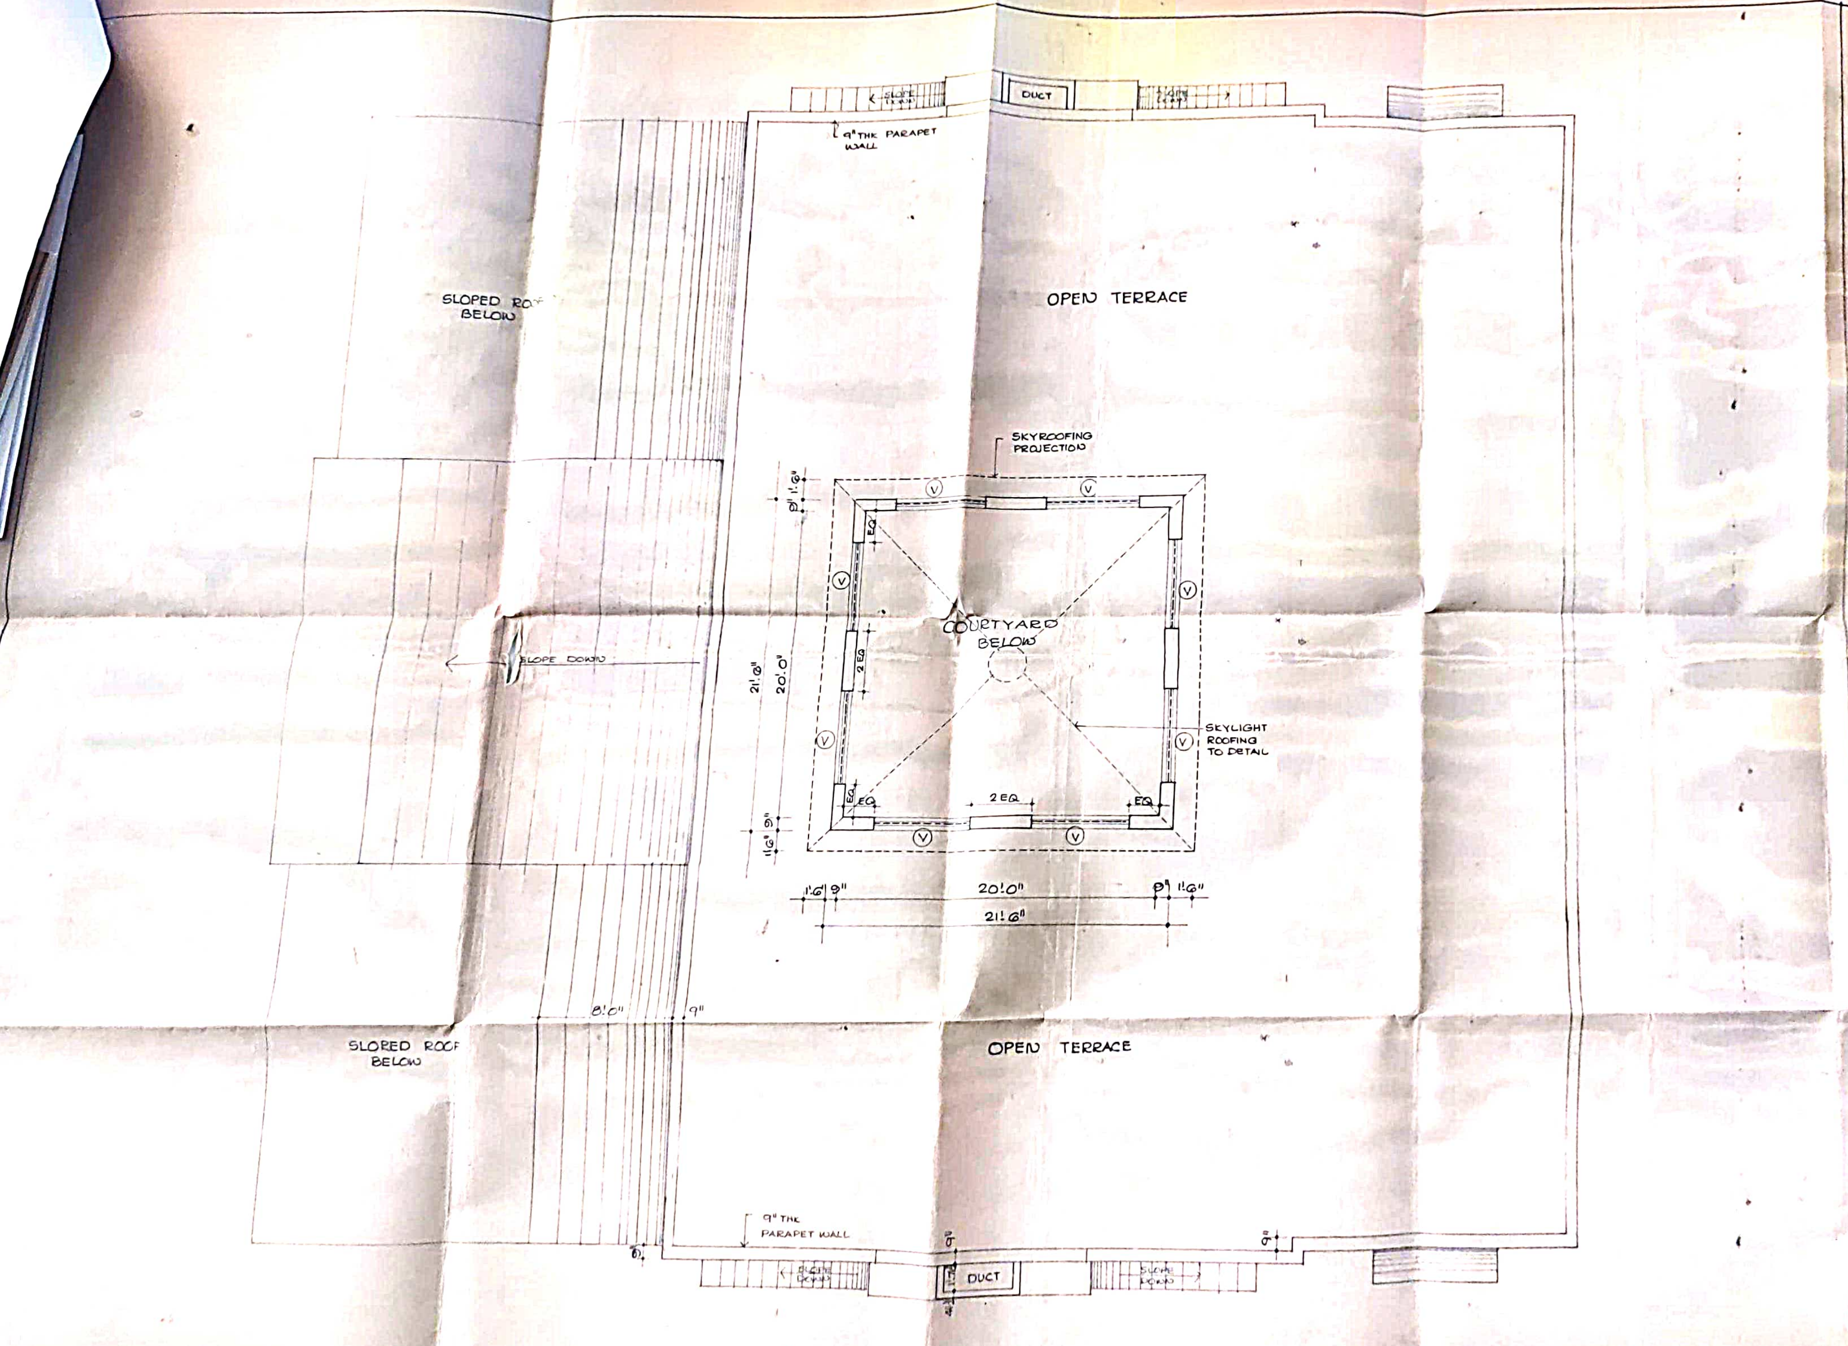

PROPOSED GUEST HOUSE
AT CUTTRALAM

TERRACE FLOOR PLAN

Scale 1"=4'.0"	Date 26.6.99	Job No 219/99
Sheet No 3	Drawn	Chkd by

For MOHAN BREWERIES & DISTILLERIES LTD.
M. Nandagopal
M. NANDAGOPAL
Managing Director

Architects

VISTHA
No. 1, Munirathnam street,
Aminjikarai,
Chennai. 29.
Ph 4834200.