

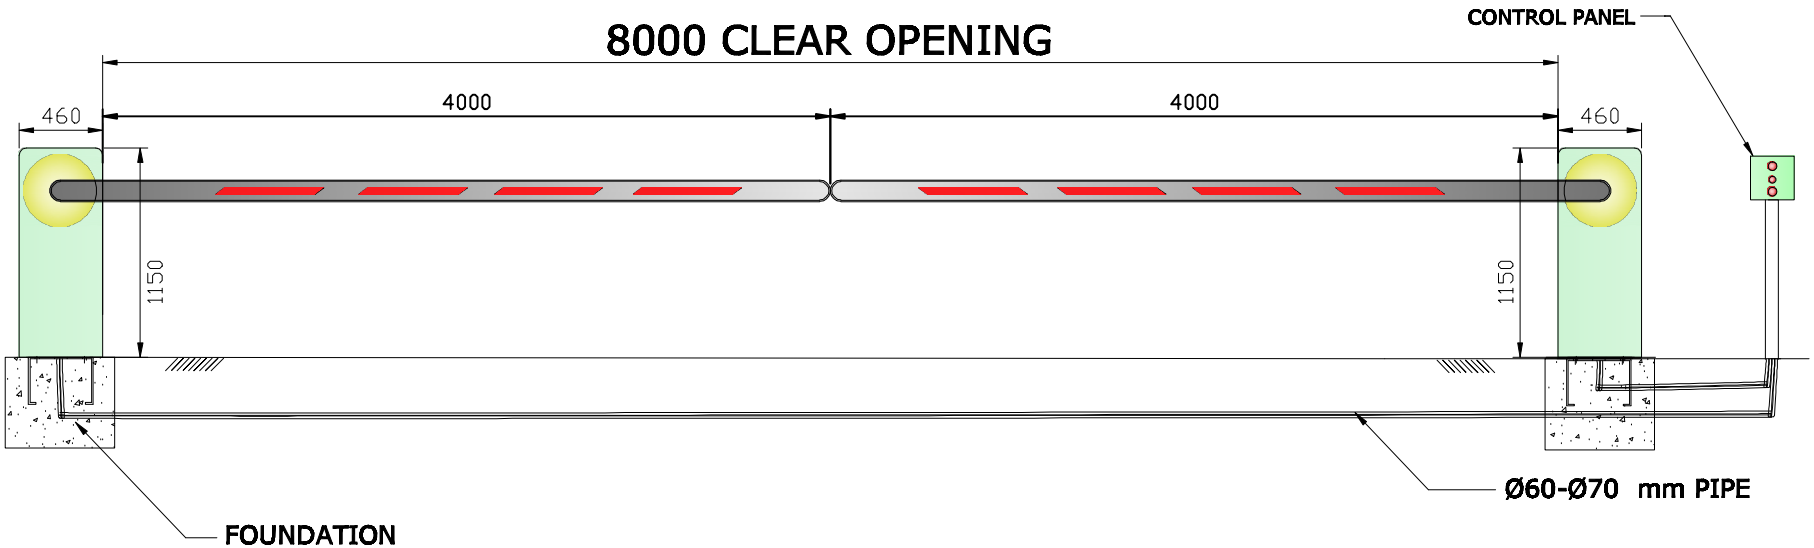


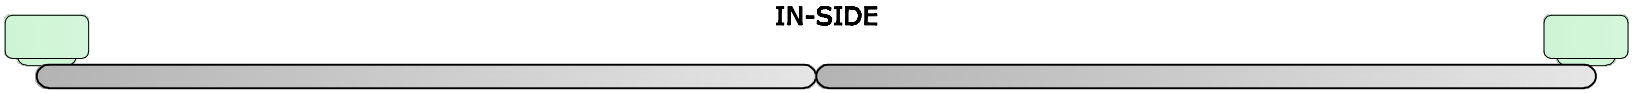

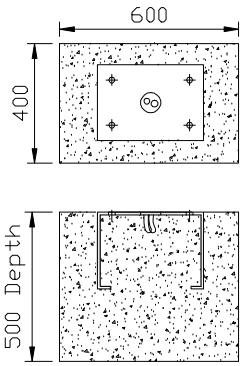

FOUNDATION DETAILS

This drawing & designing is the property of NIHVA TECHNOLOGIES. Not be sold or copy to any other concern.

TITLE

BOOM BARRIER FOUNDATION DETAILS

CLIENT APPROVAL

ALL DIMENSION ARE IN mm

	SIGN	DATE
DRAWN	ABHIJIT	28/11/14
CHECK	ANIL	28/11/14
ENG		
APPRD.		
MFG		
Ref. No.		

NIHVA TECHNOLOGIES PVT. LTD.

NIHVA TECHNOLOGY PVT. LTD. PUNE
Tel : 020 66304033
Email:- info@nihva.com
Website:- www.nihva.com

CLIENT -Valeo India Pvt Ltd

PROJECT-Valeo Thermal System,Sanand

SITE -Sanand, Gujrat

DWG. NO. - NVA/valeo/BRR/01

SCALE:01 | WT: | SHEET:01

If any queries contact : projects@nihva.com