


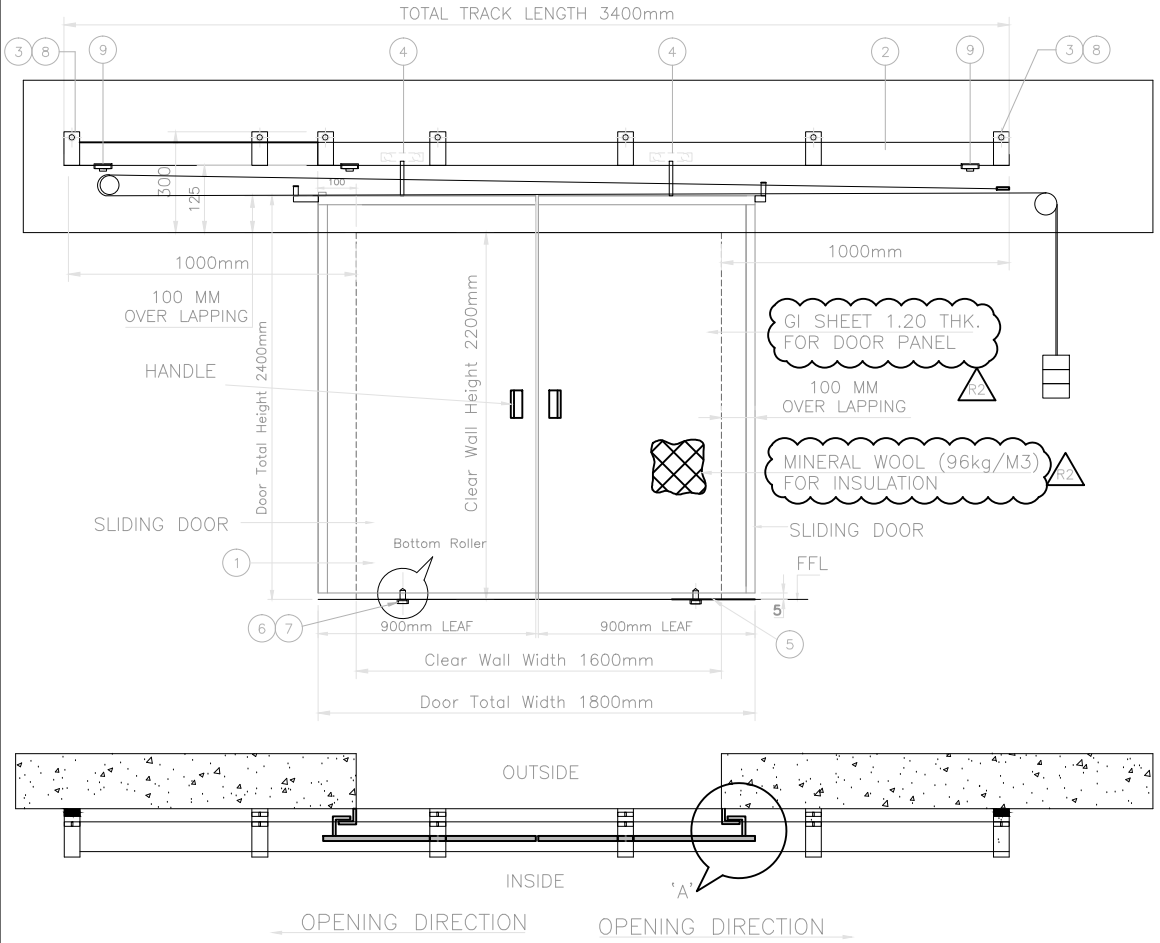


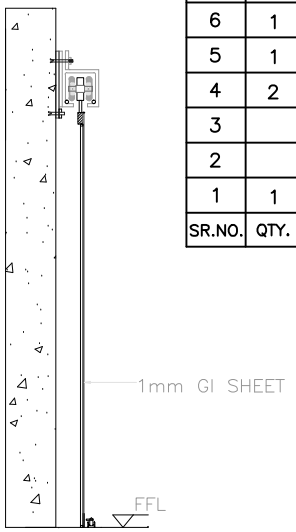


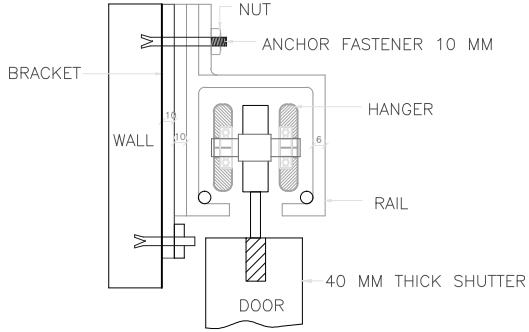

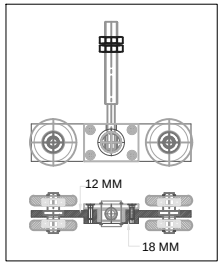


DETAIL AT 'B'

SR.NO.	QTY.	DESCRIPTION
9	1	STOPPER (FOR HANGER ASSLY.)
8	1	COVER (FOR TRACK BKT.)
7	1	BOTTOM ROLLER MTG. FLAT (BOTTOM ROLLER BKT.)
6	1	BOTTOM ROLLER ASSLY.
5	1	'Z' SECTION
4	2	HANGER ROLLER ASSLY./PANEL
3		TRACK BRACKET
2		SLIDING TRACK
1	1	SLIDING DOOR & FRAME / BACK SUPPORT SQ. TUBE

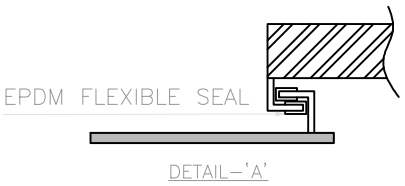

DETAIL–'A'

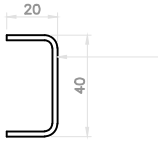

'C' SECTION USING AGAINST HOLLOW SECTION 70x40.

DETAIL–C PROFILE FOR FRAME

NOTE : DOOR OVERLAPING 100mm AT RH & LH AND TOP SIDE
ALL DIMENSIONS ARE IN MM.
CLIENT SHOULD CONFIRM DOOR OPENING DIRECTION.

TOLERANCE:- ± 10mm

Panel Make : - Radient Safe Door Make

DOOR DIMENSION		
CLEAR WIDTH	CLEAR HEIGHT	
1600mm	2200mm	01NOS

REV	DESCRIPTION	DRAWN	DATE
R03	AL DROP LOCKING ARRANGEMENT REMOVE	A.K.	05.15.2018
R02	DRG. REVISED AS PER MARK.	A.K.	29.11.2018
R01	PANEL DETAIL ADDED	A.K.	28.11.2018

This drawing & designing is the property of NIHVA TECHNOLOGIES. Not to be sold or copied to any other concern.

TITLE: AUTOMATIC SLIDING DOOR

	NAME	SIGN	DATE
DRAWN	SURAJ		21/11/18
CHECK	P.A		20/11/18
APPROVAL	R.D		20/11/18

If any queries contact : design@nihva.com

ALL DIMENSION ARE IN mm

NIHVA TECHNOLOGIES PVT. LTD. PUNE
Tel : 020 66304033
NIHVA TECHNOLOGIES PVT. LTD.
Website:- www.nihva.com
Email:- info@nihva.com

CLIENT - RATNARUP PROJECT PVT. LTD.

PROJECT -RATNARUP PROJECT PVT. LTD.

SITE - BANNER,PUNE.

DWG. NO. : NIHVA/18-19/0181/R02 | REV-02

SCALE: NTS | WT: | SHEET: 01 OF 01