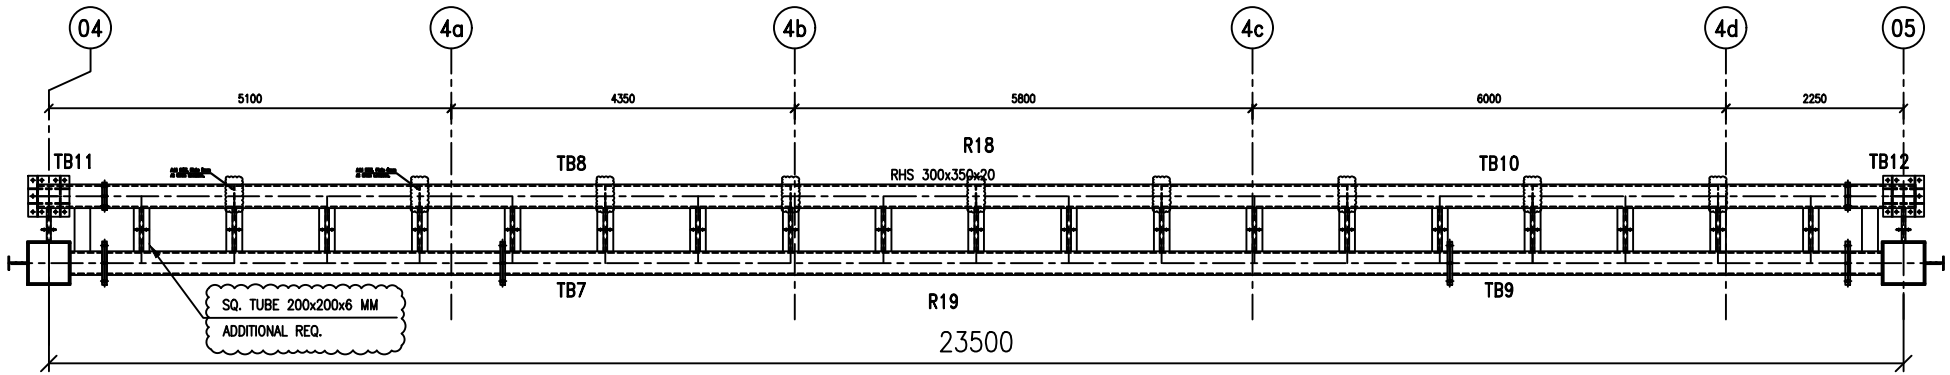
04
4a
4b
4c
4d
05
5100
4350
5800
6000
2250
TB11
TB8
R18
RHS 300x350x20
TB10
TB12
TB7
R19
TB9
SQ. TUBE 200x200x6 MM
ADDITIONAL REQ.
23500