



Tolerance ±3 mm (for all dimensions)

Dimensions in [ ] ==> clearance for installation

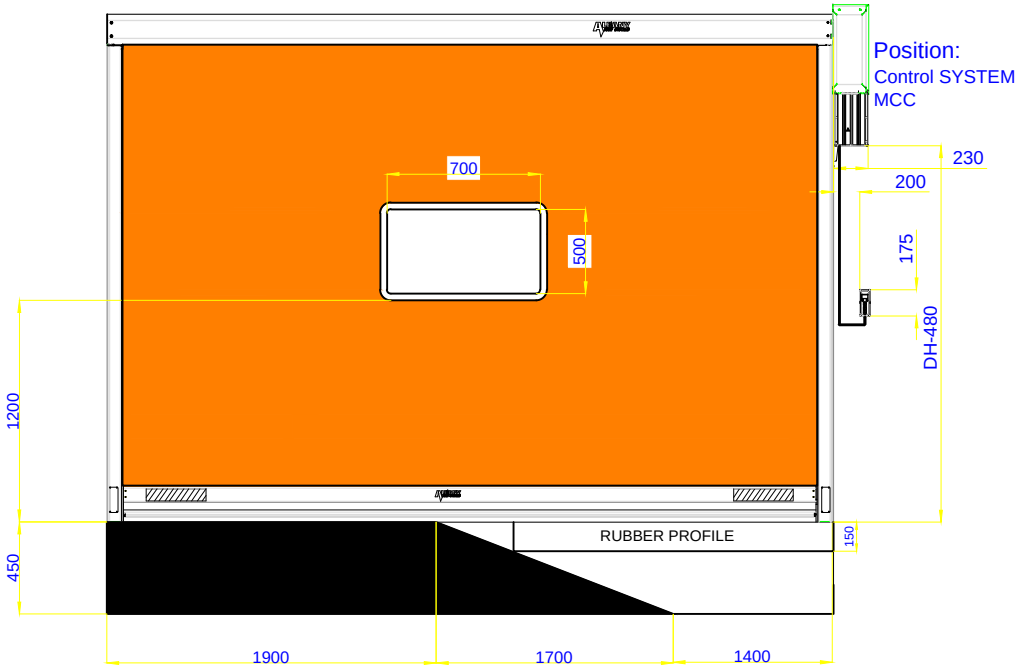

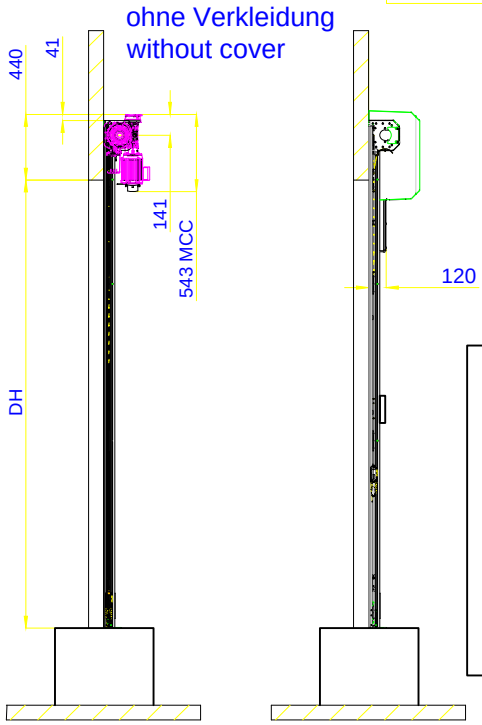

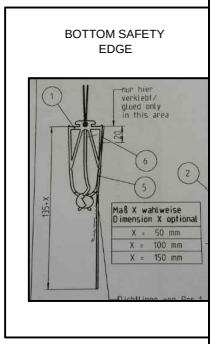

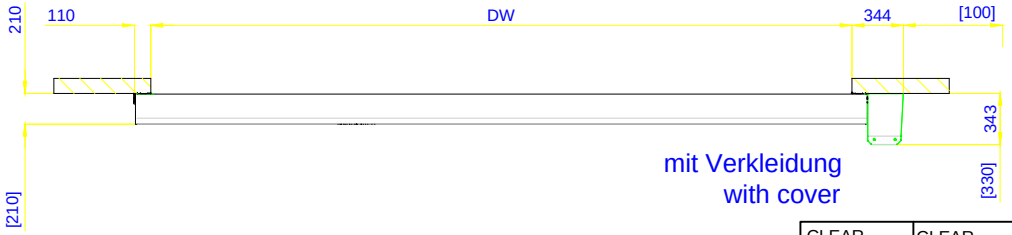

NOTE : RAL CODE - ORANGE 2009.

REV NO	REV DATE	DRAWN	REMARK
R02	05.11.2019	P.A	1. RAL CODE ADDED
R01	14.10.2019	P.A	1. WINDOW ADDED

This drawing & design is the property of NIHVA TECHNOLOGIES. Not to be sold or copied to any other concern.

TITLE: HIGH SPEED DOOR RP300 WIDE

NIHVA TECHNOLOGIES PVT. LTD. PUNE
Tel : 020 66304033
Email:- info@nihva.com
Website:- www.nihva.com

	NAME	SIGN	DATE
DRAWN	P.V.A		07.09.19
CHECK	V.M.T		07.09.19
APPV'ED			

CLIENT :- WOOSHIN

PROJECT :-

LOCATION :-

If any queries contact : design@nihva.com

DWG. NO. :- NIHVA/19-20/0094/R02 REV.:-R02

ALL DIMENSION ARE IN mm

SCALE: NTS WT: SHEET: 01 OF 01

CLEAR WIDTH(DW)	CLEAR HEIGHT(DH)	QTY
5000 MM	3000 MM	02 NOS

NOTE : ALL CIVIL & STRUCTURAL WORK WILL BE IN CLIENT SCOPE.