
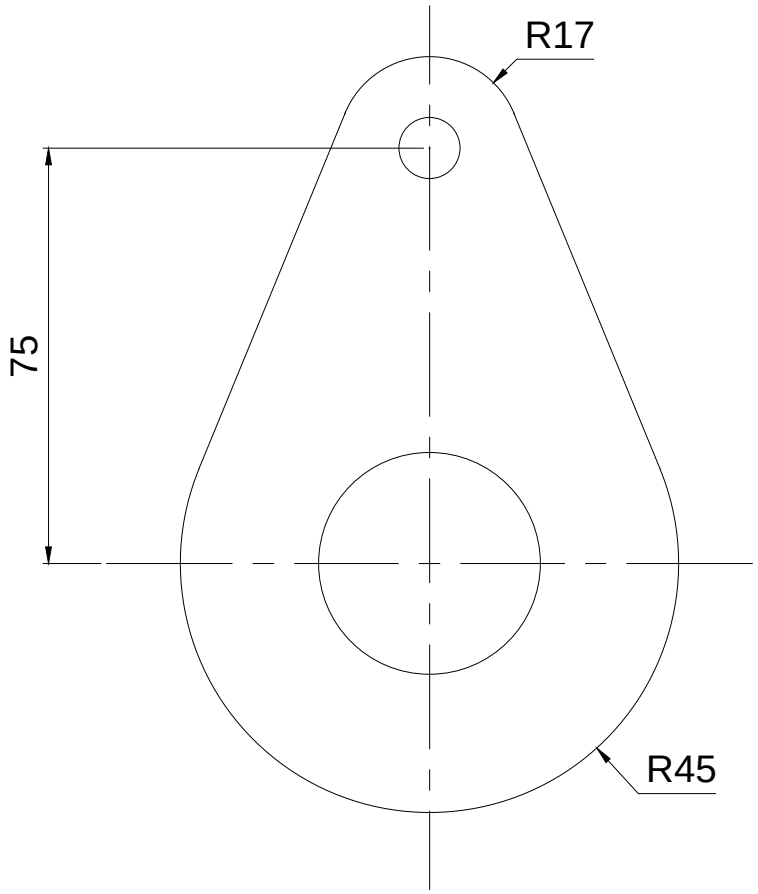


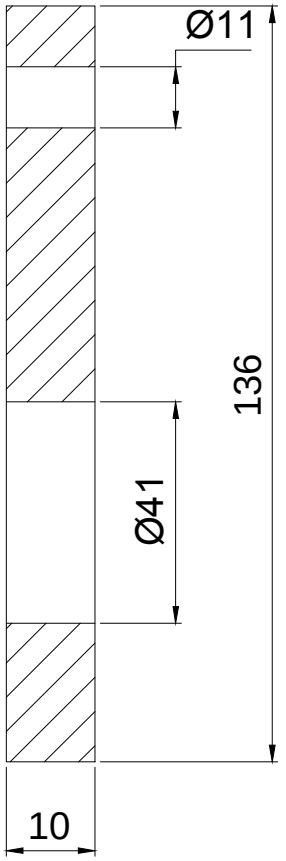

2. MS LOCK PLATE 136 X 10L = 04 NOS
M10 X 25L = 04 NOS

This drawing & design is the property of NIHVA TECHNOLOGIES. Not to be sold or copied to any other concern.

TITLE : - LOCK PLATE 02		NIHVA TECHNOLOGIES PVT. LTD. PUNE Tel : 020 66304033 Email:- info@nihva.com Website:- www.nihva.com
	SIGN	DATE
DRAWN	P.A	03.05.19
CHECK		
REV.		
APPROVAL		
If any queries contact : projects@nihva.com		
ALL DIMENSION ARE IN mm		

CLIENT -		
PROJECT -		
SITE -		
DWG. NO. : NIHVA/19-20/VDR/019		
SCALE: NTS	WT:	SHEET: 01 OF 01