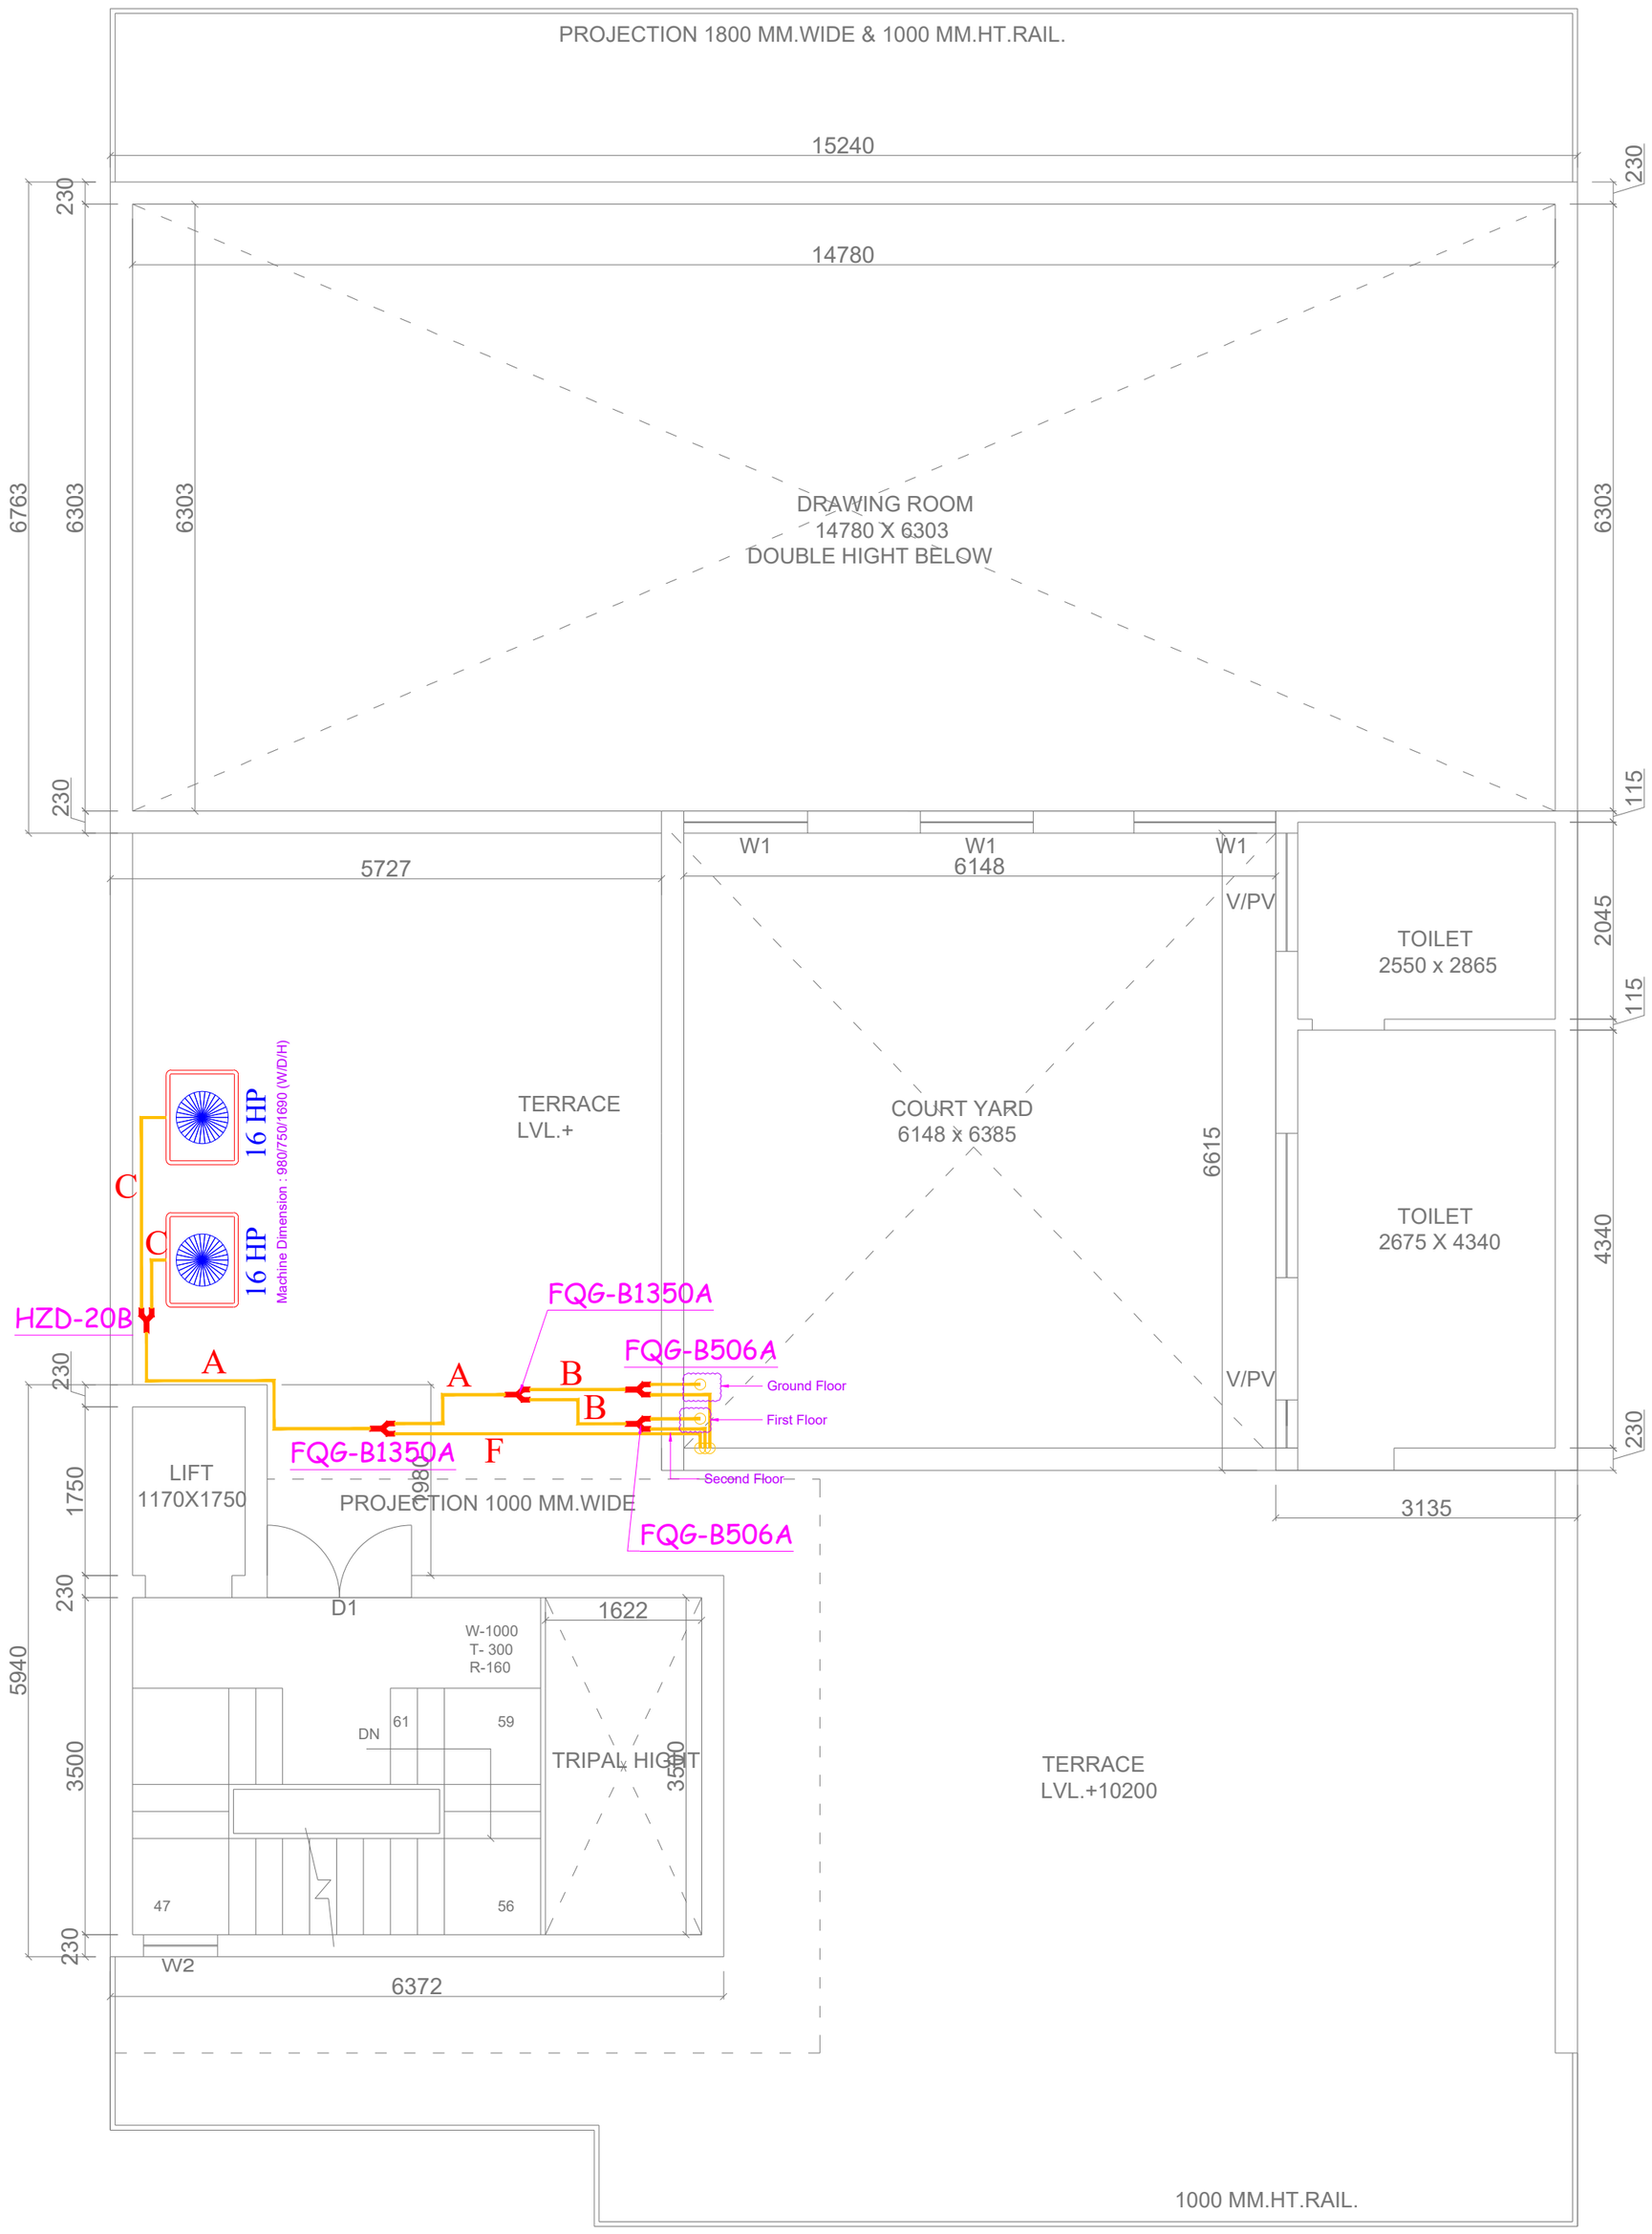


THIRD FLOOR AC PLAN

PIPE SIZES

A = 31.8 x 19.05
B = 28.58 x 15.88
C = 28.58 x 12.7
D = 22.22 x 9.52
E = 19.05 x 9.52
F = 15.88 x 9.52
G = 12.7 x 6.35

Drawing Title : Mr. Gandhi House
Location : Plot-276, Sector-55, Gurgaon
Scale : 1:1
Designed By : Rahul Thakur

HVAC Equipments Legends

S.No	Material	Description (All Dimensions in meters)
1		Cassette Indoor Unit
2		Hi-Wall Spilit Indoor Unit
3		Hard Drawn Copper Pipe
4		UPVC Drain Pipe
5		Y Branch

HAIER APPLIANCE (INDIA) PVT. LTD.
Building No. 01, Okhla Industrial Estate,
Phase 3, New Delhi

Email : info@haierindia.com, Website: www.haier.com/in.