

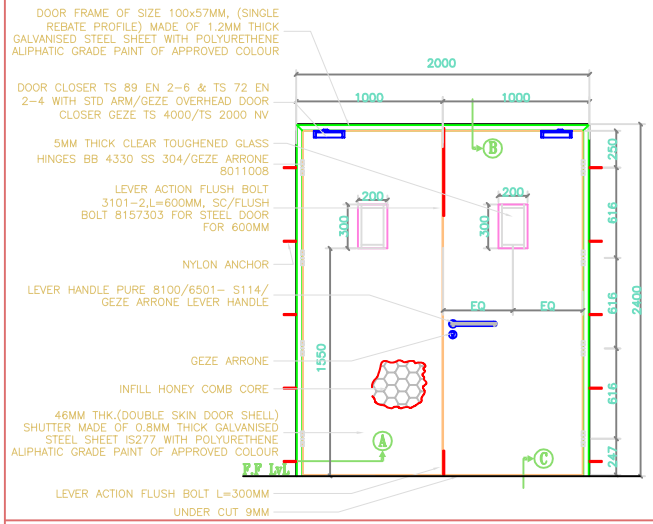


ST1/NON-FIRE RATED STEEL METAL DOOR
WITH VISION PANEL(DOUBLE SHUTTER) SIZE-2000x2400

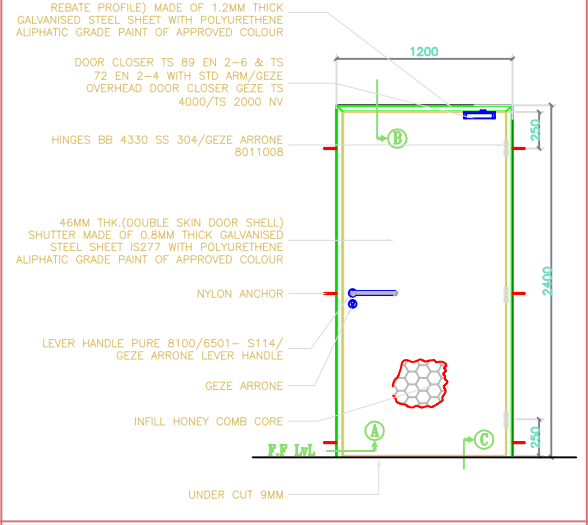

ST2/NON-FIRE RATED HOLLOW STEEL DOOR
(SINGLE SHUTTER) SIZE-1200x2400

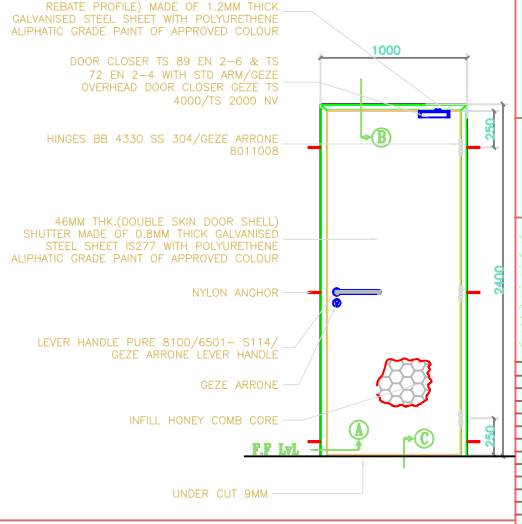

ST3/NON-FIRE RATED HOLLOW STEEL DOOR
(SINGLE SHUTTER) SIZE-1000x2400

KEY PLAN :-



LEGEND :-

N
W
E
S

GENERAL NOTES :

ALL DIMENSIONS ARE IN MILLIMETERS AND ARE UNFRAMED DIMENSIONS UNLESS OTHERWISE SPECIFIED.

ALL LEVELS ARE IN METERS AND ARE UNFRAMED LEVELS UNLESS OTHERWISE SPECIFIED.

DO NOT SCALE DRAWINGS. ONLY WRITTEN DIMENSIONS SHALL BE FOLLOWED, ANY DISCREPANCIES NOTED SHALL BE BROUGHT TO THE NOTICE OF THE ARCHITECT PRIOR TO EXECUTION.


FOR DETAILS SUCH AS DOORS, WINDOWS, GRILLS, GATES, SIGNAGE, TOILETS, KITCHENS, MASONRY, PAINTS, ETC. REFER RESPECTIVE ARCHITECTURAL DRAWINGS.

THESE DRAWINGS SHALL BE CORRELATED AND READ IN CONJUNCTION WITH RESPECTIVE CONSULTANT'S APPROVED DRAWINGS FOR STRUCTURAL WORKING, SERVICES SUCH AS PLUMBING, SANITARY, ELECTRICAL, AIR-CONDITIONING, FIRE FIGHTING, FIRE ALARM SYSTEMS, ETC. & SHOP DRAWINGS AND SPECIFICATIONS. ANY DISCREPANCIES NOTED SHALL BE BROUGHT TO THE NOTICE OF THE ARCHITECT PRIOR TO EXECUTION.


ALL TOILETS WILL HAVE SUNK FLOORS (UNLESS OTHERWISE SPECIFIED) AS PER RESPECTIVE STRUCTURAL DRAWINGS, AND WATERPROOFING AS PER SPECIFICATIONS.

SCHEDULE OF JOINERY


TYPE	DESCRIPTION	SIZE
RS	ROLLING SHUTTER	5000 x 5000
FD	FIRE DOOR	1200 x 2400
FD1	FIRE DOOR	2000 x 2400
ST1	STEEL DOOR	2000 x 2400
ST2	STEEL DOOR	1200 x 2400
ST3	STEEL DOOR	1000 x 2400
D	GLASS DOOR	3000 x 3000
D1	FLUSH DOOR	1800 x 2400
D2	GLASS DOOR	3000 x 3000
D5	FLUSH DOOR	1200 x 2400
D6	FLUSH DOOR (TOILET DOOR)	900 x 2100
D7	FLUSH DOOR (TOILET DOOR)	750 x 2100
L	LOUVER	2500 x 2100
V	VENTILATOR	600 x 600

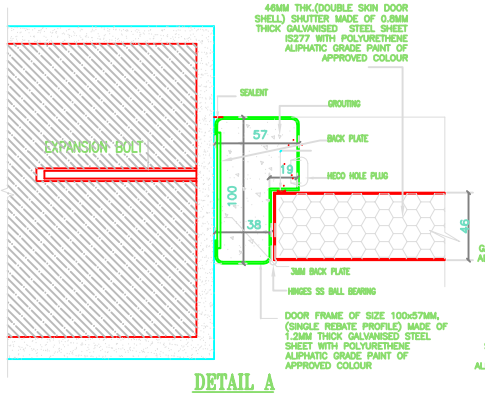


DETAIL A
SCALE 1:2

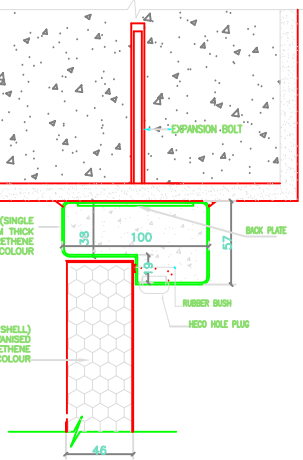

DETAIL-B
SCALE 1:2

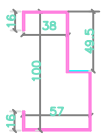

DOOR FRAME-100x57x1.2mm
(18 GAUGE STEEL SHEET-SINGLE REBATE PROFILE)

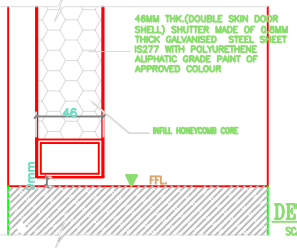

DETAIL C
SCALE 1:2

REV.	DESCRIPTION	DATE	BY	CHD.
R2	REVISED AS PER LATEST FLOOR PLAN	11-03-14	GB	EV
R1	ISSUED FOR CONSTRUCTION	06-03-14	GB	EV

AMENDMENT

GRAPHIC SCALE: 0 0.2M 0.6M 1.6M / 0.2M 0 0.4M 1.2M 2M

CLIENT:
M/s. Grazlano Transmissloni India Pvt. Ltd..

PROJECT:
PROPOSED ODS INDIA NEW PLANT IN GUJARAT.

DRAWING TITLE:
MAINFACTORY & OFFICE BUILDING JOINERY DETAILS (SHEET-3)

SCALE : 1 : 25	DRAWN : G.BABU	REV
DATE : 06-03-14	CHKD : E.VALLI	

DRAWING NO:
OEN-G-FAC-AR11-GR-02-177146 | R2

ARCHITECTURE • INTERIOR DESIGN • ENGINEERING • PLANNING • CONSTRUCTION MANAGEMENT

C R NARAYANA RAO
10, KARPAGAMBAL NAGAR, MYLAPORE, CHENNAI-600 004

B.Tech, (Hons.), M.S., (U.), Ph.D., M.Am.Soc. C.E., F.I.E., F.I.V., Chartered Engineer - Registered Architect.