




INSIDE ELEVATION

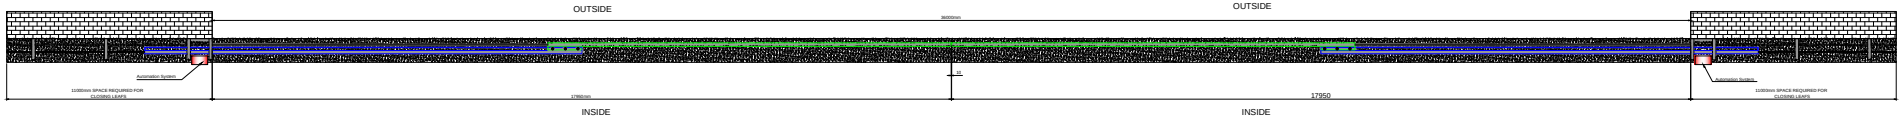


PLAN

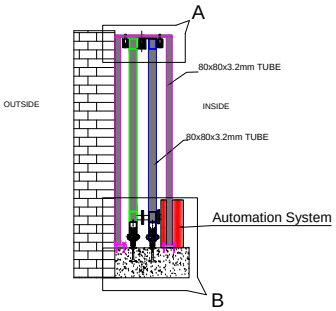

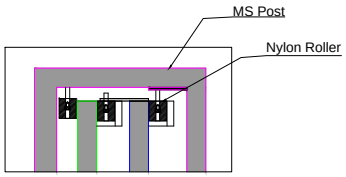

Detailed View of A

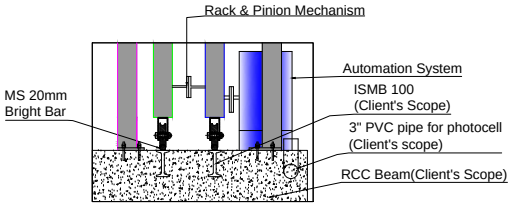

Detailed View of B

NOTE-
1. ALL REQUIRED CIVIL WORK WILL BE IN CLIENTS SCOPE.
2.IN NECESSARY GATE LEAF WILL BE IN TWO PARTS FOR TRANSPORTATION AND ILL BE WELDED TOGETHER ON SITE

SR NO	TUBE SPECIFICATION	
1	80X80X3.2mm	OUTER TUBE
2	40X40X2mm	INTERMEDIATE TUBE
3	125mm	GAP BETWEEN TUBE
4	80X80X3.2mm	POST TUBE

SR.NO	RAL CODE	RAL COLOR
04	RAL 7035	LIGHT GREY
03	RAL 5002	ULTRAMARINE BLUE
02	RAL 9002	GREY WHITE
01	RAL 1004	GOLDEN YELLOW

REV. NO.	DESCRIPTION	DRAWN	DATE	SIGN
REV.03	CHANGED SIZE	PRADEEP	15.03.2019	
REV.02	SIZE CHANGE AS PER PREVIOUS NOTE. NO. 2 REMOVED	AKASH	02.01.2019	
REV.01	CHANGED SIZE	SURAJ	25.12.2018	

CLEAR WIDTH	CLEAR HEIGHT	QUANTITY
36000mm	1800mm	1 NOS

This drawing & designing is the property of NIHVA TECHNOLOGIES. Not to be sold or copied to any other concern.

TITLE: Motorised telescopic Sliding gate 35m x 1.8m

	NAME	SIGN	DATE
DRAWN	SURAJ		08/12/18
CHECK	PRADEEP		08/12/18
APPROVAL	R.D		08/12/18

If any queries contact : design@nihva.com

ALL DIMENSION ARE IN mm

NIHVA TECHNOLOGIES PVT. LTD.
NIHVA TECHNOLOGIES PVT. LTD. PUNE
Tel : 020 66304033
Email:- info@nihva.com
Website:- www.nihva.com

CLIENT - INDAMER TECHNICS PVT. LTD.

PROJECT -

SITE LOCATION -

DWG. NO. : NIHVA/18-19/0196/R03 | Rev- 03

SCALE: NTS | WT: | SHEET: 01 OF 01