

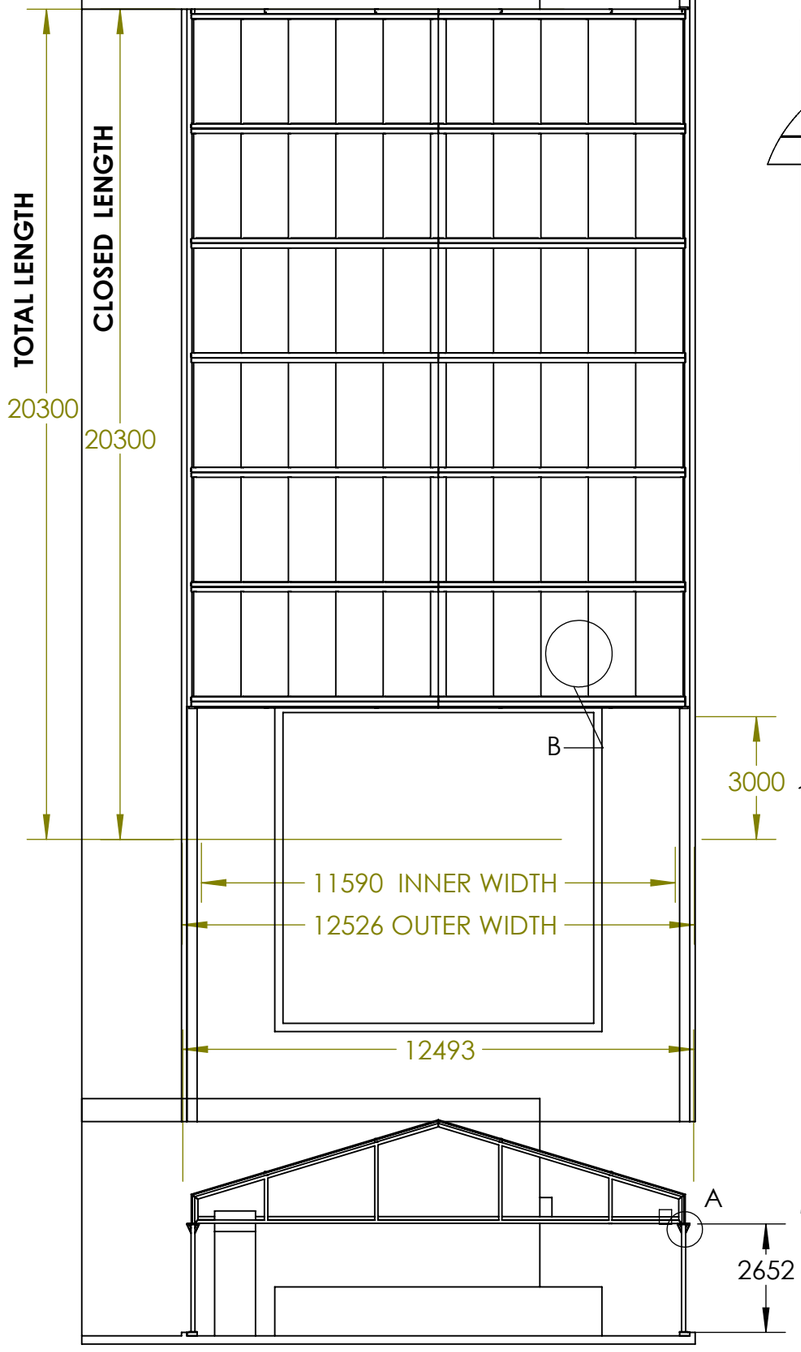


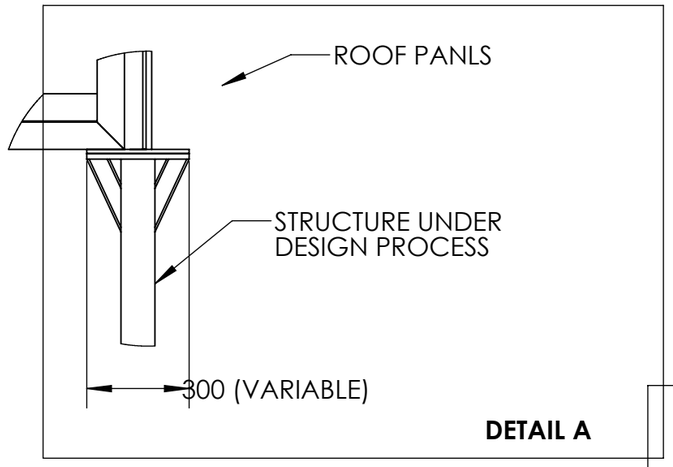



DETAIL A

DETAIL B
GRID SIZE

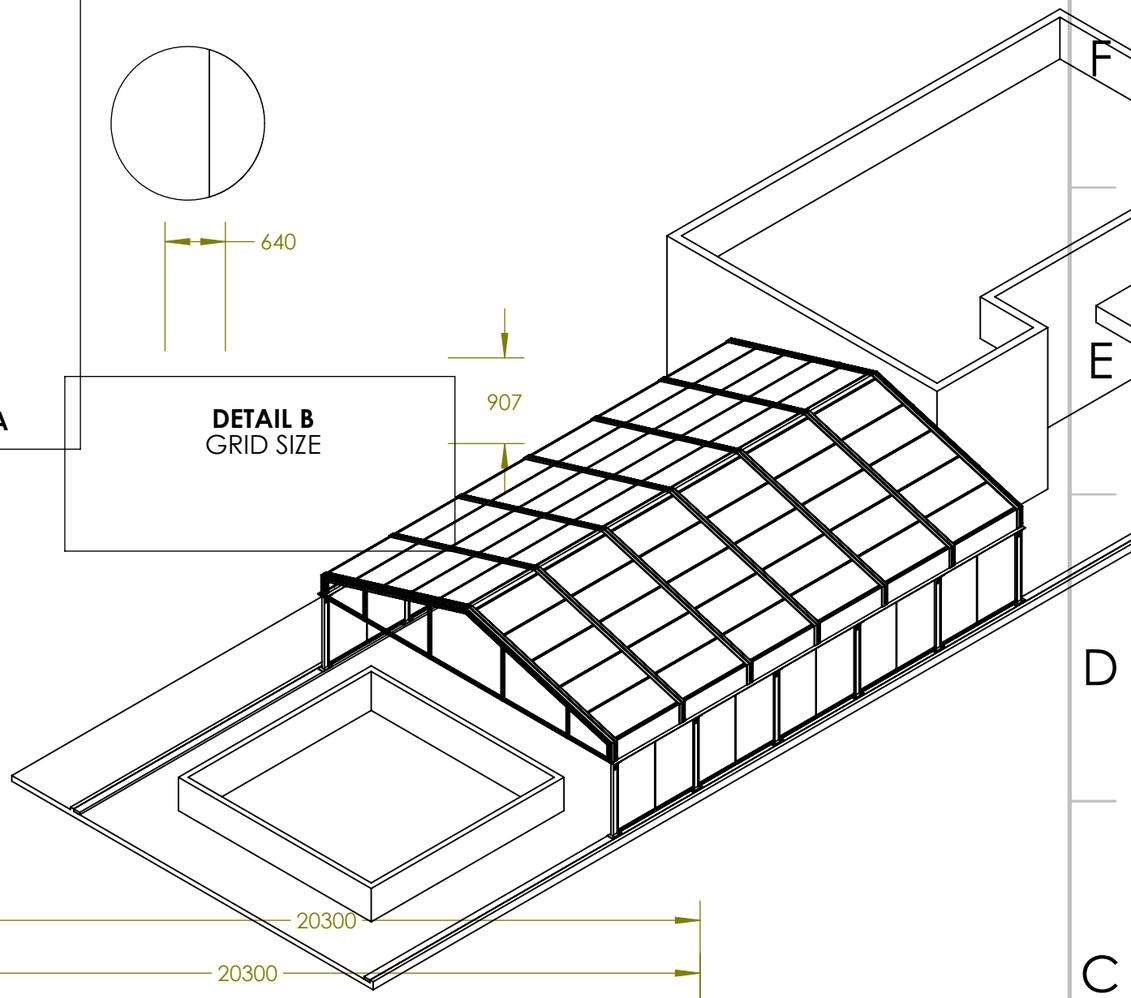

EXTRA SLIDING FOR STACKING
PURPOSE TO GET MORE OPENING

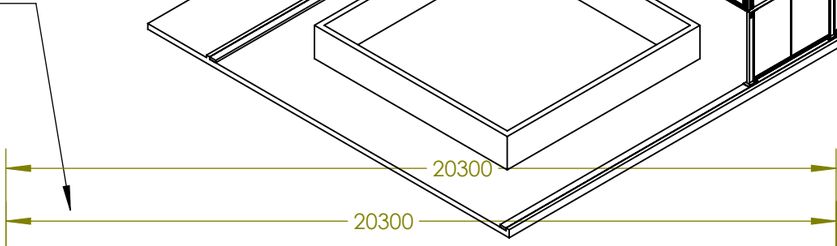

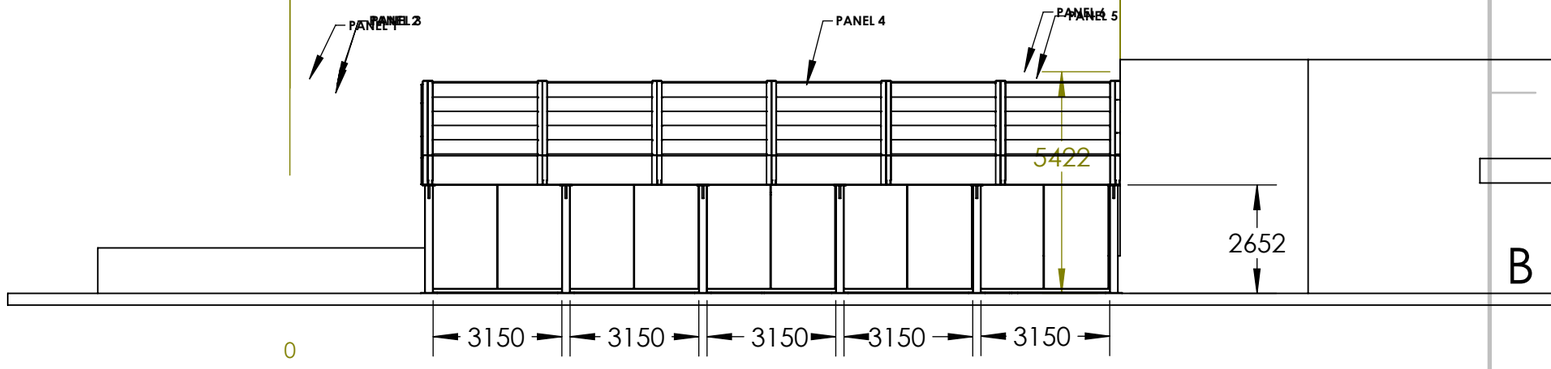

- STRUCTURE DESIGN IS UNDER PROCESS
  SO STRUCTURE DIMENSIONS MAY VARY ACCORDINGLY.

TITLE - ENCLOSED ROOF				NIHVA TECHNOLOGIES PVT.LTD.PUNE Website - www.nihva.com
	NAME	SIGNATURE	DATE	CLIENT - 24K
DRAWN	D. V.		05.04.2023	PRODUCT - RETRACTABLE ROOF
CHK'D	P. M.		05.04.2023	SITE LOCATION - PUNE_IN
APPV'D	V. T.		05.04.2023	
if any queries contact - supportautomation@nihva.com				DWG NO - NIHVA/22-23/00XX / REVISION -
ALL DIMENSION ARE IN mm			A3	SCALE - / SHEET 2 OF 2