

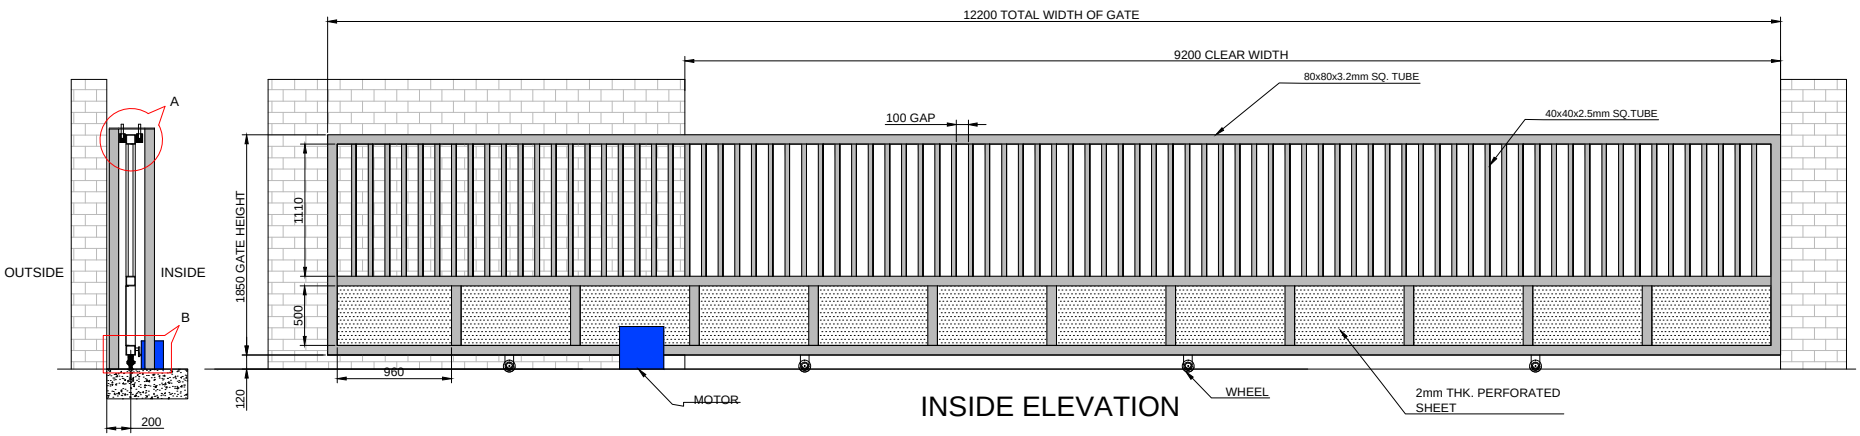



INSIDE ELEVATION

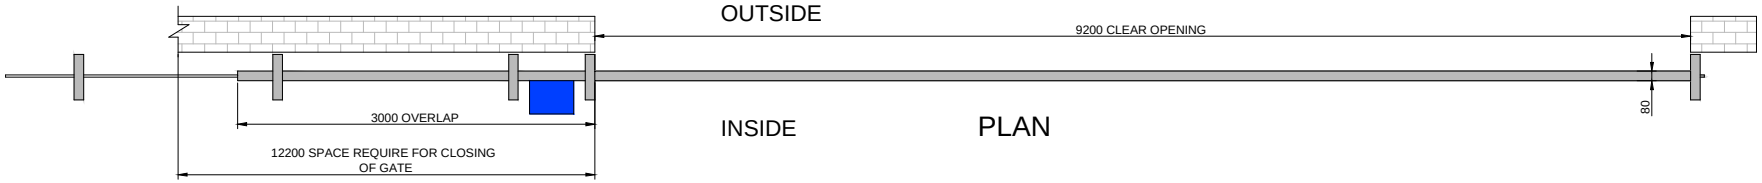

PLAN

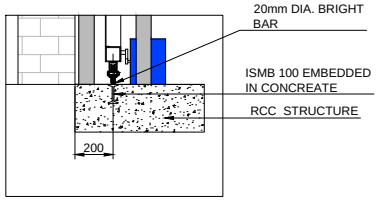

DETAILED VIEW OF A

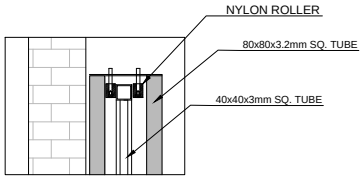

DETAILED VIEW OF B

DIMENSION :		
CLEAR WIDTH	CLEAR HEIGHT	QUANTITY
9200 mm	1850 mm	1 NOS.

MATERIAL :

THICKNESS :

NOTE: ALL REQUIRED CIVIL WORK WILL BE IN CLIENT'S SCOPE.

NIHVA TECHNOLOGIES PVT. LTD.

NIHVA TECHNOLOGY PVT. LTD. PUNE
Email:- info@nihva.com
Website:- www.nihva.com

TITLE:

SINGLE LEAF SLIDING GATE

CLIENT'S APPROVAL :

CLIENT - PROXIMITY ENGG.

PROJECT -

SITE LOCATION -

DWG. NO. : NIHVA/16-17/0063

SCALE: NTS	WT:	SHEET:1 OF 1
DRAWN BY: OMKAR		DATE: 30-08-2016
CHECK : ANIL		DATE: 30-08-2016

If any queries contact : projects@nihva.com

NOTE: ALL DIMENSION ARE IN mm

THIS DRAWING & DESIGNING IS THE PROPERTY OF NIHVA TECHNOLOGIES. NOT BE SOLD OR COPY TO ANY OTHER CONCERN.