




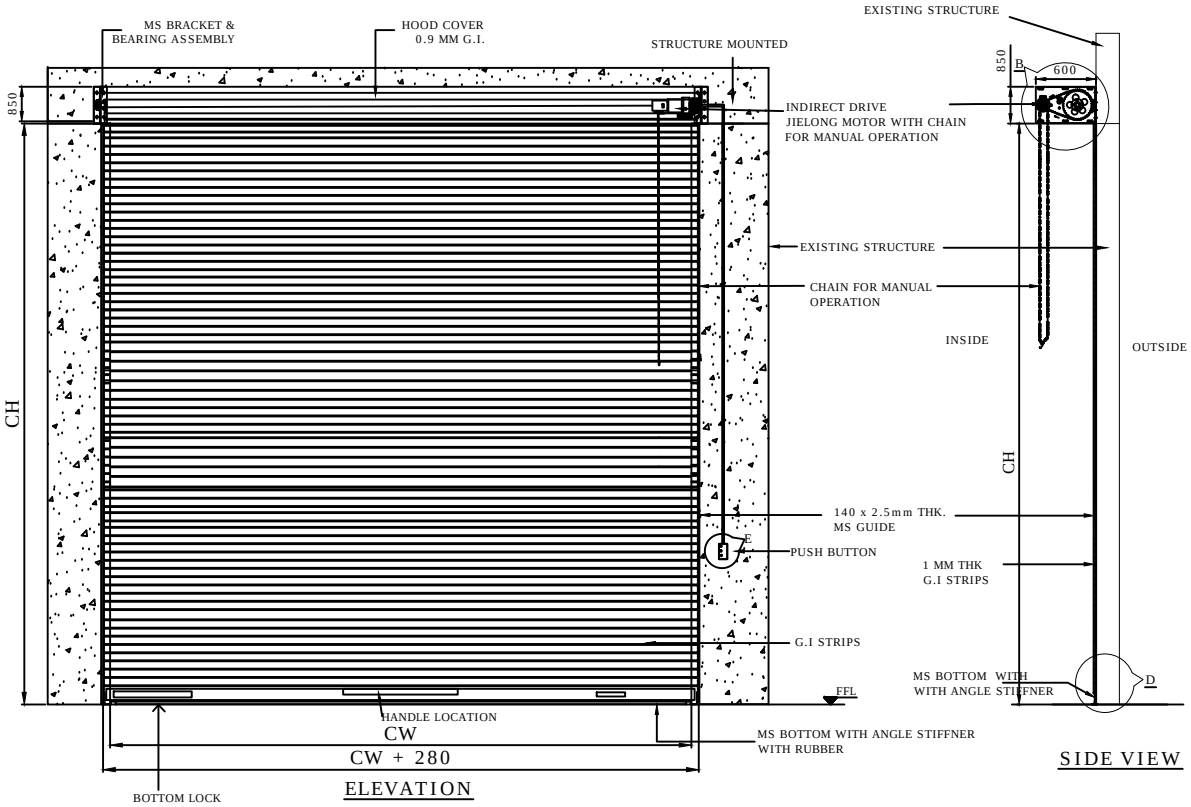


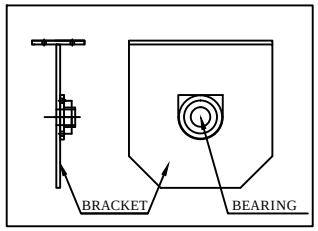

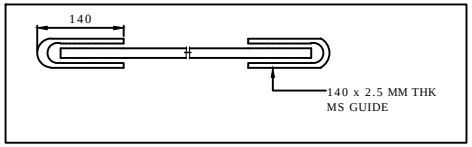

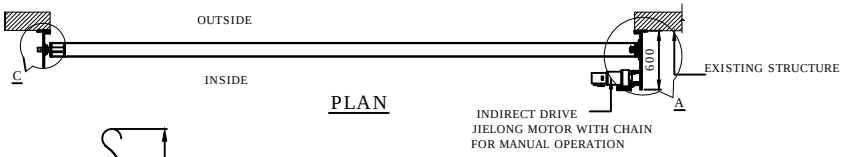

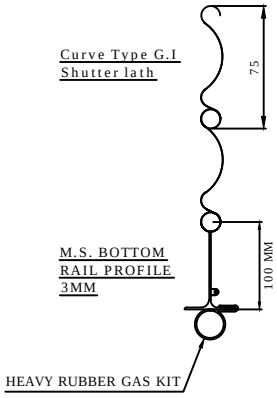

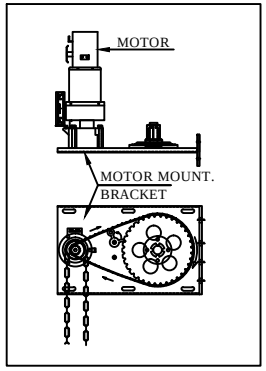

DETAILS : C

(NOTE: REQUIRED TECHNICAL STRUCTURE & CIVIL WORK FOR SHUTTER IN CLIENT SCOPE)

4500	5000	1	RAL 9002 POWDER COATING
CLEAR WIDTH (CW)	CLEAR HEIGHT (CH)	QUANTITY	RAL COLOR

This drawing & design is the property of NIHVA TECHNOLOGIES. Not to be sold or copied to any other concern.

TITLE G.I. SLAT MOTORIZED ROLLING SHUTTER

NIHVA TECHNOLOGIES PVT. LTD.

NIHVA TECHNOLOGIES PVT. LTD. PUNE
Tel : 020 66304033
Email:- info@nihva.com
Website:- www.nihva.com

	NAME	SIGN	DATE
DRAWN	S.M.S.		7.11.2020
CHECK			
APPRD.			

CLIENT -

PROJECT -

SITE LOCATION - PUNE

If any queries contact : projectsupport@nihva.com

DWG. NO. : NIHVA/20-21/VDR/0074 REV- R01

ALL DIMENSION ARE IN mm

SCALE: NTS WT: SHEET: