

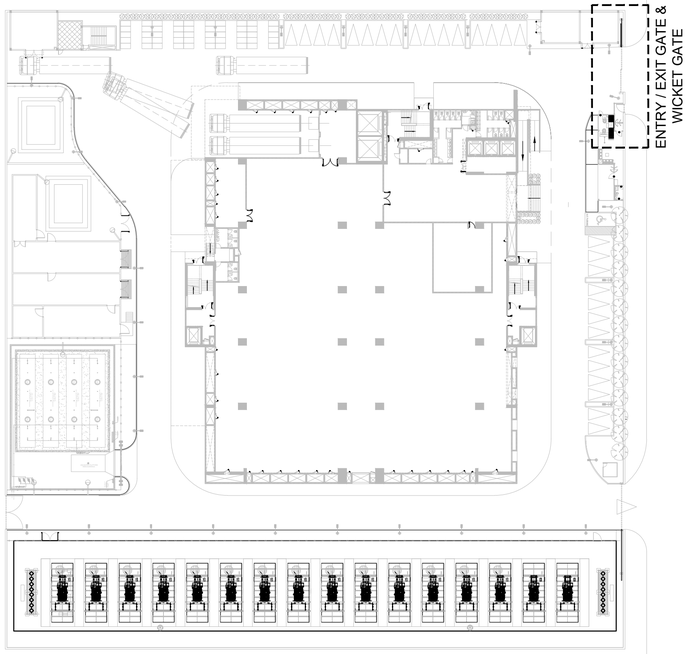



KEY PLAN

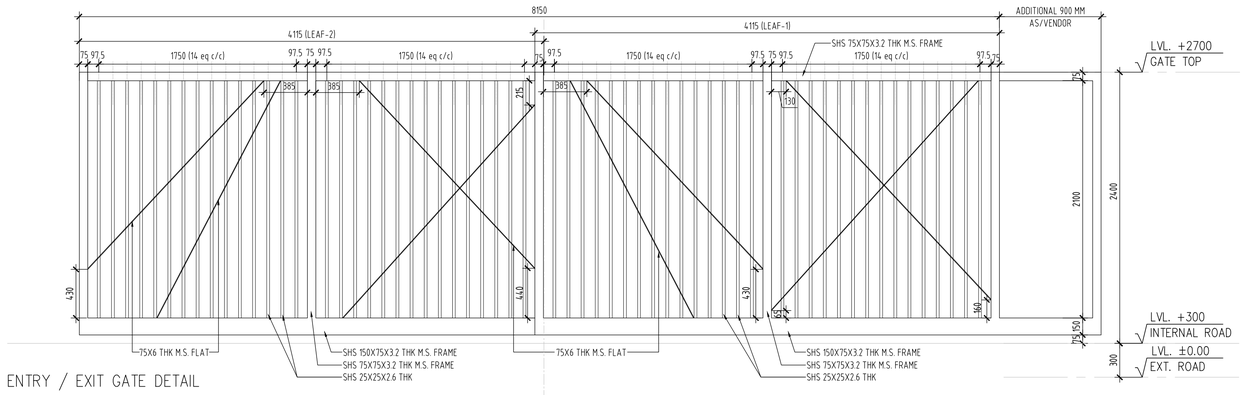


ENTRY / EXIT GATE DETAIL

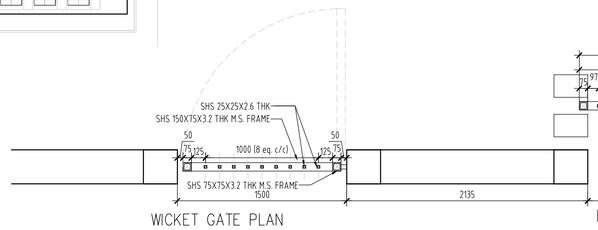

WICKET GATE PLAN

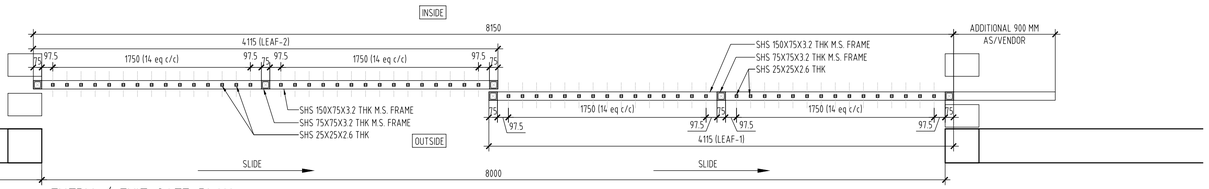

ENTRY / EXIT GATE PLAN

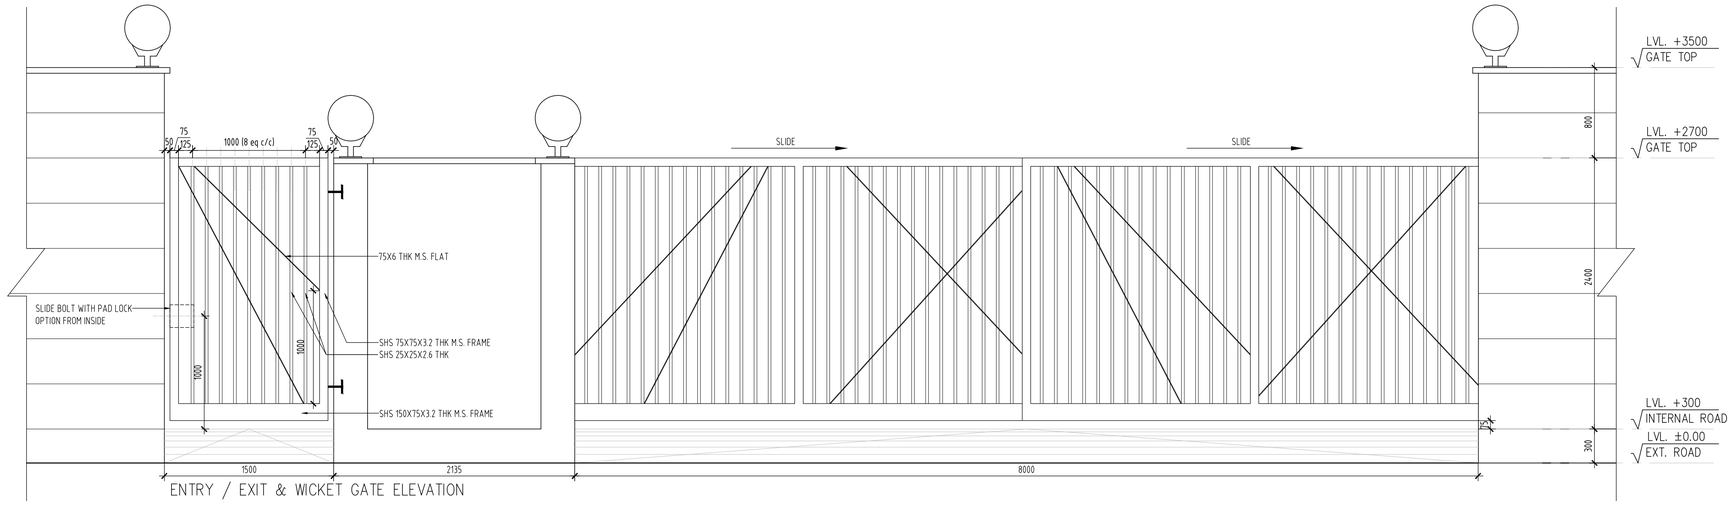

ENTRY / EXIT & WICKET GATE ELEVATION

DESIGNPLUS ARCHITECTURE
S-296, Greater Kailash Part -2,
New Delhi -110048
Ph-41613854, 41623854

22/01/2021

GOOD FOR CONSTRUCTION

NOTES :

1. THIS DRAWING IS THE PROPERTY AND COPYRIGHT OF M/S DESIGN PLUS ARCHITECTURE (P) LTD. & SHALL NOT BE COPIED OR USED IN ANY WAY WITHOUT THEIR WRITTEN PERMISSION.
2. THIS DRAWING SHALL BE READ IN CONJUNCTION WITH THE OTHER RELEVANT ARCHITECTURAL AND OTHER CONSULTANTS DRAWINGS. IT SHALL BE DEEMED THE RESPONSIBILITY OF THE CONTRACTOR/ OR THE FABRICATOR TO BRING TO THE NOTICE OF THE ARCHITECTS, PRIOR TO ANY CONSTRUCTION OR FABRICATION ANY DISCREPANCY WITHIN OR BETWEEN THE AFOREMENTIONED DRAWINGS.
3. ALL DIMENSIONS ARE IN MM AND TO BE READ ONLY AND NOT MEASURED
4. ANY DISCREPANCY IN THE CROSS CHECK DIMENSIONS ARE TO BE BROUGHT TO THE NOTICE OF THE ARCHITECTS BY THE CONTRACTOR/PROJECT MANAGERS IMMEDIATELY.
5. PROJECT MANAGERS/ CONTRACTORS TO VERIFY ALL SITE CONDITIONS AND ANY CONDITION DIFFERENT OR NOT IN COHERENCE WITH THE DRAWINGS/DETAILS MUST BE IMMEDIATELY INFORMED TO THE ARCHITECTS.
6. ALL DRAWINGS,DETAILS TO BE REFEREED IN CONJUNCTION TO THE CORRESPONDING ITEMS OF BILL OF QUANTITIES. ANY DISCREPANCY TO BE INFORMED TO THE ARCHITECTS.

NO	DATE	REVISION
REVISIONS		

CONSULTANTS:

PROJECT MANAGER:

STRUCTURAL CONSULTANTS:
TPC TECHNICAL PROJECTS CONSULTANTS PVT. LTD.
B-74, SECTOR-57, NOIDA, U.P.

MEP CONSULTANTS:
PROION CONSULTANTS PVT. LTD.
82, SUKHDEV VIHAR, NEW DELHI

LANDSCAPE ARCHITECT:

PROJECT TITLE:
IT PARK, 143 NOIDA

OWNER:
M/S URVASI INFRATECH PVT. LTD.
GATEWAY TOWER, DLF PHASE-3, GURUGRAM, HARYANA

ARCHITECT:
DESIGNPLUS ARCHITECTURE
S-296, GREATER KAILASH, PART-2
NEW DELHI-110048

KEY PLAN:

DRAWING TITLE:
STT BLOCK
ENTRY/EXIT GATE &
WICKET GATE DETAIL

DEALT BY:	KAPIL		
CHKD BY:	DIMANJEET	SCALE:	1:25
APPROVED BY:	S.M.	DATE:	22.01.2021

PURPOSE :
- ☐ FOR TENDER
- ☐ FOR INFORMATION
- ■ FOR EXECUTION
- ☐ FOR APPROVAL

A

DRAWING NO: NOIDA-AR-STT-LDSP-611

REVISION: R0