
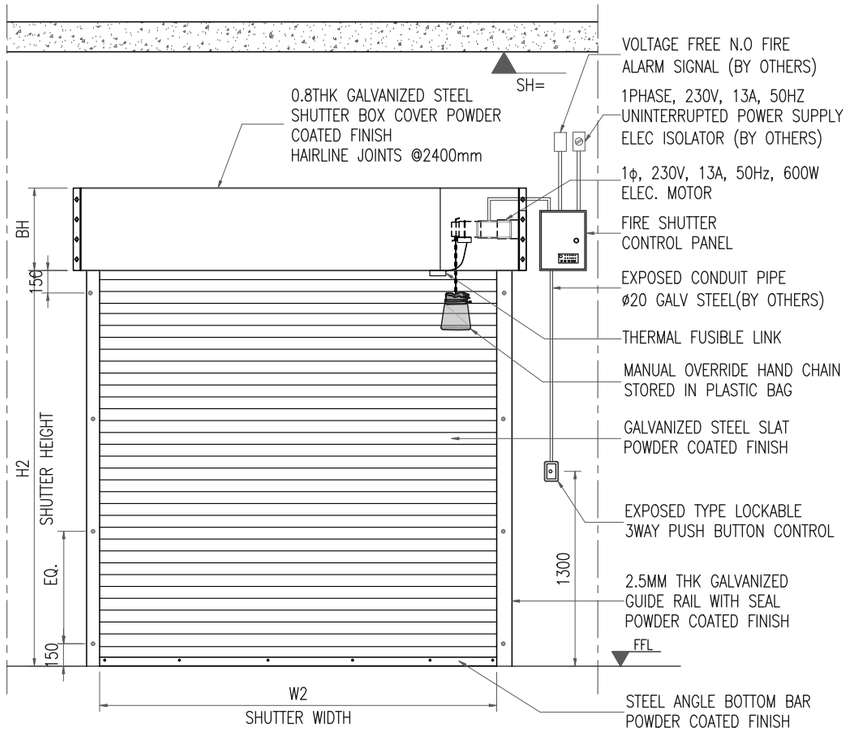



A — INTERIOR ELEVATION
SCALE: 1:40

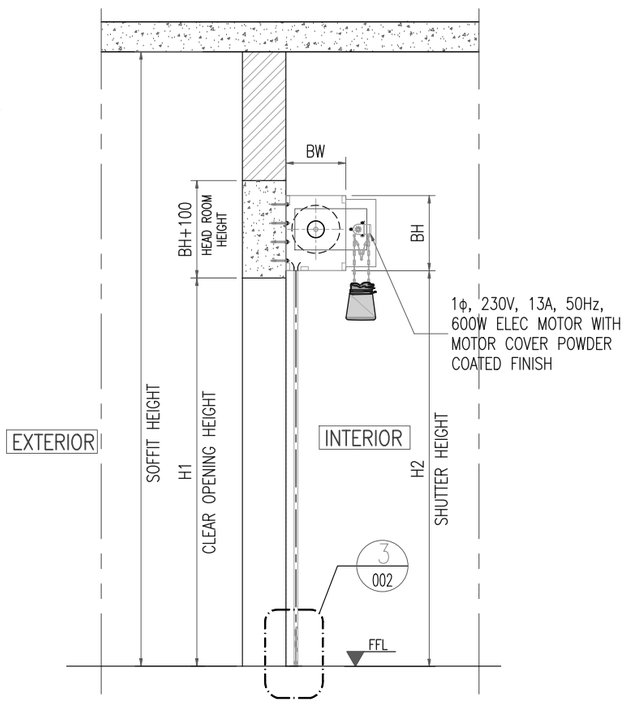

A1 — SECTION
SCALE: 1:40

2HRS FIRE RATED ROLLER SHUTTER – SCHEDULE


S.NO	SHUTTER REF.	QTY	OPENING SIZE W1	OPENING SIZE H1	SHUTTER SIZE W2	SHUTTER SIZE H2	HEAD BOX SIZE BW	HEAD BOX SIZE BH	MOTOR LOCATION	SHUTTER FINISH
1	FRS–1	1	2700	3500	2750	3550	500	600	TBC	TBC
2	FRS–2	1	2700	3500	2750	3550	500	600	TBC	TBC
3	FRS–3	1	2700	3500	2750	3550	500	600	TBC	TBC
4	FRS–4	1	2700	3500	2750	3550	500	600	TBC	TBC
5	FRS–5	1	2700	3500	2750	3550	500	600	TBC	TBC
6	FRS–6	1	2700	3500	2750	3550	500	600	TBC	TBC
7	FRS–7	1	2700	3500	2750	3550	500	600	TBC	TBC
8	FRS–8	1	2700	3500	2750	3550	500	600	TBC	TBC
9	FRS–9	1	2700	3500	2750	3550	500	600	TBC	TBC
10	FRS–10	1	2700	3500	2750	3550	500	600	TBC	TBC
11	FRS–11	1	2700	3500	2750	3550	500	600	TBC	TBC
12	FRS–12	1	2700	3500	2750	3550	500	600	TBC	TBC
13	FRS–13	1	2700	3500	2750	3550	500	600	TBC	TBC
14	FRS–14	1	2700	3500	2750	3550	500	600	TBC	TBC
15	FRS–15	1	2700	3500	2750	3550	500	600	TBC	TBC
16	FRS–16	1	2700	3500	2750	3550	500	600	TBC	TBC
17	FRS–17	1	2700	3500	2750	3550	500	600	TBC	TBC
18	FRS–18	1	2700	3500	2750	3550	500	600	TBC	TBC
19	FRS–19	1	2700	3500	2750	3550	500	600	TBC	TBC
20	FRS–20	1	2700	3500	2750	3550	500	600	TBC	TBC
21	FRS–21	1	2700	3500	2750	3550	500	600	TBC	TBC
22	FRS–22	1	2700	3500	2750	3550	500	600	TBC	TBC
23	FRS–23	1	2700	3500	2750	3550	500	600	TBC	TBC

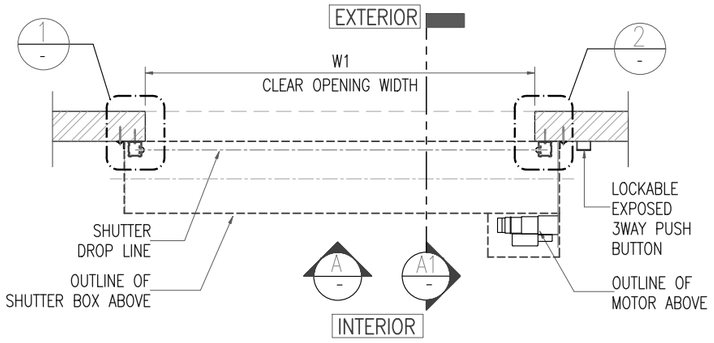

PLAN– 2HRS SINGLE SKIN ROLLER SHUTTER
SCALE: 1:40

SPECIFICATIONS (2HRS FIRE RATED SHUTTER) :-

SLAT	1.2mm THK GALVANIZED STEEL SINGLE SKIN SLAT, POWDER COATED FINISH
SIDE GUIDE	2.5mmTHK GALV. STEEL 'G' TYPE GUIDE POWDER COATED FINISH
END PLATE	MS PLATE, GREY PRIMER COATED
BOTTOM ANGLE	4mmTHK x 40 x 40 STEEL ANGLE BOTTOM BAR, POWDER COATED FINISH
SHUTTER BOX COVER	0.8mmTHK GALVANIZED STEEL, POWDER COATED FINISH
MOTOR COVER	0.8mmTHK GALVANIZED STEEL, POWDER COATED FINISH
MODE OF OPERATION	ELECTRICAL
POWER SUPPLY	1 PHASE, 230V, 13A, 50Hz ISOLATOR
FIRE ALARM SIGNAL	VOLTAGE FREE NORMALLY OPEN SIGNAL
AUTO CLOSING DEVICE	1) THERMAL FUSIBLE LINK
	2) FIRE ALARM SIGNAL
ACCESSORIES	1) 3 WAY PUSH BUTTON
	2) MANUAL OVERRIDE CHAIN

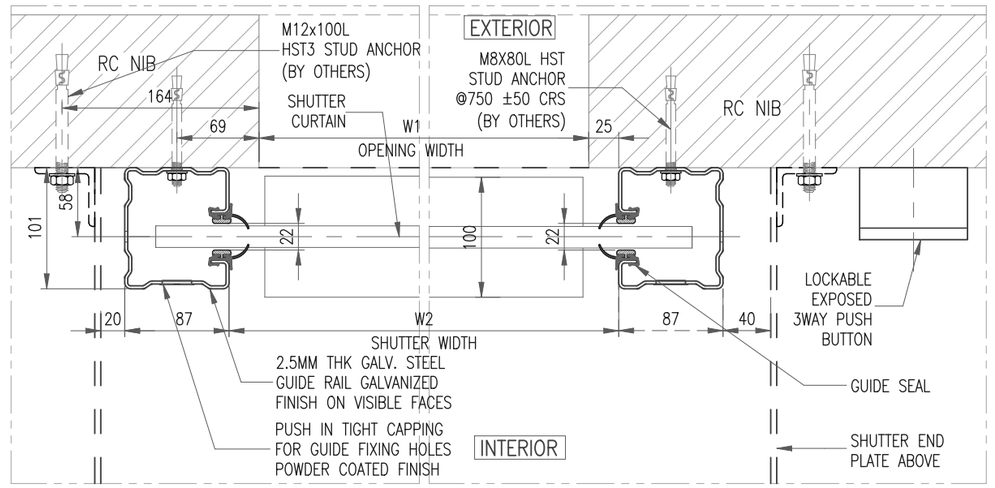

1 — ENLARGED VIEW
SCALE: 1:5

2 — ENLARGED VIEW
SCALE: 1:5

COLOR OF POWDER COATING FINISH : TBC	
PARTS	FINISH
GALV. STEEL SLAT	POWDER COATED FINISH
BOTTOM BAR	POWDER COATED FINISH
GALV. STEEL GUIDE RAIL	POWDER COATED FINISH
BOX COVER,	POWDER COATED FINISH

NOTE :
ALL DIMENSIONS ARE IN MILLIMETERS UNLESS OTHERWISE STATED.

Rev.	Date	By	Description	Checked	Approved
0	30.01.26	PS	FOR APPROVAL	SK	

ferco FERCO SHUTTERS AND SEATING SYSTEMS PRIVATE LIMITED
Survey No.8/1A2B,8/2A2, Industrial Shed, Parivakkam Road, Senneerkuppam, Poonamallee, Chennai 600056.

Contractor :
M/S. NIHVA TECHNOLOGIES
PUNE

Project Title :
SUPPLY OF 2HRS FIRE SHUTTER

Drawing Title :
2HRS FIRE RATED ROLLER SHUTTER PLAN,ELEVATION,SECTION & DETAILS

Designed	Checked	Approved
PS	SK	
Scale: As shown	Drawn: PS	Date: 30.01.2026

Drawing No. : FER–NHT–FRS–SD–001 | Rev. 0 | Sheet 1 of 3
CAD File Name : FER–NHT–FRS–SD–001_0.dwg | A3

Date Printed: 30–Jan–26

File Path: \\design1\Shared–Design1\Projects dwgs – 2025\1.QUOTE STAGE PROJECTS\F25–26–099 – Nihva technologies – FRS – S\Shop Drawing