
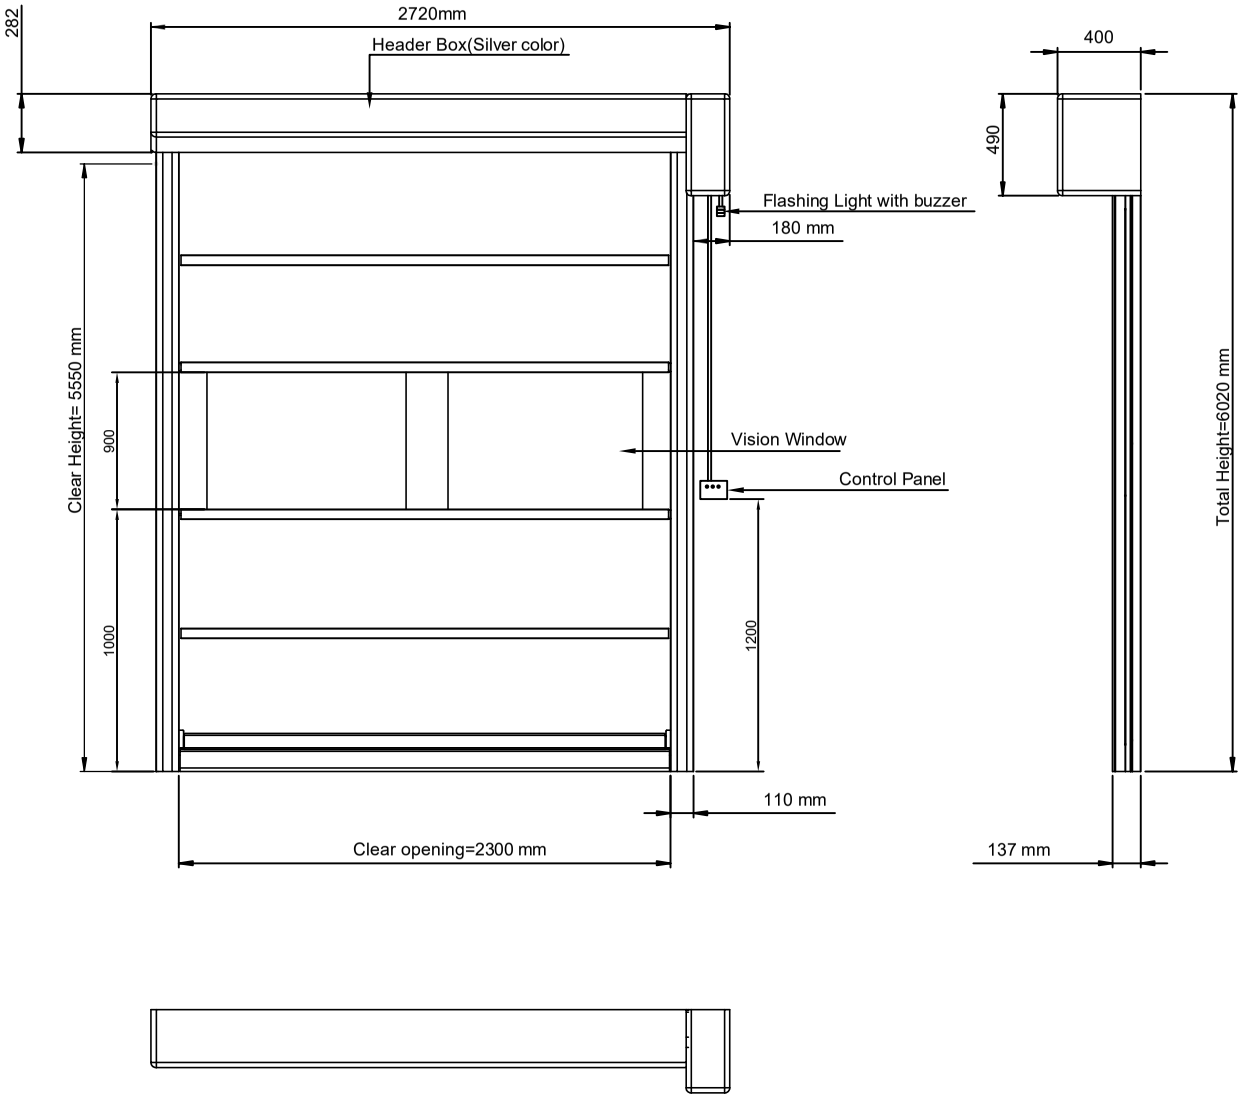


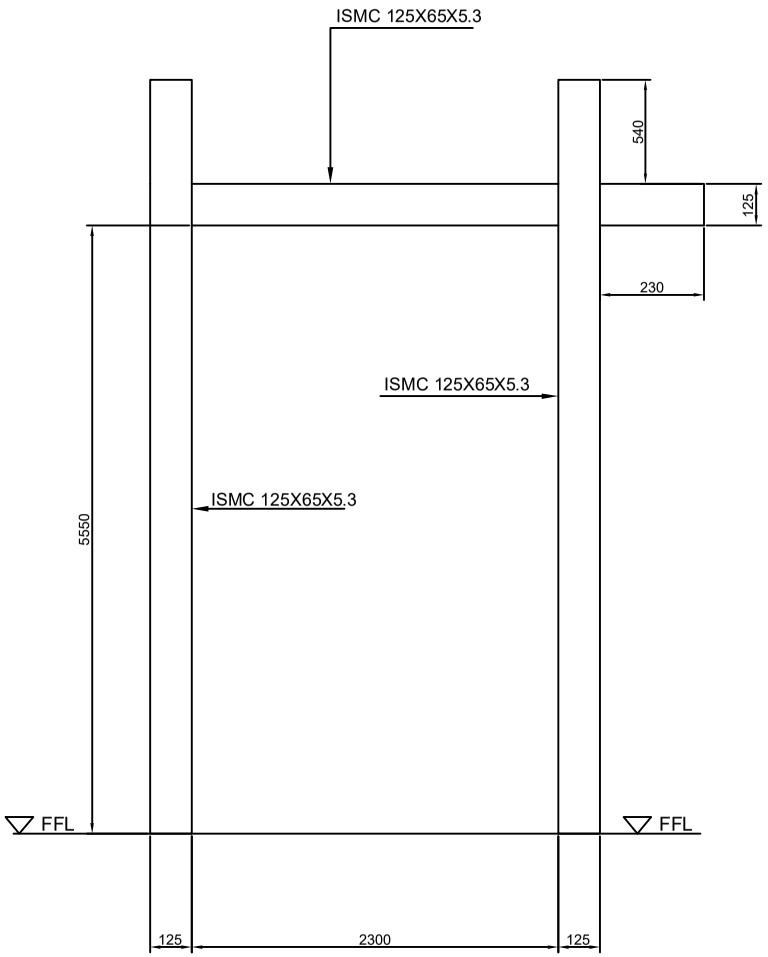

Note:--

1.All Dimension are in MM

2.All Civil work and structure is in client scope

3.Curtain color is Gray RAL 7035

Rev No.	Revision	Date	Revised By

This drawing & design is the property of NIHVA TECHNOLOGIES. Not to be sold or copied to any other concern.

TITLE:- HIGH SPEED DOOR

NIHVA TECHNOLOGIES PVT. LTD.
NIHVA TECHNOLOGIES PVT. LTD. PUNE
Tel : 020 66304033
Email:- info@nihva.com
Website:- www.nihva.com

	NAME	DATE	SIGN
DRAWN	SUJATA	11/01/2022	
CHECK	G. P	11/01/2022	
APPRD.	A.K	11/01/2022	

CLIENT - YASH HIGHVOLTAGE LTD.

LOCATION -GUJARAT

PRODUCT - HSD

If any queries contact : design@nihva.com

DWG NO:-NIHVA/21-22/CLT/0310 REV- 0

ALL DIMENSION ARE IN mm

SCALE: NTS SCALE:-- 1:1 SHEET: 01 OF 01