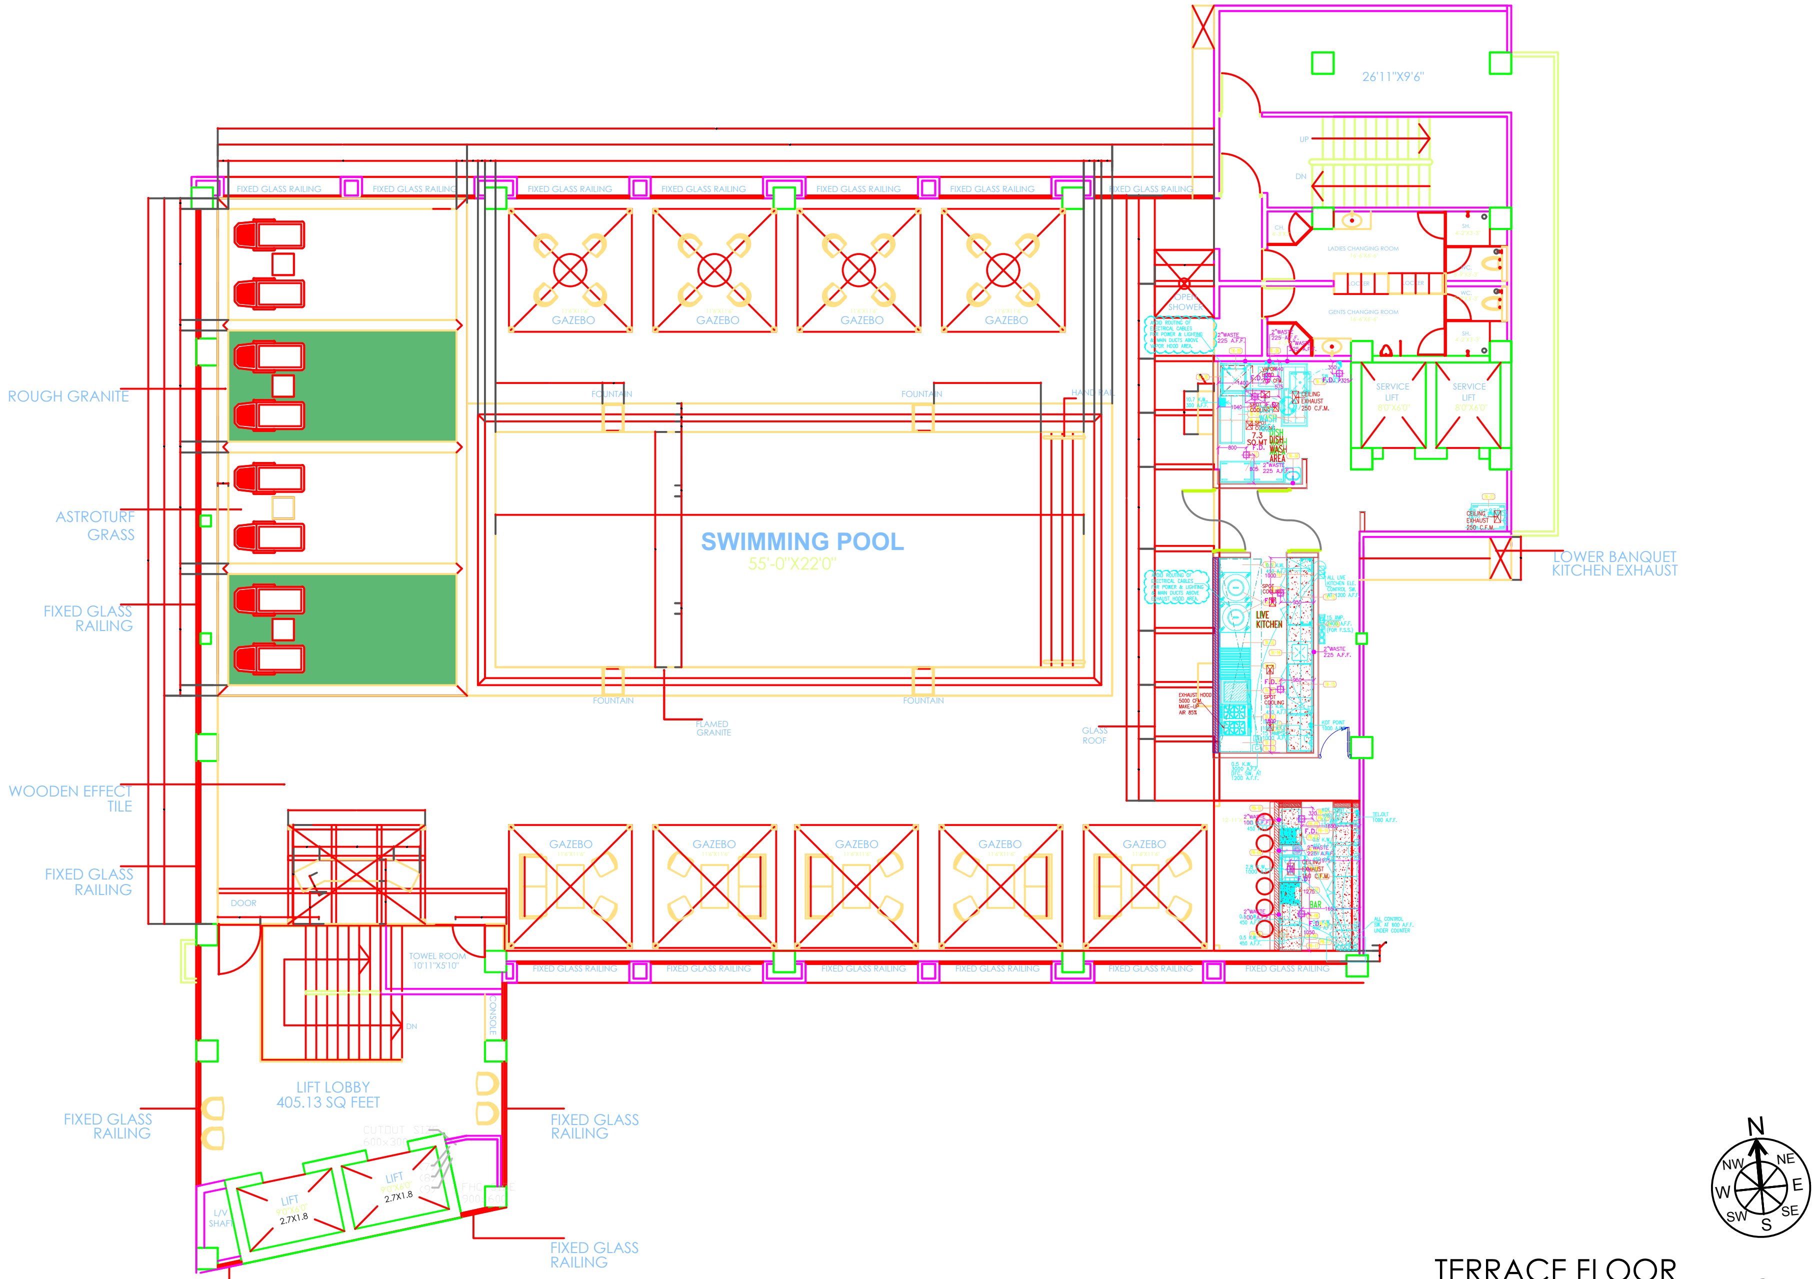

TERRACE FLOOR LAYOUT

MINARY DRG.	P0	PROJECT: PROPOSED RADISSON HOTEL INTERIOR. AT GORAKHPUR
PPROVAL & MENTS		
TLE: TERRACE FLOOR TERLLAY-001		CLIENTS: M/S. CONTINENTAL DEVELOPERS PVT. LTD.

NOTES:
- THIS IS A SCHEMATIC DRG. FOR GUIDELINES TO SHOP DRG
- ALL DIMENSIONS ARE IN INCHES
- REFER WRITTEN DIMENSIONS ONLY
- CONTRACTOR SHOULD CROSS-CHECK ALL DIMENSIONS,AND IF ANY DISCREPANCY FOUND, IT SHOULD GET RECTIFIED FROM ARCHITECT PRIOR TO EXECUTION.

THIS DRAWING, INCLUDING ANY PATENTED OR PATENTABLE FEATURES EMBODIES CONFIDENTIAL INFORMATION OF NAREN KUWADEKAR & ASSOCIATES AND ITS USE IS CONDITIONED UPON THE USER'S AGREEMENT NOT TO REPRODUCE THE DRAWING IN WHOLE OR IN PART NOR THE MATERIAL DESCRIBED THEREON, NOR TO USE THE DRAWING FOR ANY PURPOSE OTHER THAN SPECIFICALLY PERMITTED IN WRITING BY NAREN KUWADEKAR & ASSOCIATES.

TITLE- TERRACE.FLOOR	DRG. NO.	A/16	DATE	19-05-16
SCALE 1/4"-1'0"	DRN. BY	S.M.	CHK.BY	S.M.

ARCHITECTS • PROJECT PLANNERS • LANDSCAPE DESIGNERS
NAREN KUWADEKAR
& ASSOCIATES.
201,ABHISHEK
OPP.SAB TV
OFF NEW ANDHRI LINK RD.
MUMBAI - 400 058.