

DRAWING

REV DESCRIPTION	DATE	REV NO
	24-07-2026	REV 00

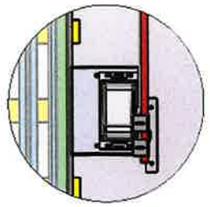


DETAIL B
SCALE 1 : 18

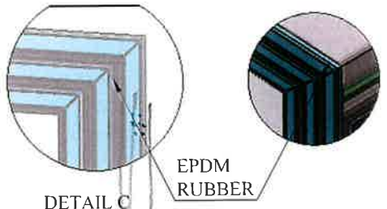


DETAIL C
SCALE 1 : 18

DETAIL F
SCALE 1 : 20

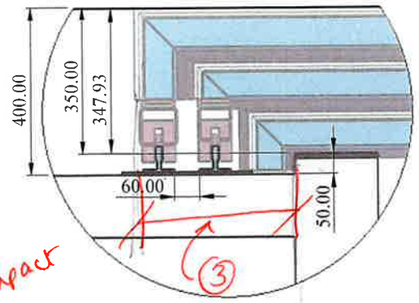


DETAIL E
SCALE 1 : 10

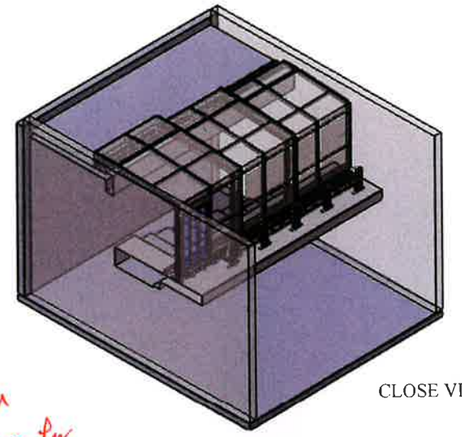


CLOSE VIEW

* Operating Weight?

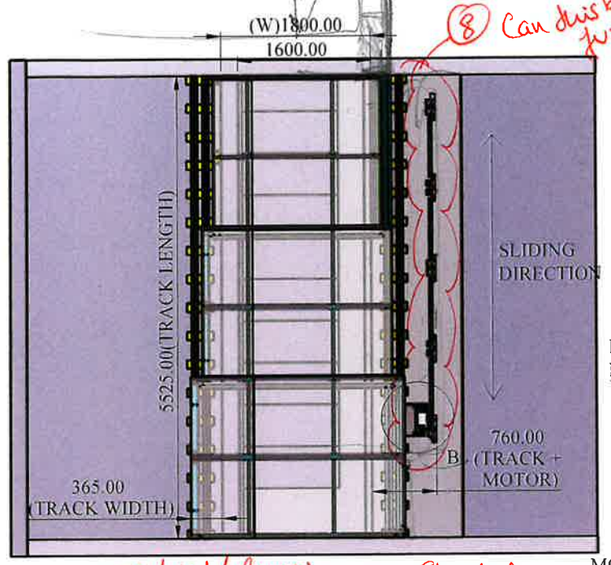


8 Can this be Compact further

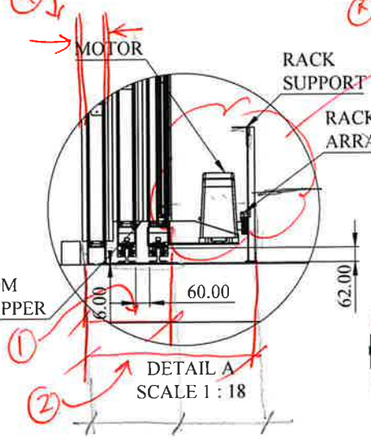


DETAIL A
SCALE 1 : 18

4 Kindly Confirm usage & Size for these Members

5 Can these be eliminated / Covered

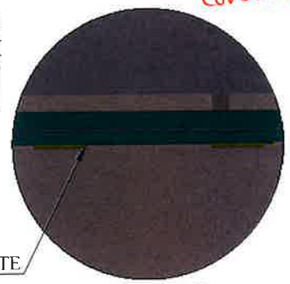



DETAIL H
SCALE 1 : 8

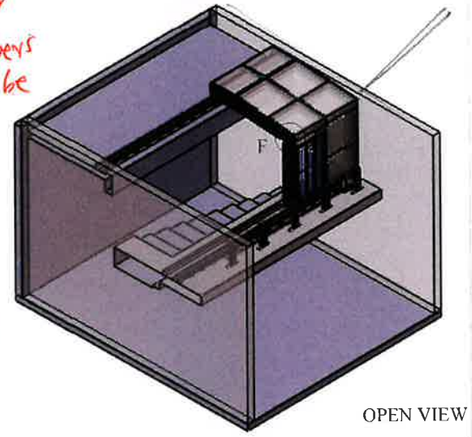


OPEN VIEW

6 Operating Load / Reaction on Structure

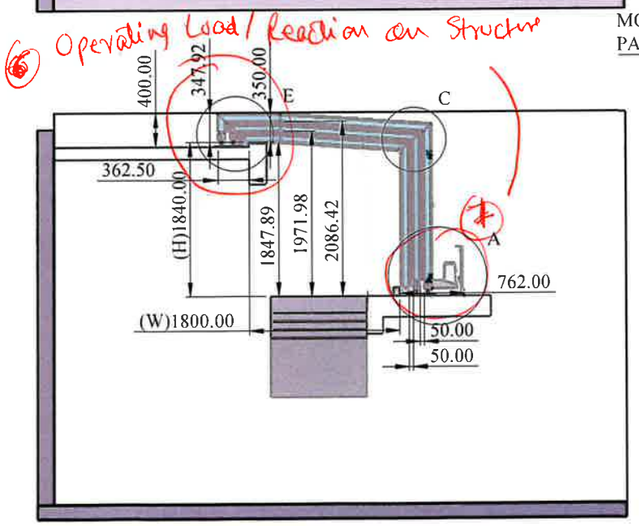

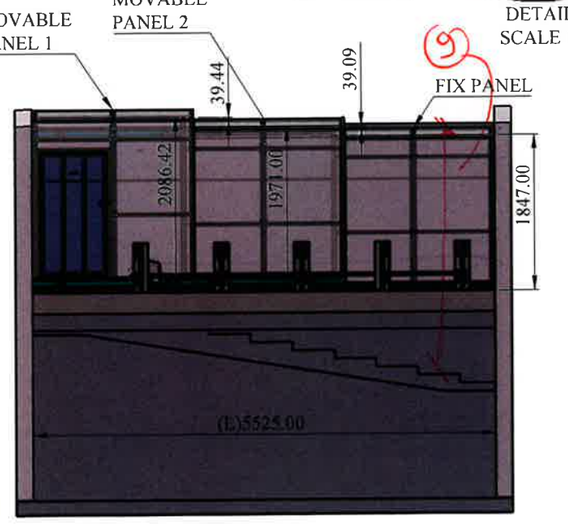

9

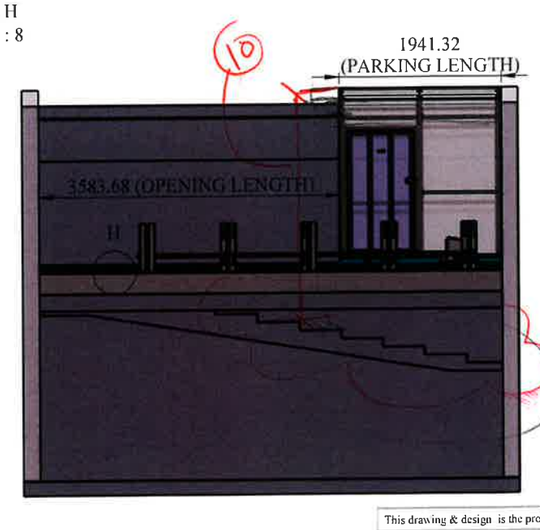

Show Stairs in True Scale as per architect Intent

NOTE :

THIS DRAWING IS FOR CLIENT APPROVAL
BASE STRUCTURE IN CLIENT SCOPE
EPDM RUBBER FLAPPER PROVIDED FOR AIR WATER SEAL.

SPECIAL INSTRUCTION'S :

This drawing & design is the property of NIHVA TECHONOLOGIES PVT. LTD. Not to be sold or copied to any other concern

TITLE - L SHAPE ENCLOSURE
DWG NO - NTPL-000

NIHVA TECHNOLOGIES PVT.LTD.PUNE
Website - www.nihva.com

	NAME	SIGNATURE	DATE
DRAWN	V.W.		24-07-2026
CHK'D	S.P.		25-07-2026
APPV'D	V.T.		25-07-2026

If any queries contact - info@nihva.com
ALL DIMENSION ARE IN mm | A2

PRODUCT - L SHAPE ENCLOSURE.
CLIENT NAME - LODHA GROUP.
SITE LOCATION - MUMBAI (VERSOVA).
MATRIAL - | QTY - 1
PROJECTION METHOD: | SCALE :
SHEET 1 OF 1