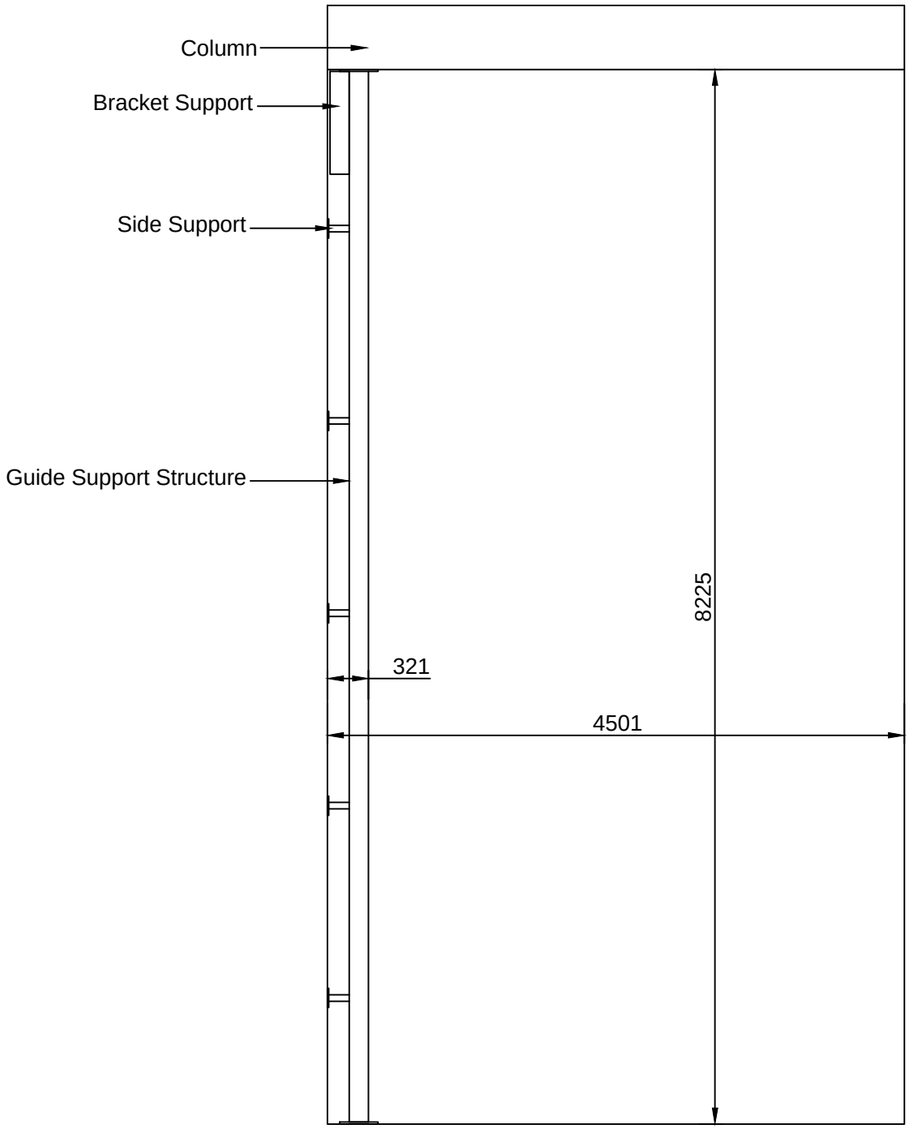

View From Outside

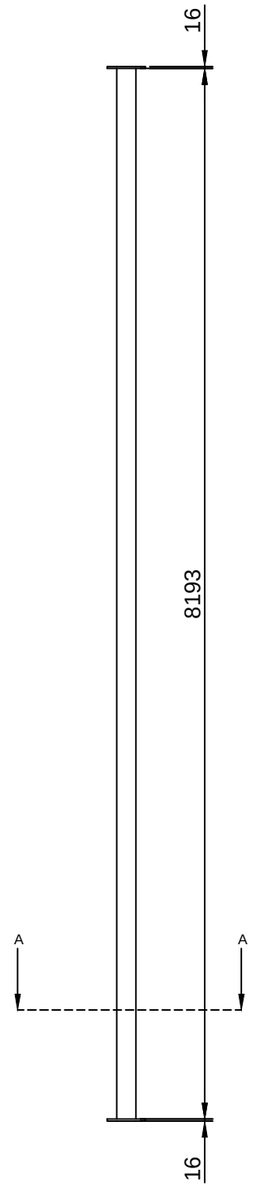

Guide Support Structure Assembly

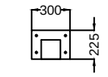

Section A-A

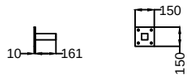

Side Support Ass.

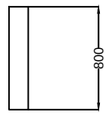

Bracket Support
SHS 150 x 150

DIMENSION :

CLEAR WIDTH	CLEAR HEIGHT	QUANTITY
4180 mm	7900 mm	1 No

MATERIAL :

THICKNESS :

NOTE:-

NIHVA TECHNOLOGIES PVT. LTD.

NIHVA TECHNOLOGIES PVT. LTD. PUNE
Email:- info@nihva.com
Website:- www.nihva.com

TITLE:

DOUBLE WALL ROLLING SHUTTER STRUCTURE (1st Floor RH from inside)

CLIENT'S APPROVAL :

CLIENT - SEZ BIOTECH

PROJECT -

SITE LOCATION - PUNE

DWG. NO. : NIHVA/21-22/MFG/046

SCALE: NTS	WT:	SHEET:1 OF 1

DRAWN BY: G.P.	DATE: 29-03-2022
CHECKED BY: P.J.	DATE: 29-03-2022
APPROVED BY : A.K.	DATE: 29-03-2022

If any queries contact : design@nihva.com

NOTE: ALL DIMENSIONS ARE IN mm

THIS DRAWING & DESIGN IS THE PROPERTY OF NIHVA TECHNOLOGIES. NOT TO BE SOLD OR COPIED TO ANY OTHER CONCERN.