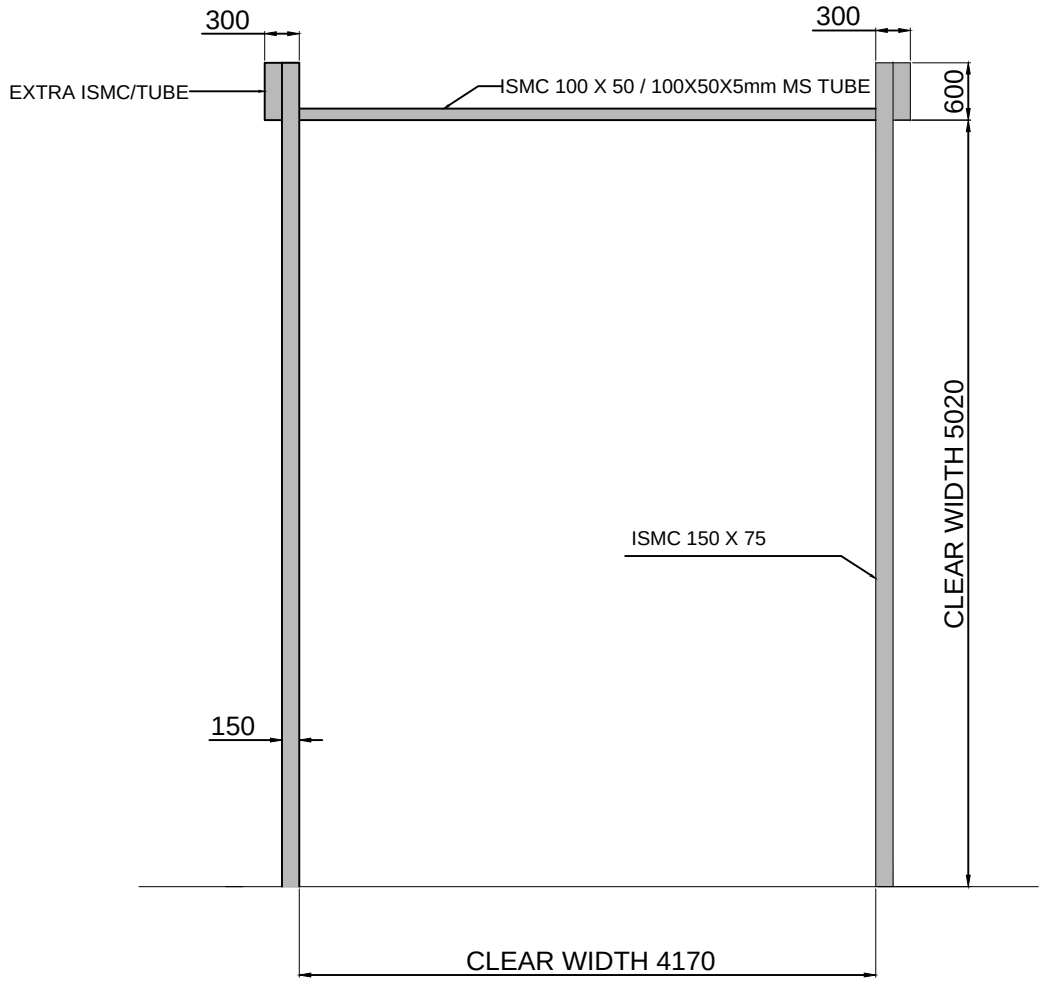


1. ISMC 150 X 75 X 12.45 MTR = 204.18 KGS
2. ISMC 100 X 50 X 4.17 MTR = 38.36 KGS

TOTAL WEIGHT = 242.54 KGS

CLEAR WIDTH	CLEAR HEIGHT	QUANTITY
4170	5020	02

TOLERANCE - ±10mm & 15 kgs

NOTE :
1. MATERIAL FOR ALL STRUCTURE = M.S

This drawing & design is the property of NIHVA TECHNOLOGIES. Not to be sold or copied to any other concern.

TITLE
STRUCTURE FOR GEAR OPERATED ROLLING SHUTTER

NIHVA TECHNOLOGIES PVT. LTD.

NIHVA TECHNOLOGIES PVT. LTD. PUNE
Tel : 020 66304033
Email:- info@nihva.com
Website:- www.nihva.com

	NAME	SIGN	DATE
DRAWN	PRADEEP		12-07-2018
CHECK	PRADEEP		12-07-2018
APPRD.	R.D		12-07-2018

CLIENT - SYNERGY
PROJECT-EMBASSY INDUSTRIAL PARKS PVT. LTD.
SITE LOCATION - CHAKAN
If any queries contact : design@nihva.com
DWG. NO. : NIHVA/17-18/0082
REV- 00
ALL DIMENSION ARE IN mm
SCALE: NTS
WT:
SHEET: 01 OF 01