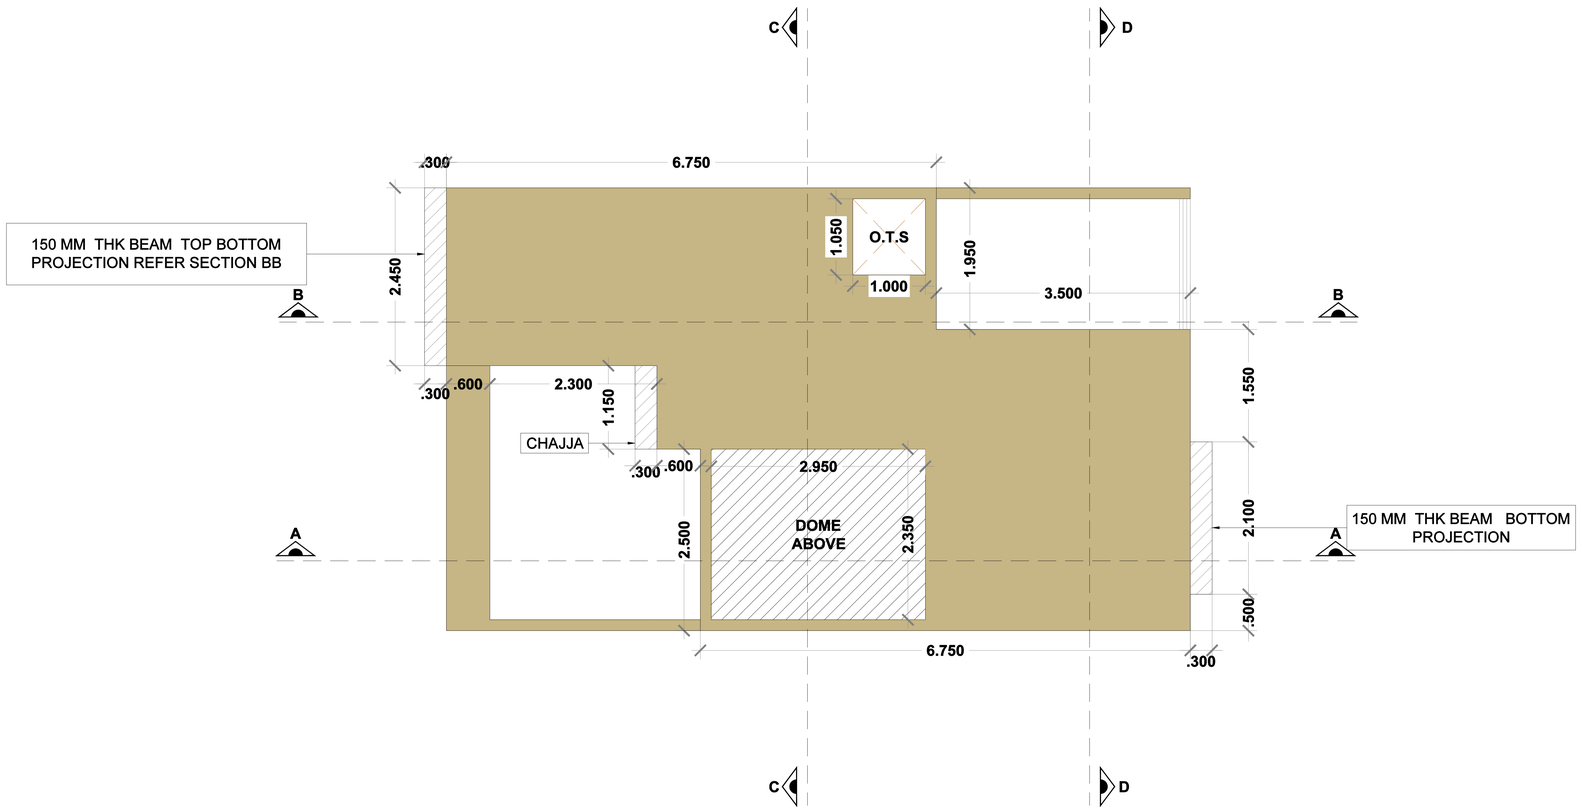


STAMP OF APPROVAL

REVISIONS :

NO	DATE	DESCRIPTION
01	DD/MM/YY	1)
02	DD/MM/YY	1)
03	DD/MM/YY	1)
04	DD/MM/YY	1)

SCHEDULE OF OPENINGS

DOOR	SIZE	LINTEL LEVEL
D	1.20 X 2.45	2.45 M
D1	1.00X 2.45	2.45 M
D2	0.75X 2.45	2.45 M
SD	3.50 X 2.30	2.45 M

SCHEDULE OF WINDOWS

WINDOW	SIZE	LINTEL LEVEL	SILL LEVEL
W	2.00 X 2.45	2.45 M	0.00 M
W1	1.80 X 1.70	2.45 M	0.75 M
W2	1.80 X 1.25	2.45 M	1.20 M
W3	1.00 X 1.70	2.45 M	0.00 M
V	0.60 X 0.90	2.45 M	1.55 M

PROJECT :

PROPOSED RESIDENTIAL BUNGALOW FOR MR.SRIKANTH KOMMA
AT - GODREJ WOODS MAMURDI, TALUKA - HAVELI, DISTRICT - PUNE

TITLE : ROOF PLAN

NORTH

Client Name	MR.SRIKANTH KOMMA
Project Co-Ordinator	

SCALE	DWG. NO.	JOB NO	DATE	REVISION
1 : 100	001	0001	18.05.2024	R.001

NOTES :

- Do not scale this drawing.
- All dimensions shall be verified on site before proceeding with work.
- All dimensions are in millimeter unless noted otherwise.
- All room dimensions are unfinished dimension.
- Any discrepancy found in this drawing to be brought to the immediate notice of Architects by Project Manager/ Contractor before execution.
- T.O.C.=Top of concrete,T.O.F.=Top Of Finish, C/C.=Centre to Centre,O/O.=Out to Out.
- All the levels specified are T.O.C. unless otherwise specified.
- This drawing to be read in conjunction with structural, MEP and other consultant's drawing.
- For all R.C.C.sizes,design & details refer to R.C.C. Consultant's drawing.
- The sizes given for doors/windows and openings are clear masonry/R.C.C. opening sizes.
- All sleeves shown are indicative,for all service details, sleeves invert level & cutout in slab refer service consultant's drawing or coordinate with coordination department.
- All external terraces,dry balconies horizontal surface to be water proofed and sloped as per RWP position.
- Architect shall not be responsible in any manner if there are any deviations on site w.r.t. this drawing without the written permission from Architect.
- Architect shall not be responsible in any manner for the centering, shuttering and scaffolding erected on the site for any purpose.
- Any additional excavation/provision required for the purpose of soling, water proofing, compacting the murum, casting of the raft shall be as per the drawings and details given by the R.C.C. consultant.water proofing consultant/agencies.
- Architect shall not be responsible for any damages caused due to any reasons arising out of 'Specialized Consultant's deficient services with regard to design and supervision of the work entrusted to them,who were appointed/engaged in construction with the developer.
- The Project Manager to procure shop drawings for all fabricationitems/elements like grills, railing, canopies, top terrace elevation features, pergolas, gate feature, facade elements, louvers etc.and get it approved from structural/specialized consultant before execution of the same on site.
- Architect shall not be responsible in any manner for the labours hired, use of materials (type & grade) on site by the owner or third party.
- This drawing should not be used for execution on site unless it is mentioned as GFC & signed by the project architect.

205, 'A' Square Building, Plot No.34, ADC, Sect.26, Nigdi, Pradhikran, Pune -411044

Architecture | Interior | Landscape | Urban Design | Planning

arc

Solutions

+91 7741 00 00 31 | +91 7741 90 00 32 | +91 7720 08 38 82