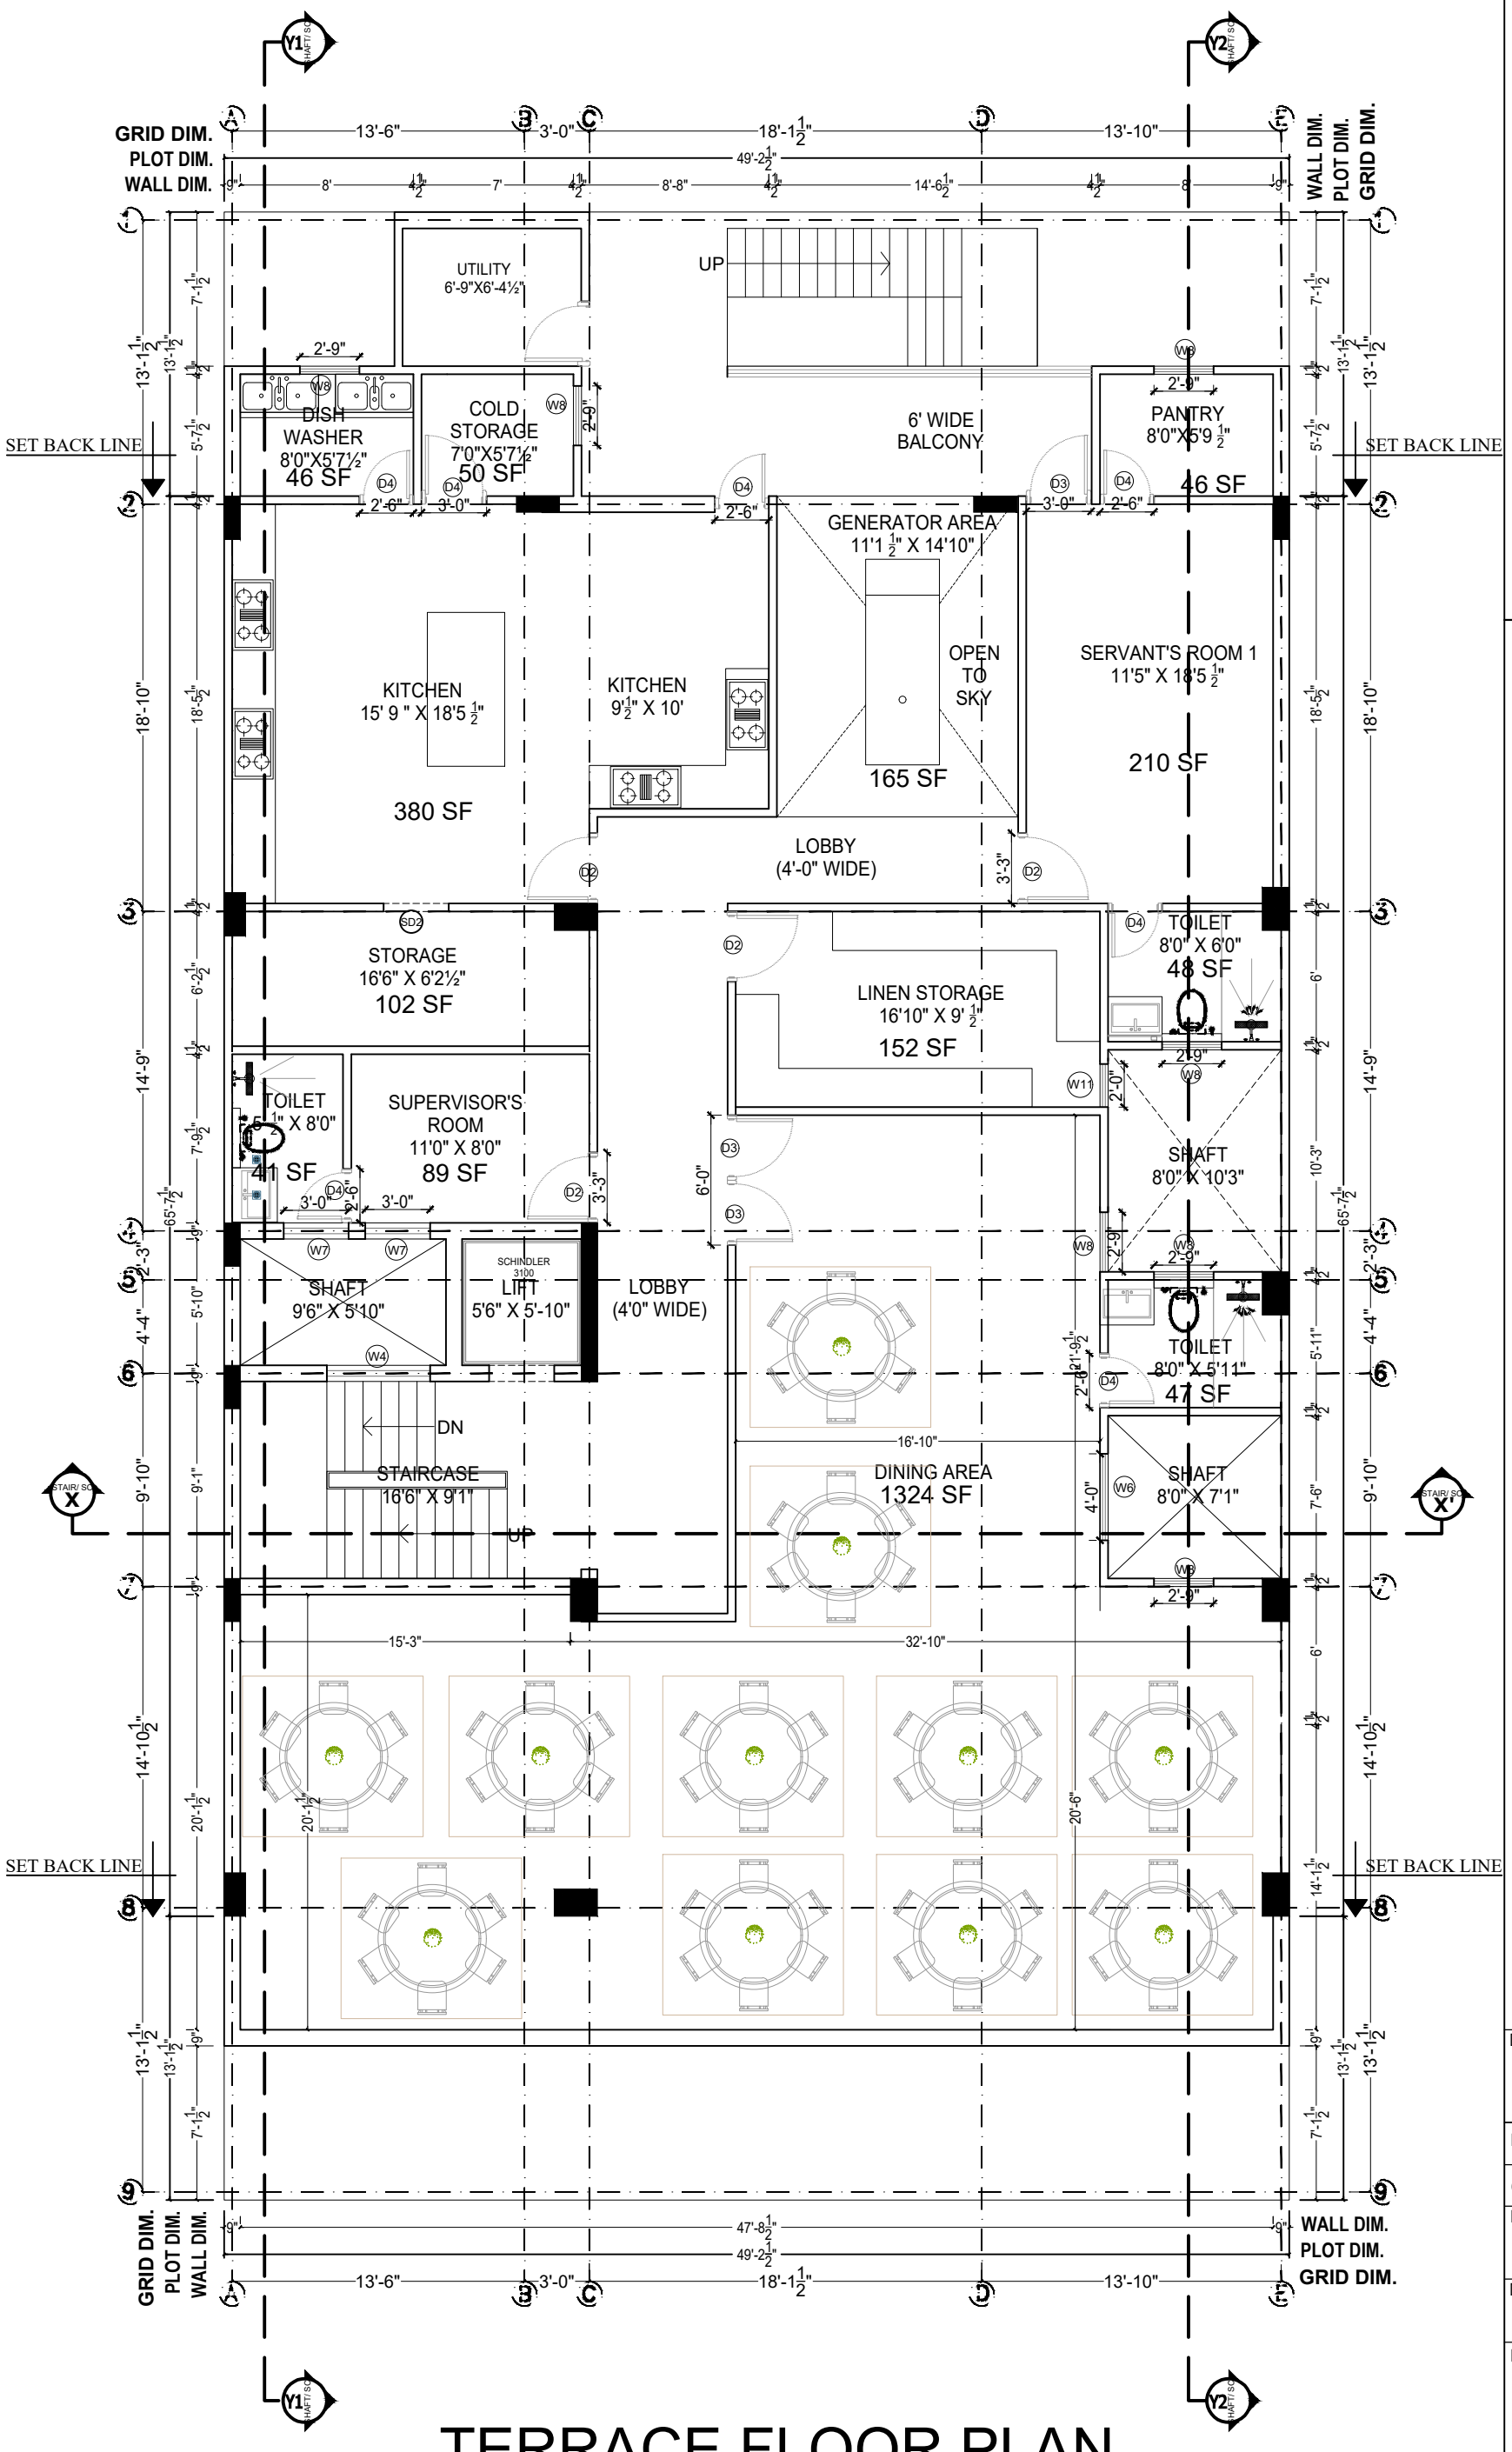


TERRACE FLOOR PLAN

Project Name:
MR. GAGAN GOURI
Plot:- 2425 P, Sector 57, Gurgaon

NOTES:-

ALL DIMENSIONS TO BE READ NOT TO BE SCALED.

ALL DIMENSIONS ARE IN INCH. EXCEPT OTHERWISE MENTIONED.

THIS DRAWING SUPERCEDES ALL OTHER PREVIOUS DRAWING.

THIS DRAWING SHOULD BE READ IN CONJUCTION WITH RELEVANT STRUCTURE DRAWING & ANY DISCRIPANCY NOTICED SHOULD BE GOT CLARIFIED BEFORE EXECUTION.

ANY AMBIGUITY IN THE DRAWING MUST
BE BROUGHT TO THE ARCHITECT'S NOTICE BEFORE THE COMMENCEMENT OF REVELENT ITEMS OF WORK.

THIS DRAWING IS THE PROPERTY OF DREAM SPACE AND NOT TO BE COPYIED OR USED IN ANY MANNER WITHOUT THEIR PERMISSION.

Drawing Name :
TERRACE FLOOR PLAN

DRAWN	Rajeev
CHECKED	Ar. Ankur Tulsyan
Date : 09/03/2020	Revision No : R-0 Revision Date :

Drawing Status : Final Architecture

F.I.O. ☐ Tender ☐ G.F.C. ☐

PRINCIPAL ARCHITECT :
DREAM SPACE
ARCHITECTS AND INTERIOR DESIGNERS
C 226, SUSHANT SHOPPING ARCADE, SUSHANT LOK 1
GURGAON, HARYANA. MOB: 78385-38599
TEL: 0124-4078295, WEB: WWW.DS-DESIGN.IN