

DWG.No.
PUS404_EX_ARCH_MP_GTDT_00 R0

RELEASE FOR EXECUTION

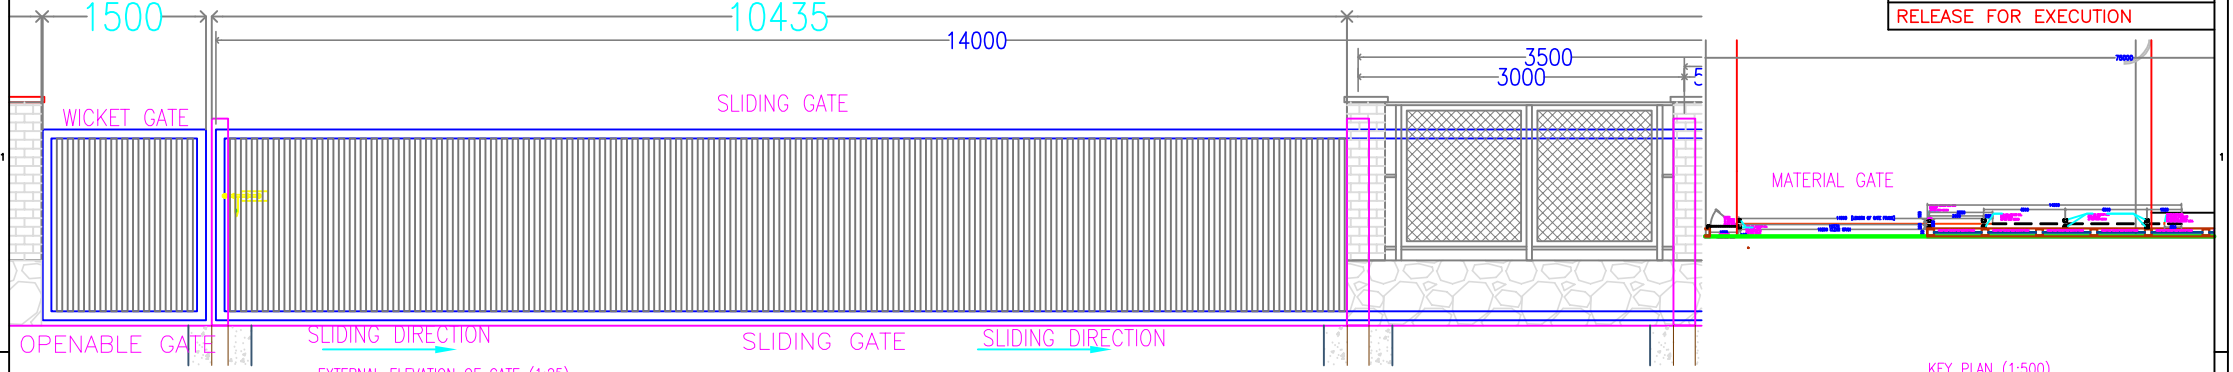



EXTERNAL ELEVATION OF GATE (1:25)

KEY PLAN (1:500)

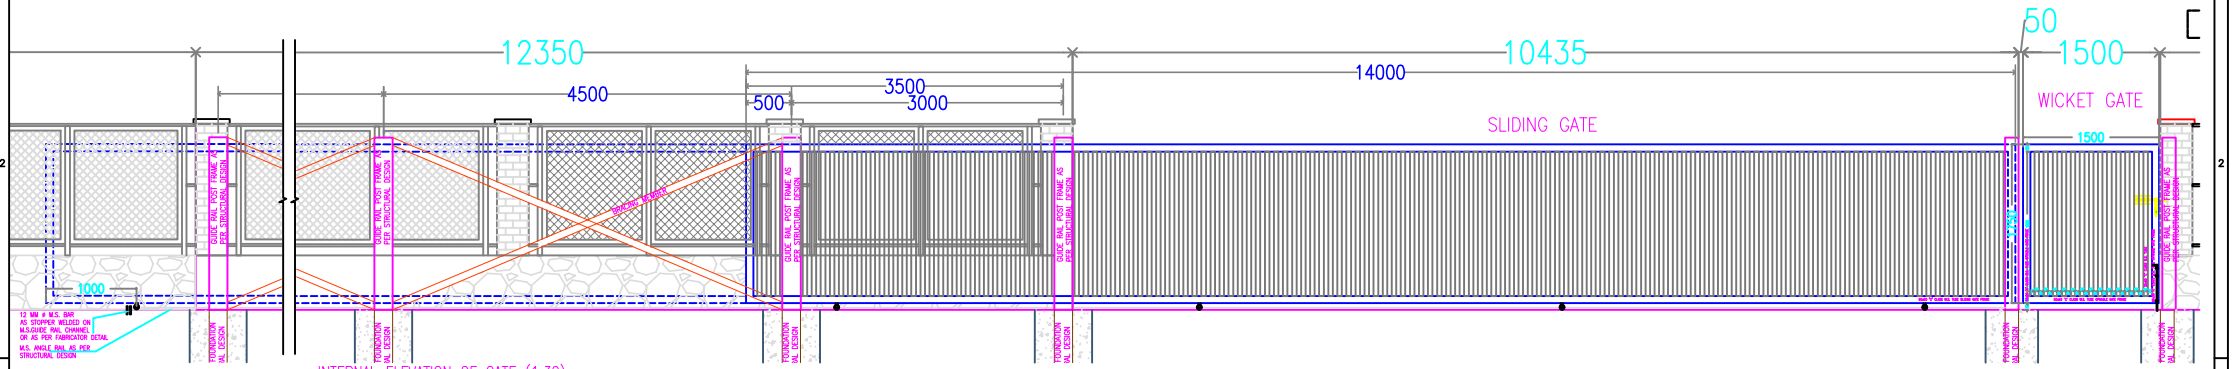

INTERNAL ELEVATION OF GATE (1:30)

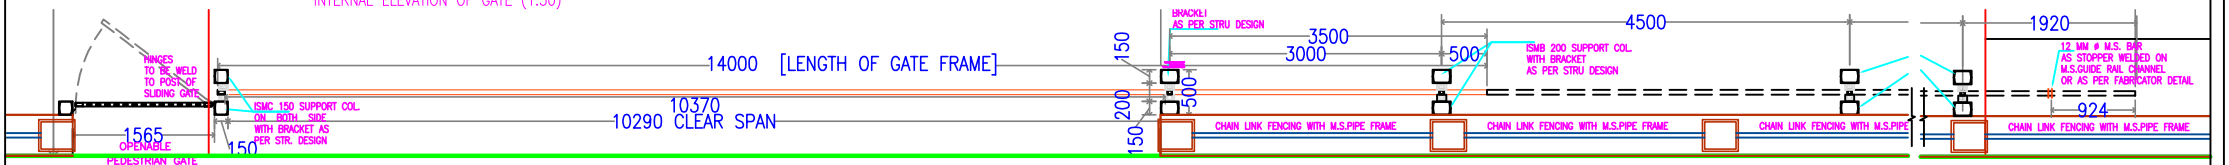

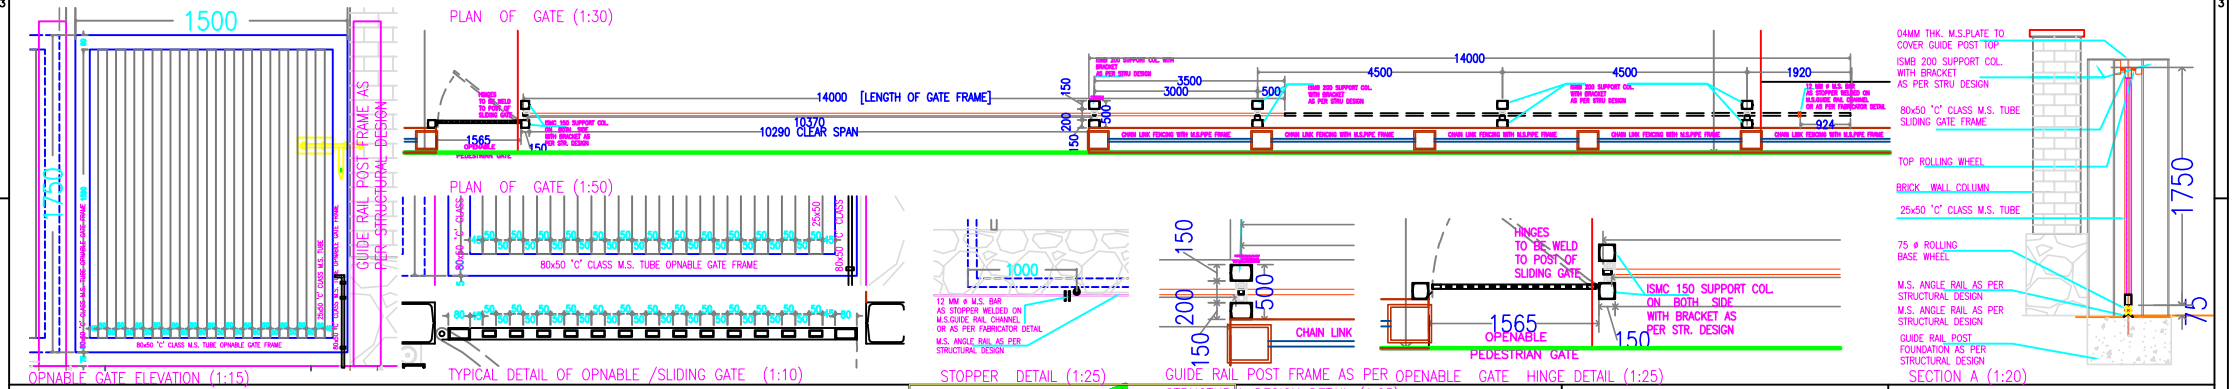

OPNABLE GATE ELEVATION (1:15)

TYPICAL DETAIL OF OPNABLE /SLIDING GATE (1:10)

STOPPER DETAIL (1:25)


GUIDE RAIL POST FRAME AS PER OPENABLE GATE HINGE DETAIL (1:25)

SECTION A (1:20)

GUIDE RAIL POST FRAME AS PER STRUCTURAL DESIGN DETAIL (1:25)

REVISIONS :

NO.	DATE	REMARKS
RO	.....	.....
NO.	DATE	REMARKS

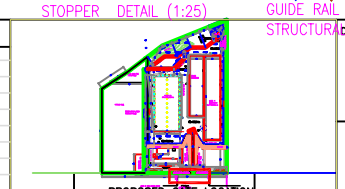

PROJECT KEY PLAN

CLIENT SIGN

CLIENT:
PUSH ENGINEERING PVT.LTD.
PROPOSED INDUSTRIAL BUILDING AT PLOT NO. B16,KHANDALA, PHASE- 2 MIDC ,DIST-SATARA.

JOB NO :	PUS404	DRAWN BY :	D.DESHPANDE
SCALE :	1:30	CHECKED BY :	D.DESHPANDE
DATE :	01.01.22	APPROVED BY :	

NOTES :
1) ONLY WRITTEN DIMENSIONS ARE TO BE FOLLOWED.
2) READ THIS DRAWING ALONG WITH THE RELEVANT DEPT. DRAWING.
3) ANY AMBIGUITY IN THIS DRAWING TO BE REFERED TO THE CONSULTANT BEFORE EXECUTION OF THE WORK
4) ALL DIMENSIONS ARE IN mm

TITLE:
GATE DETAIL

DWG.No.
PUS404_EX_ARCH_MP_GTDT_00 R0

ARCHIVISTA
ENGINEERING PROJECTS PVT.LTD.
Office No.201&202,Sai Empire, Baner, PUNE-411045,MAHARASHTRA,INDIA.
PH.91-20-66284444,6400
www.archivistaindia.com