
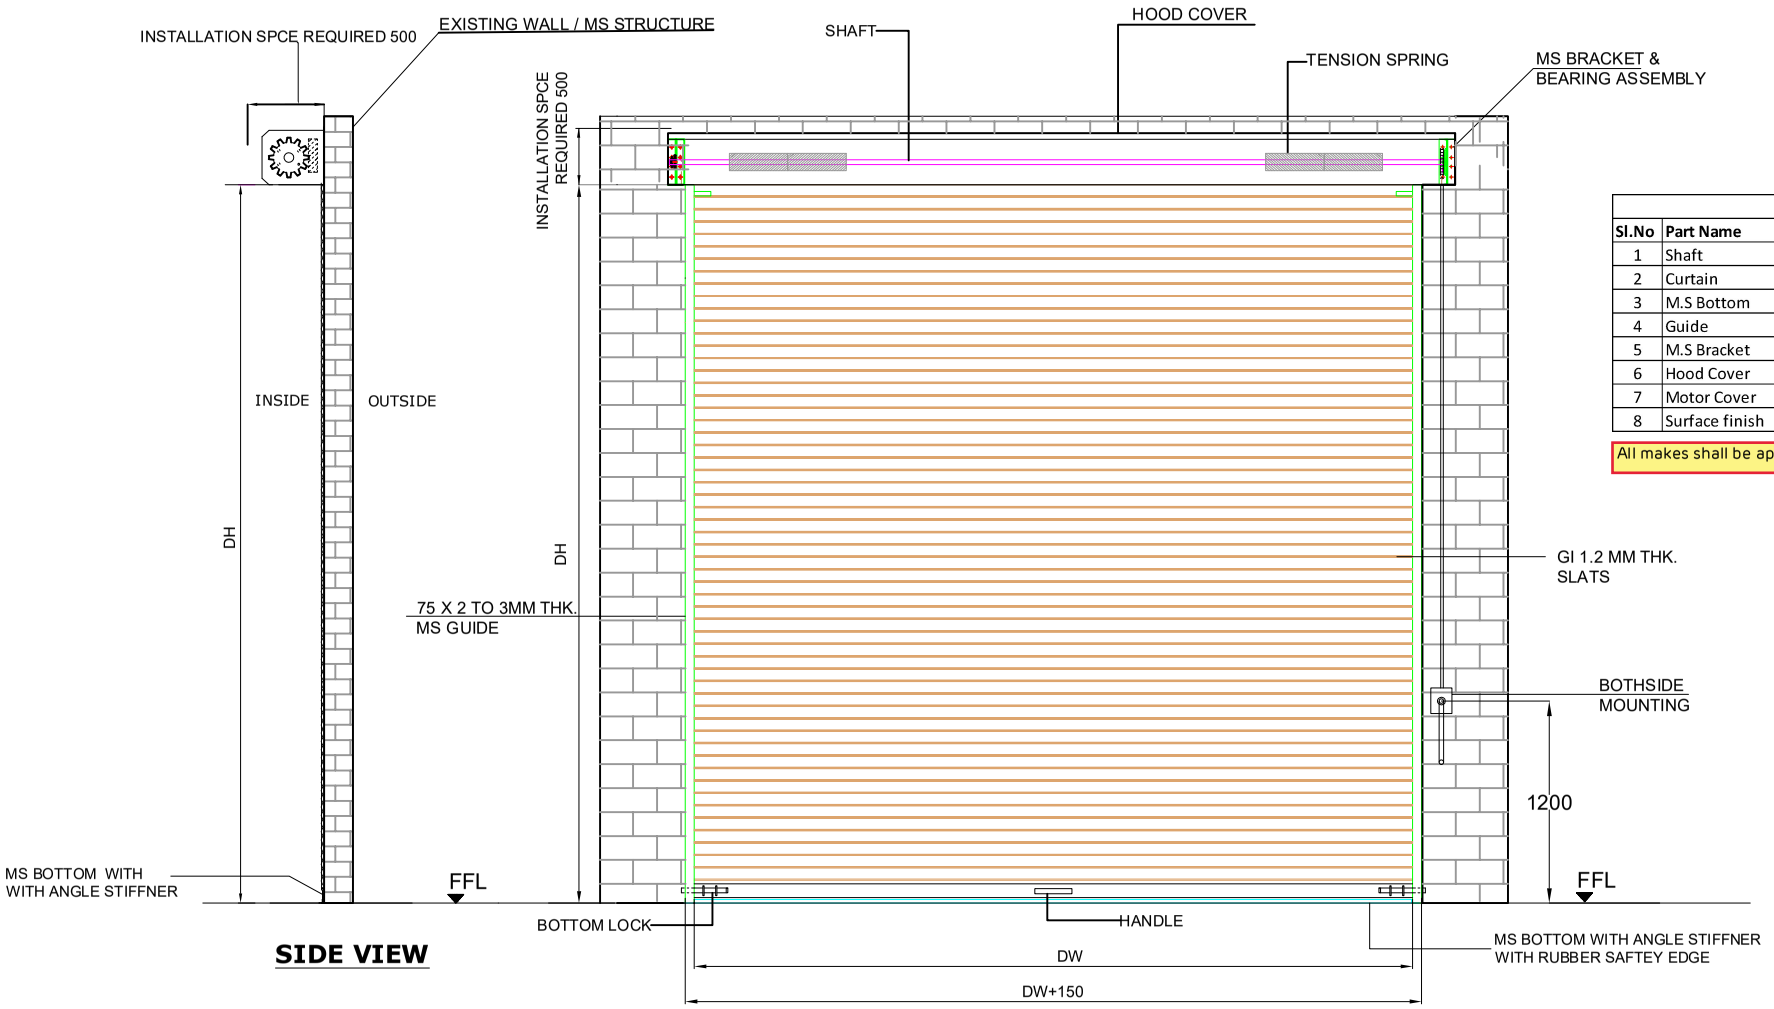


SIDE VIEW


Technical Data		
Sl.No	Part Name	Description
1	Shaft	Minimum 150DN(165OD) as per IS 1239
2	Curtain	1.2mm approx 350Mpa for GI
3	M.S Bottom	2.5mm thickness
4	Guide	75 X 2 to 3mm thickness
5	M.S Bracket	400X400X5 NIHVA make IS 2062
6	Hood Cover	0.9 to 1.2mm with NIHVA make
7	Motor Cover	0.9 to 1.2mm with NIHVA make
8	Surface finish	Powder coating

All makes shall be approved by our Quality Department.

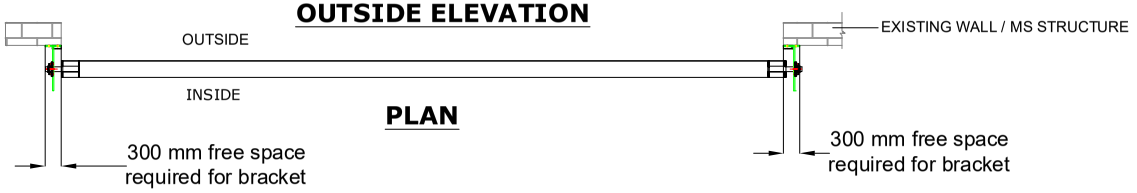

OUTSIDE ELEVATION

PLAN

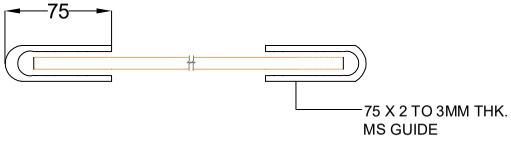

Colour Shall be match with side cladding.

RAL CODE	SHADE	COLOUR
RAL 9001	CREAM	
RAL 5002	ULTRAMARINE BLUE	
RAL 7035	LIGHT GREY	
RAL 7001	SILVER GREY	

NOTE:-

1. ALL DIMENSION ARE IN MM
2. SURFACE FINISH: POWDER COATING OF APPROVED RAL CODE
3. MOUNTING: ON CONCRETE COLUMN/WALL OR MS STRUCTURE, KINDLY CONFIRM
4. IF MS STRUCTURE REQUIRED WILL BE IN SHREE PRE FAB STEEL PVT LTD SCOPE
5. KINDLY CONFIRM INSIDE OR OUTSIDE MOUNTING Inside Mounting

Shall be fixed on structural frame. Frame shall be as per requirement and shall be supplied by M/s Shree Pre Fab SPL

REV.NO	REVISION	DATE	REVISED BY

CLEAR WIDTH (DW)	CLEAR HEIGHT (DH)	QTY
4000	4000	3NOs

This drawing & designing is the property of NIHVA TECHNOLOGIES. Not to be sold or copied to any other concern.

TITLE :-
GEAR OPERATED ROLLING SHUTTER

	NAME	DATE
DRAWN	SUJATA.B	11/01/2022
CHECK	A.K	11/01/2022
APPROVAL	V.T	11/01/2022

NIHVA TECHNOLOGIES PVT. LTD.
NIHVA TECHNOLOGIES PVT. LTD. PUNE
Tel : 020 66304033
Email:- info@nihva.com
Website:- www.nihva.com

CLIENT - SHREE PRE FAB STEEL PVT LTD

PROJECT -ROLLING SHUTTER

DWG. NO. : NIHVA/22-23/CLT/0176 | REV-00

If any queries contact : design@nihva.com | SCALE: NTS | WT: | SHEET: 01 OF 01

ALL DIMENSION ARE IN mm