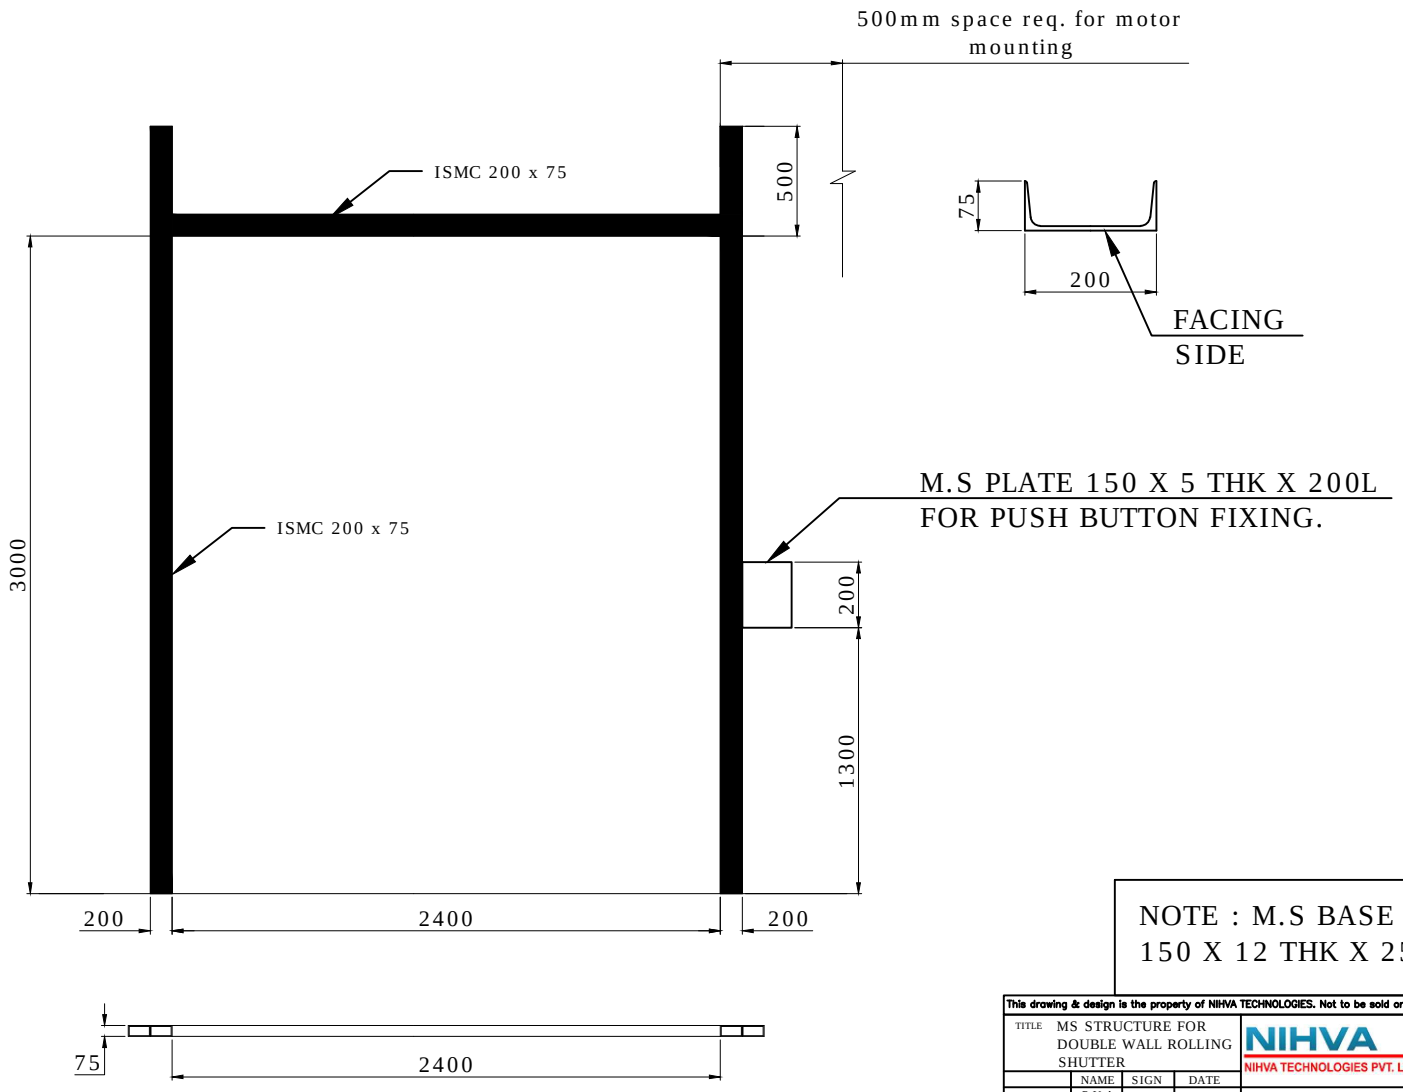

NOTE : M.S BASE PLATE 150 X 12 THK X 250L = 2 NOS

ALL STRUCTURAL DIMENSIONS SHOWN ARE MINIMUM REQUIREMENT.

This drawing & design is the property of NIHVA TECHNOLOGIES. Not to be sold or copied to any other concern.

TITLE	MS STRUCTURE FOR DOUBLE WALL ROLLING SHUTTER	NIHVA TECHNOLOGIES PVT. LTD.	NIHVA TECHNOLOGIES PVT. LTD. PUNE Tel : 020 66304033 Email:- info@nihva.com Website:- www.nihva.com
	NAME / SIGN / DATE		
DRAWN	P.V.A / / 28.02.19	CLIENT - RELIANCE	
CHECK	V.M.T / / 28.02.19	PROJECT -	
APPROVAL	/ /	SITE - NILAKOTTAI, TAMILNADU.	
If any queries contact :design@nihva.com		DWG. NO. : NIHVA/18-19/0281	REV- 1
ALL DIMENSION ARE IN mm		SCALE: NTS / WT:	SHEET: 01 OF 01