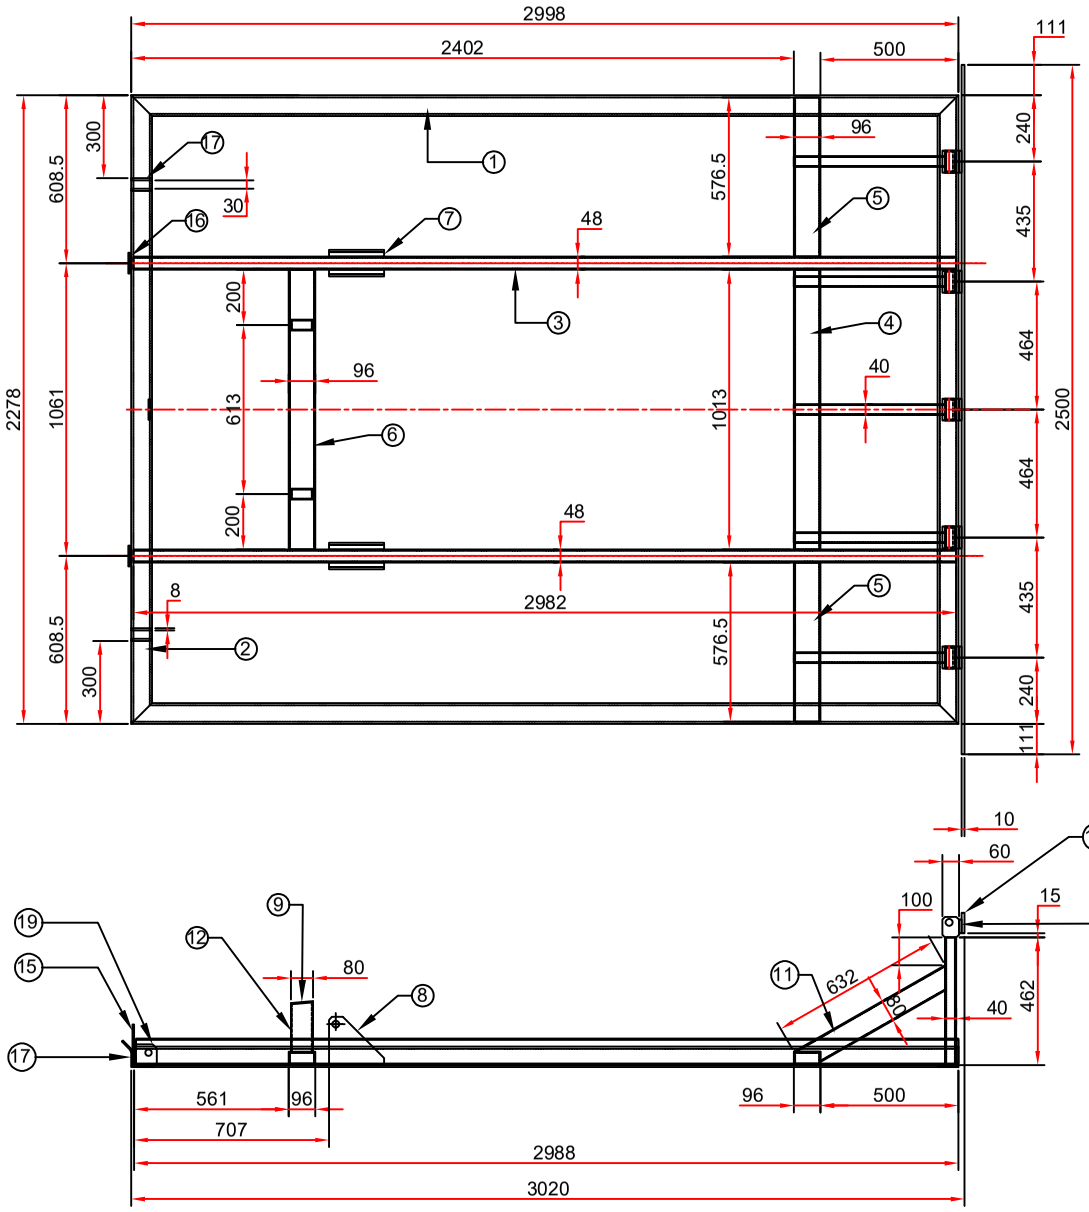


BOM			
SL NO.	DESCRIPTION	SPECIFICATION	QTY
1	ISA	75X75X8X2998	2NOS
2	ISA	75X75X8X2278	2NOS
3	RECT. TUBE	96X48X4.8X2982	2NOS
4	RECT. TUBE	96X48X4.8X1013	1NO
5	RECT. TUBE	96X48X4.8X576.5	2NOS
6	RECT. TUBE	96X48X4.8X1013	1NO
7	MS FLAT	75X16X200L	4NOS
8	CYLINEDER MTNG BKT	175X8X200L	4NOS
9	MS FLAT	50X5X100L	2NOS
10	RECT.TUBE	80X40X4X462	5NOS
11	RECT.TUBE	80X404X632	5NOS
12	RECT.TUBE	96x48X4.8X183	2NOS
13	MS BLOCK(DECK HLDNG BKT)	75X60X85	5NOS
14	MS FLAT	75X10X2500	1NO
15	MS FLAT	75X5X155	1NO
16	MS FLAT	50X5X75	2NOS
17	MS FLAT	75X5X185	2NOS
18	MS FLAT	50X10X100	5NOS
19	STOPPER BRACKET	75X5X8	4NOS
20	SQ TUBE	25X25X3X740	2NOS
21	MS ANGLE	75X75X8X30L	2NOS

This drawing & design is the property of NIHVA TECHNOLOGIES. Not to be sold or copied to any other concern.

TITLE:- BASE FRAME

NIHVA TECHNOLOGIES PVT. LTD.

	NAME	DATE	SIGN
DRAWN	SUJATA	11/02/2023	
CHECK	A.K	11/02/2023	
APPRD.	V.T	11/02/2023	

If any queries contact : design1@nihva.com

ALL DIMENSION ARE IN mm

CLIENT - Aegis Infrasolutions(India) Pvt Ltd

LOCATION - Pune

PRODUCT - Dock leveler

DWG NO:-NIHVA/22-23/MFG/0110 REV- 0

SCALE: NTS SCALE:-- 1:1 SHEET: 01 OF 01

Rev No.	Revision	Date	Revised By