
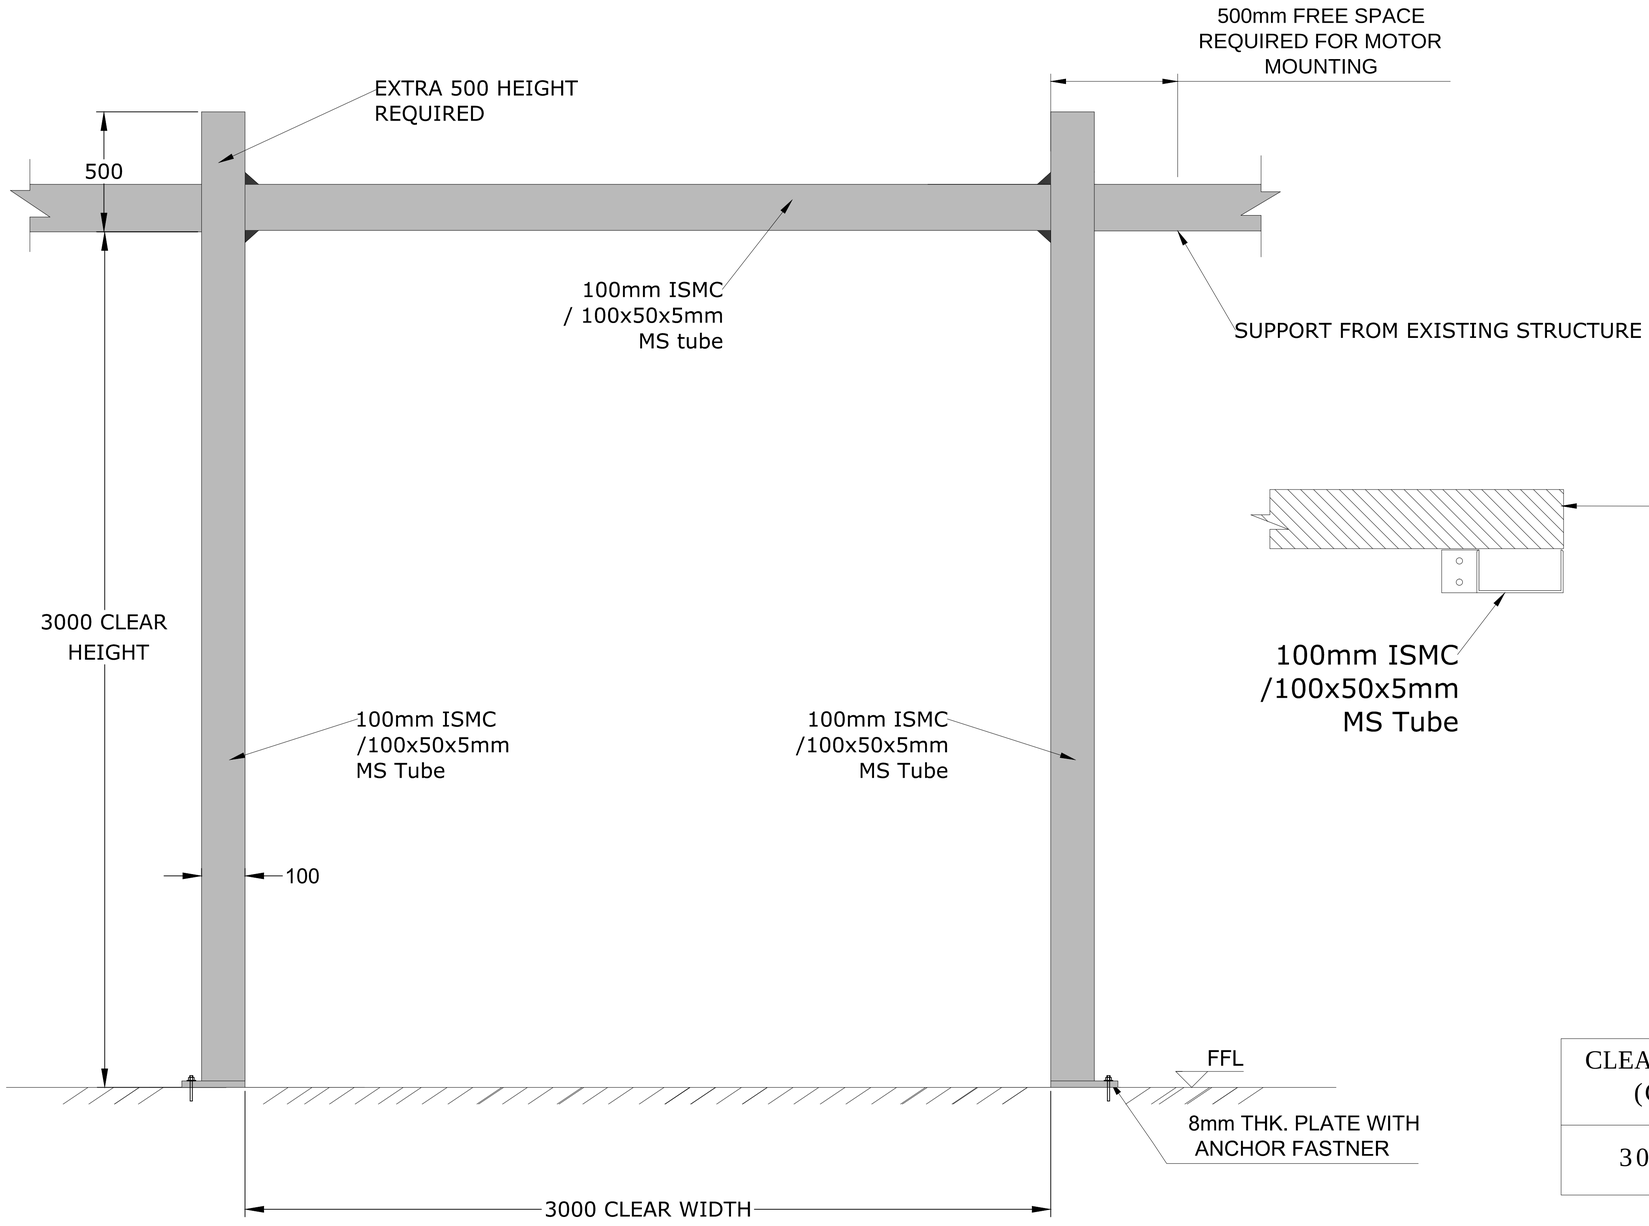


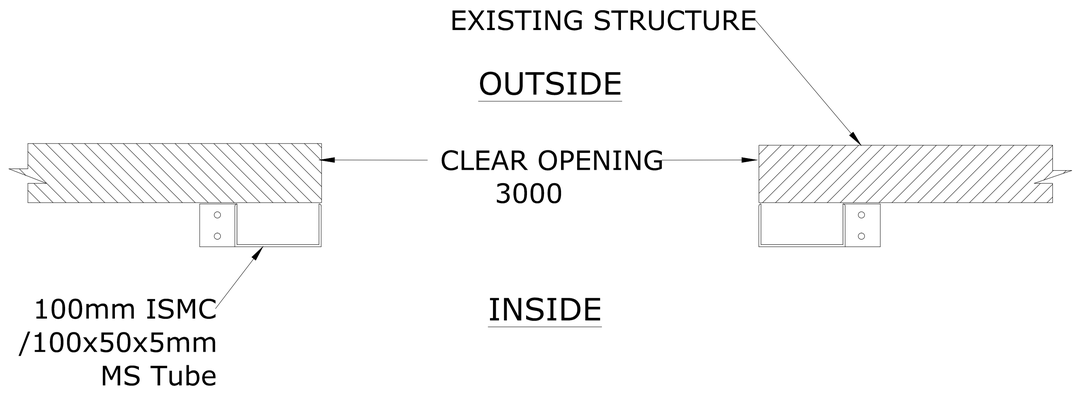

PLAN

CLEAR WIDTH (CW)	CLEAR HEIGHT (CH)
3000	3000

This drawing & design is the property of NIHVA TECHNOLOGIES. Not be sold or copy to any other concern.

TITLE

STRUCTURE FOR HIGH SPEED DOOR (RR 300 S)

CLIENT APPROVAL

ALL DIMENSION ARE IN mm

	SIGN	DATE
DRAWN	OMKAR	12/06/17
CHECK	S.S.	12/06/17
ENG		
APPRD.	S.S.	12/06/17
MFG		
Ref. No.		

NIHVA TECHNOLOGIES PVT. LTD.

NIHVA TECHNOLOGIES PVT. LTD. PUNE
Tel : 020 66304033
Email:- info@nihva.com
Website:- www.nihva.com

CLIENT - MARS INTERNATIONALS

PROJECT-

SITE - KHED CITY,Pune

DWG. NO. - NIHVA/17-18/0101

SCALE: NTS | WT: | SHEET: 01

If any queries contact : projects@nihva.com