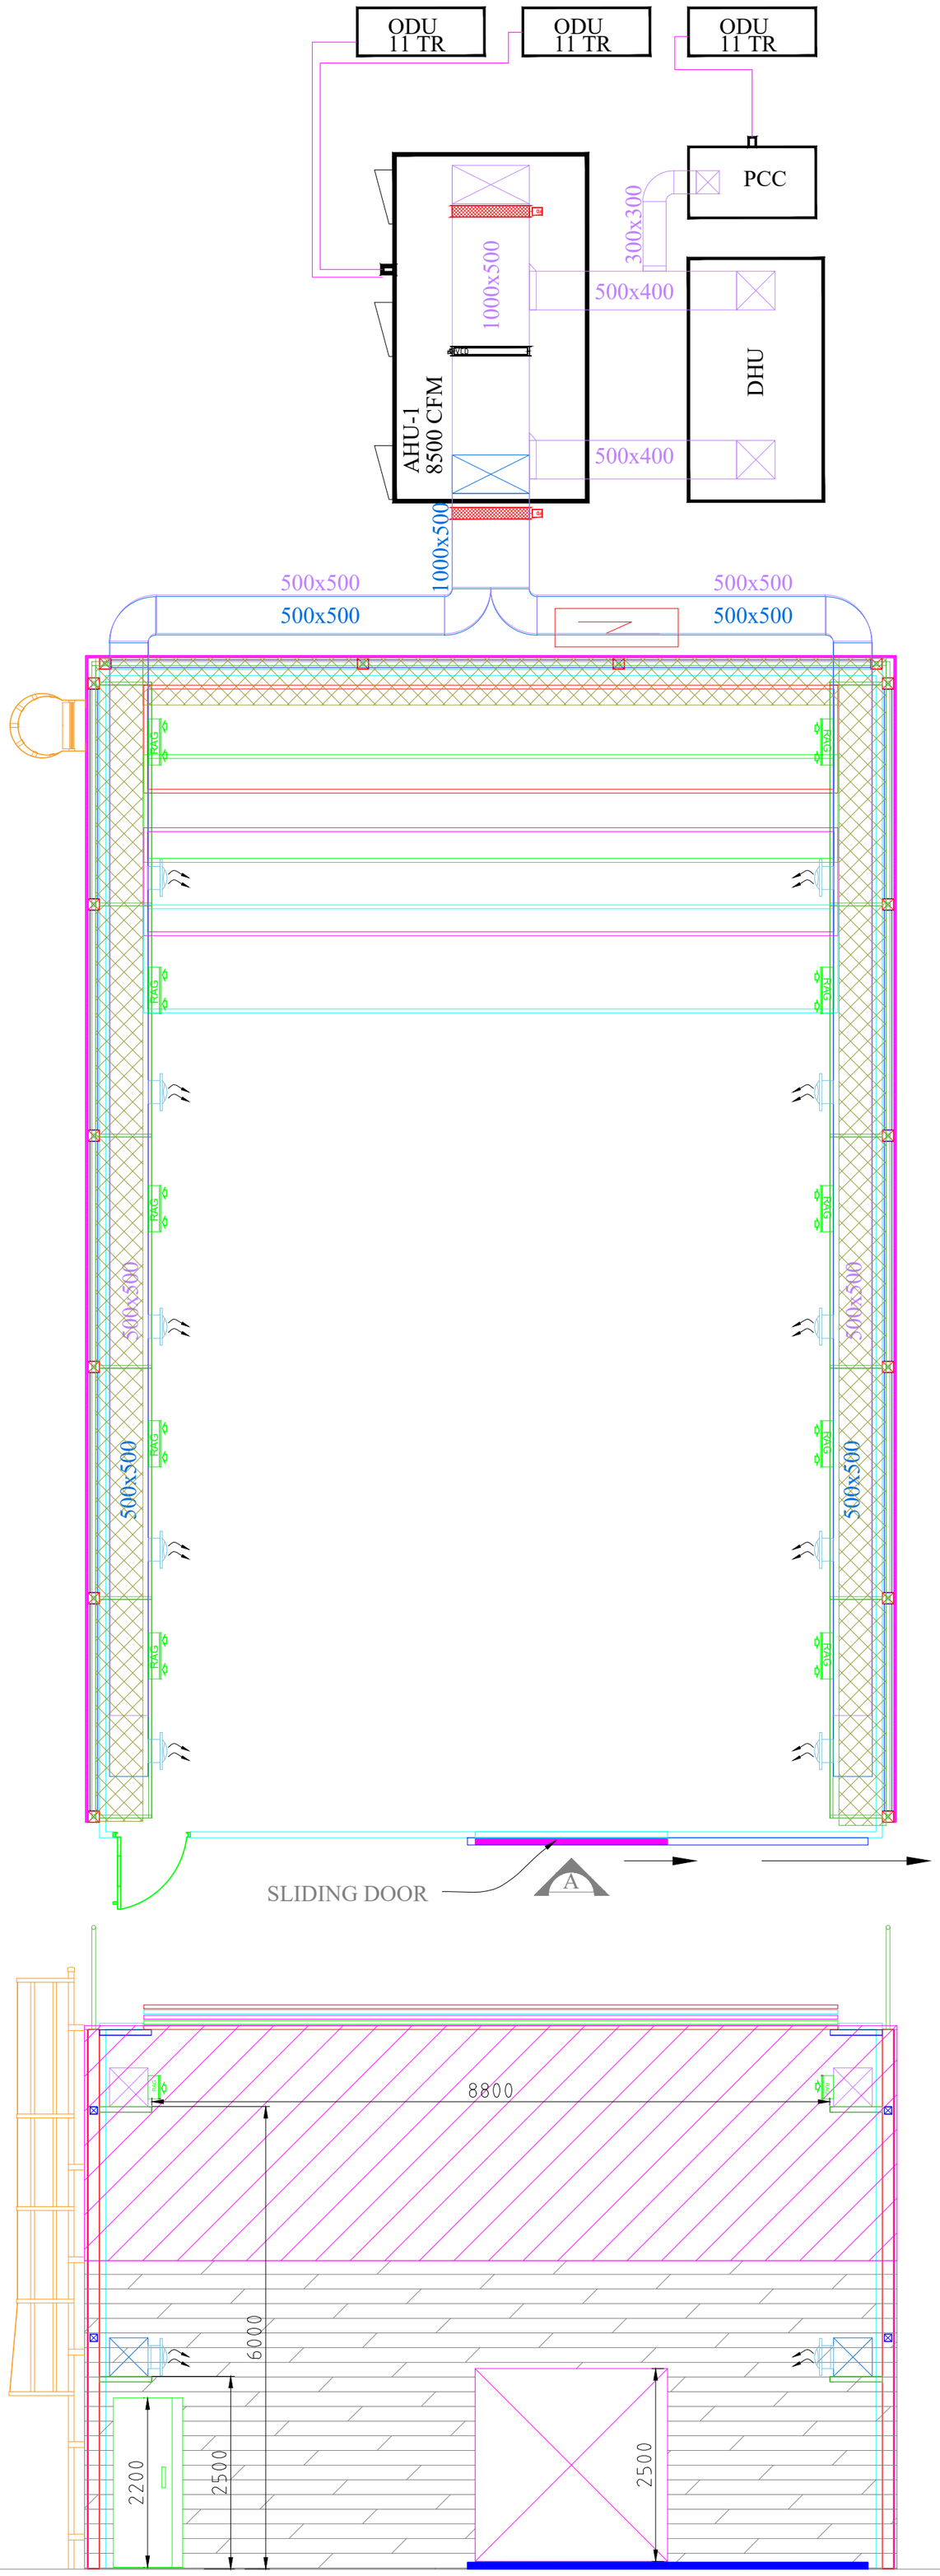


ELEVATION -A

GRILLE		SIZE IN MM LENGTH x WIDTH
SUPPLY	RETURN	
SAG	RAG	600 x 300

JET NOZZLE	SIZE IN MM
	Ø300

HVAC CONTRACTOR :

INTEGRATED COOLING SOLUTIONS PVT. LTD.

E-193/1 SHAHEEN BAGH JAMIA NAGAR NEW DELHI-110025
EMAIL :- icoolprojects@gmail.com

TITLE: DUCTING LAYOUT			
SCALE	SHEET-A1	ISO - 1:125	REFERENCE NO. ICS- ----------
DRAWN	V.S		DRAWING NO. ICS- ---------- / REV. R-0
CHECKED	I.K		