

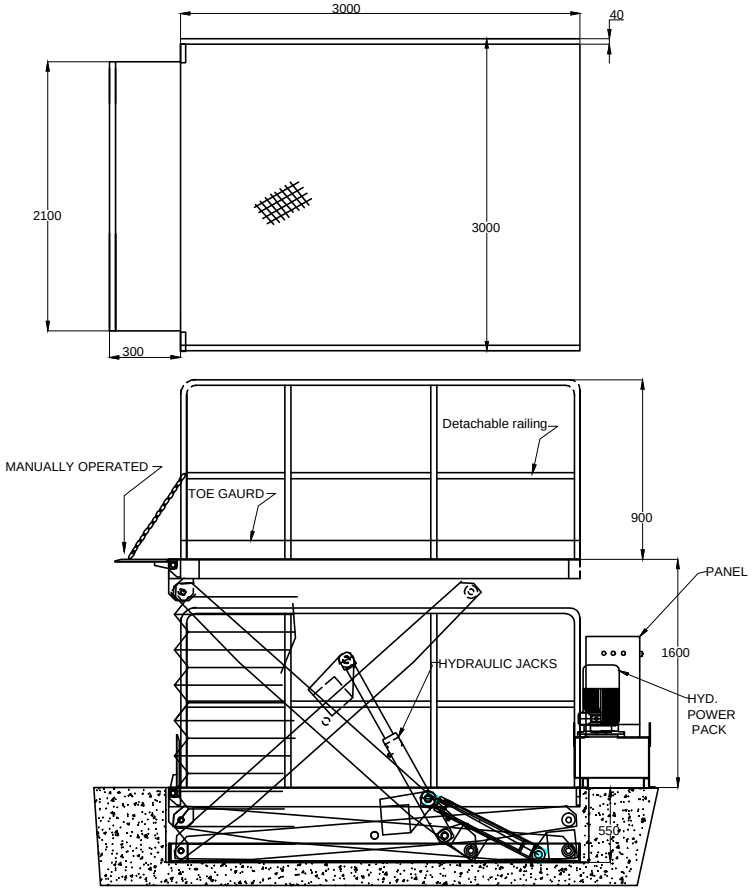


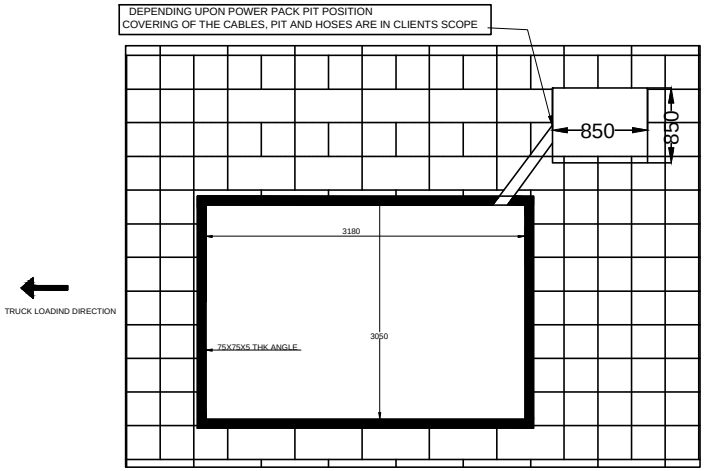

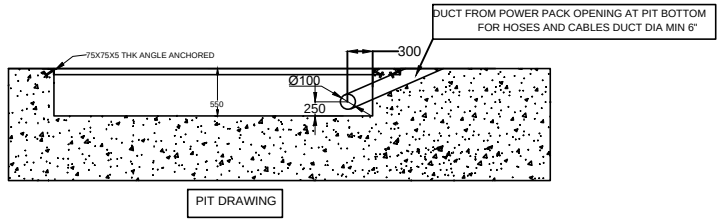

SPECIFICATIONS	
RATED CAPACITY	3 TON
PLATFORM LENGTH	3000 mm
PLATFORM WIDTH	3000 mm
OVERALL LENGTH	3150 mm
OVERALL WIDTH	3000 mm
LIP	MANUAL , ONE SIDE
LIP SIZE	350 X 2100
SAFETY BELLOW	PROVIDED
CLOSE HEIGHT	550 mm
LIFT HEIGHT	1600 mm
POWERPACK MOTOR	3 PHASE AC, 5 HP
PENDANT	1 NO
LIFT & LOWER CUT-OFF	YES
STATION ADJUSTABLE SWITCH	YES

NOTE :
1. PIT FOR SCISSOR LIFT HAS TO BE DIAGONALLY WITHIN 3-5 MM
2. BASE OF THE PIT HAS TO BE IN WATER LEVEL AND RIGHT ANGLE TO THE VERTICAL SIDE WALLS
3. REQUIRED ALL CIVIL WORK, CONDUIT & PIT WORK IN CLIENT SCOPE.
4. PROPER DRAINAGE SYSTEM SHOULD BE PROVIDED FOR THE PIT.

RAL CODE PAINT	RAL 1004 GOLDEN YELLOW	

This drawing & design is the property of NIHVA TECHNOLOGIES. Not to be sold or copied to any other concern.

TITLE PIT MOUNTED HYDRAULIC SCISOR LIFT

	NAME	SIGN	DATE
DRAWN	S.M.S.		18.11.2020
CHECK	S.M.S.		18.11.2020
APPRD.			

If any queries contact : projectsupport@nihva.com

ALL DIMENSION ARE IN mm

NIHVA TECHNOLOGIES PVT. LTD.
NIHVA TECHNOLOGIES PVT. LTD. PUNE
Tel : 020 66304033
Email:- info@nihva.com
Website:- www.nihva.com

CLIENT - ACCURATE INDUSTRIAL CONTROLS PVT LTD

PROJECT - ACCURATE INDUSTRIAL CONTROLS PVT LTD

SITE LOCATION - PUNE

DWG. NO. : NIHVA/20-21/0090 | REV- R00

SCALE: NTS | WT: | SHEET: