


DOCK LEVELER SIZE	WIDTH (W)	LENGTH (L)	HEIGHT (H)	LIP (C) LENGTH	BUFFER SIZE (OPTIONAL)
	2000	2000	480	400	330X250X100


PIT DIMENSION	WIDTH (W 1)	LENGTH (L 1)	DEPTH (D)	ALL DIMENSIONS ARE IN mm
	2050	2080	490	

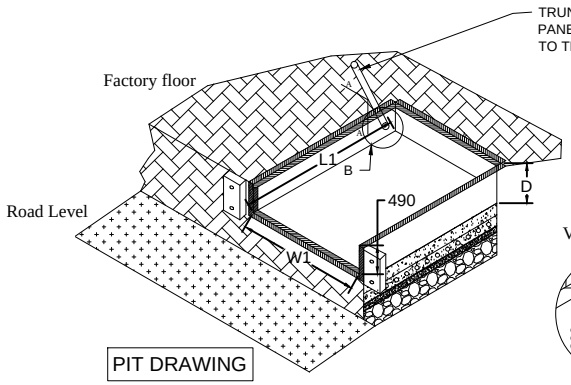

PIT DRAWING

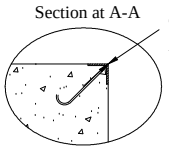


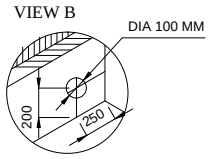

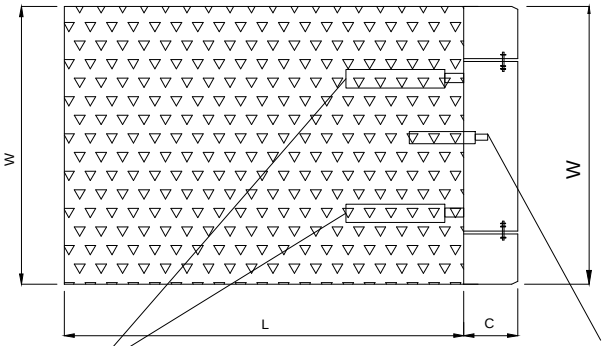

DECK CYLINDER 2 NOS

LIP CYLINDER 1 NOS

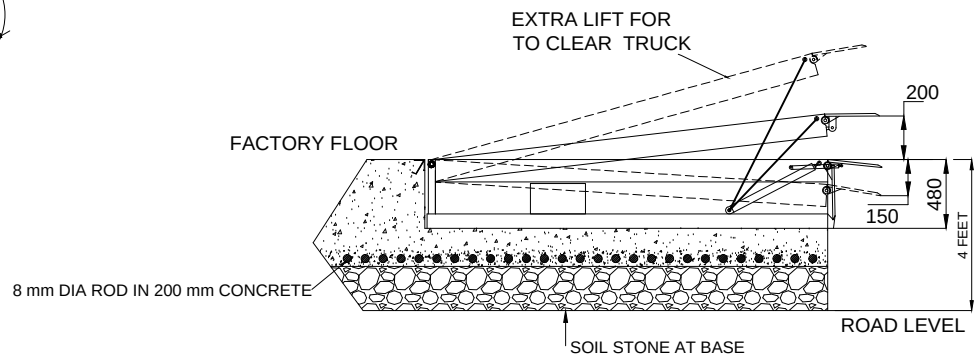

DOCK LEVELER- 3 TON CAPACITY

NOTE: -

1. PROPER DRAINAGE SHOULD BE DONE
2. TRENCH AS SHOWN SHOULD BE MADE BY DECIDING THE POWER PACK POSITION (SUPPLY CABLE LENGTH STD. 5000 MM)
3. LEVEL OF THE PIT SHOULD BE PLAIN AND SHOULD TAKE AT LEAST 10000 KGS FLOOR LOADING
4. MOUNTING ARRANGEMENT FOR BUMPERS SHOULD BE MADE AS PER BUMPER DRAWING (IF ORDERED)
5. FABRICATION TOLERANCE FOR PLATFROM SIZE WILL BE ± 15 MM

This drawing & design is the property of NIHVA TECHNOLOGIES. Not to be sold or copied to any other concern.

TITLE: DOCK LEVELLER

NIHVA TECHNOLOGIES PVT. LTD. PUNE
Tel : 020 66304093
Email:- info@nihva.com
Website:- www.nihva.com

	NAME	SIGN	DATE
DRAWN	P.A		26/02/18
CHECK	OMKAR		26/02/18
APPROVAL	SHEKHAR		26/02/18

CLIENT- PIONEER GROUP
PROJECT -
SITE -
DWG. NO. : NIHVA/17-18/0374
REV. - 0
SCALE: NTS
WT:
SHEET: 01 OF 01

If any queries contact : design@nihva.com

ALL DIMENSION ARE IN mm

QTY 01NOS