


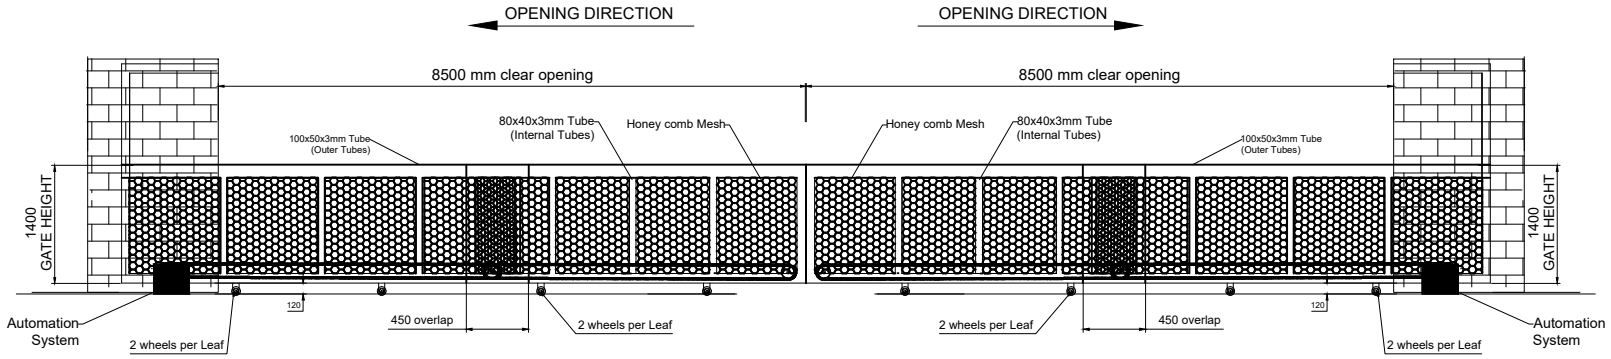


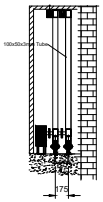

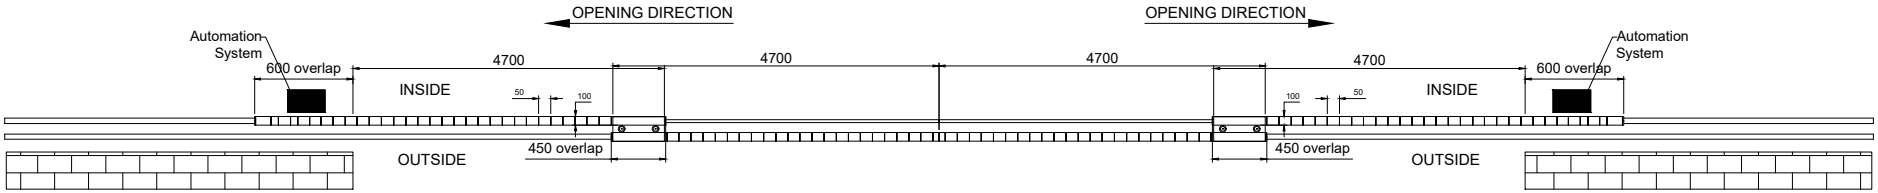

Clear Opening size - 17000mm x 1400mm
Total No. of Leaf - 4 Leaf
Factory paint finish - Red oxide primer coat
NOTE :- *ALL REQ. CIVIL WORK WILL BE IN CLIENT SCOPE.

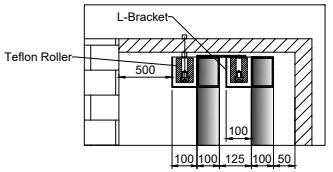

This drawing & designing is the property of NIHVA TECHNOLOGIES. Not be sold or copy to any other concern.

TITLE	TELESCOPIC SLIDING GATE		
	SIGN	DATE	
DRAWN	J.P	15/10/25	CLIENT - KOHLI VILLA
CHECK	B.S	15/10/25	PROJECT - TELESCOPIC SLIDING GATE
REV.	00		SITE -
APPROVAL			DWG. NO. : NIHVA/15-16/178
If any queries contact : projects@nihva.com			SCALE: 01 / WT: / SHEET: 01 OF 01
ALL DIMENSION ARE IN mm			

NIHVA TECHNOLOGY PVT. LTD. PUNE
Tel : 020 66304033
Email:- info@nihva.com
Website:- www.nihva.com