


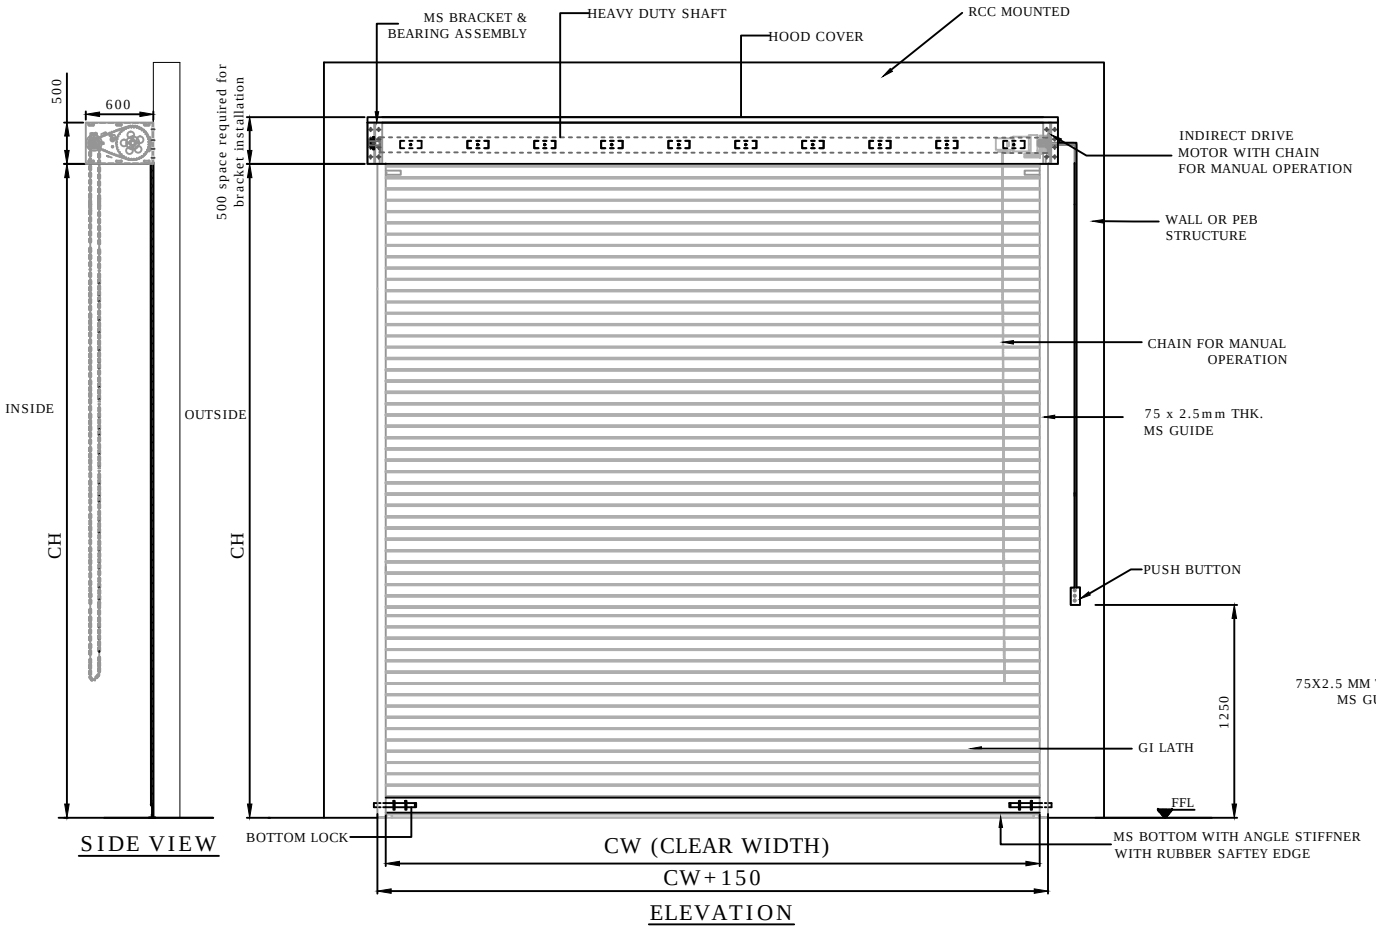


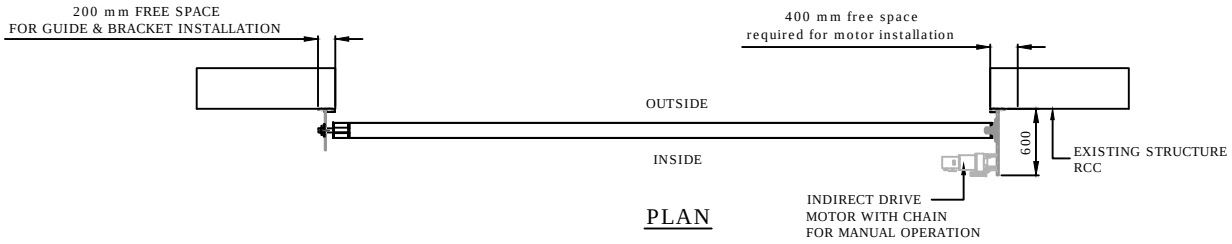

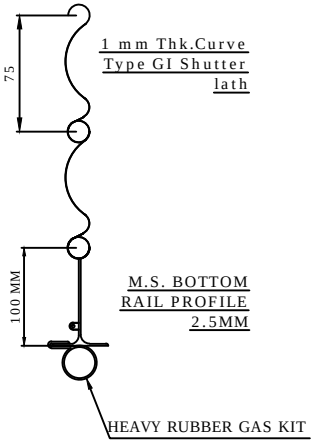

M.S. BOTTOM RAIL PROFILE 2.5MM

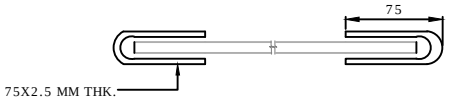

RAL Code - 7035 Grey

CLEAR WIDTH (CW)	CLEAR HEIGHT (CH)	QUANTITY
3000mm	3000mm	10 NOS
2400mm	3000mm	01 NOS

DIMENSION :

CLEAR WIDTH	CLEAR HEIGHT	QUANTITY
3000	3000	10 NOS
2400	3000	01 NOS

MATERIAL:

THICKNESS :

NOTE:
1. REQUIRED STRUCTURE FOR ROLLING SHUTTER WILL BE CLIENT'S SCOPE.
2. ONE COAT OF RED OXIDE PRIMER WILL BE GIVEN TO THE SHUTTER.
3. SINGLE PHASE. 3 CORE 1.5 SQ. CABLE REQUIRE AT SITE(CLIENT'S SCOPE)
4. FINAL FINISH WILL BE AS SUPPLIED EARLIER.

NIHVA TECHNOLOGIES PVT. LTD.
NIHVA TECHNOLOGIES PVT. LTD. PUNE
Email:- info@nihva.com
Website:- www.nihva.com

TITLE:

MOTORIZED ROLLING SHUTTER

CLIENT'S APPROVAL :

CLIENT -

PROJECT -

SITE LOCATION -

DWG. NO. : NIHVA/18-19/VDR/376

SCALE: NTS	WT:	SHEET:1 OF 1

DRAWN BY: P.A	DATE: 07.02.2019
CHECK BY : P.A.	DATE: 07.02.2019
APPROVED BY :	DATE:

If any queries contact : projects@nihva.com

NOTE: ALL DIMENSIONS ARE IN mm

THIS DRAWING & DESIGN IS THE PROPERTY OF NIHVA TECHNOLOGIES. NOT TO BE SOLD OR COPIED TO ANY OTHER CONCERN.